D.V.	Nº TAL.	DATA PL.	ÁREA (ha)	VARIEDADE
6.45%	1	05/2024	38.11	CTC 04
	2		44.42	
	3		28.33	
TOTAL PLANTIO			110.86	

ÁREAS	(ha)	(%)
PLANTIO	110.86	93.79
CARREADORES	6.27	5.31
OUTROS	0.00	0.00
SUB TOTAL AGRICULTÁVEL	117.13	99.09
AP.P.	0.92	0.78
ÁRVORES	0.15	0.13
OUTROS	0.00	0.00
SUB TOTAL NÃO AGRICULT.	1.07	0.91
ÁREA TOTAL	118.20	100.00


C. NÍVEL: 11265.90 m/l 2.59 ha 2.19 %

LEGENDA

- FAZENDA
- TALHÃO
- REDE ELÉTRICA
- TERRAÇO BASE LARGA
- TERRAÇO EMBUTIDO


ESPAÇAMENTO: 0.00 x 0.00

TIRO MÉDIO ESTIMADO: 000.00 m

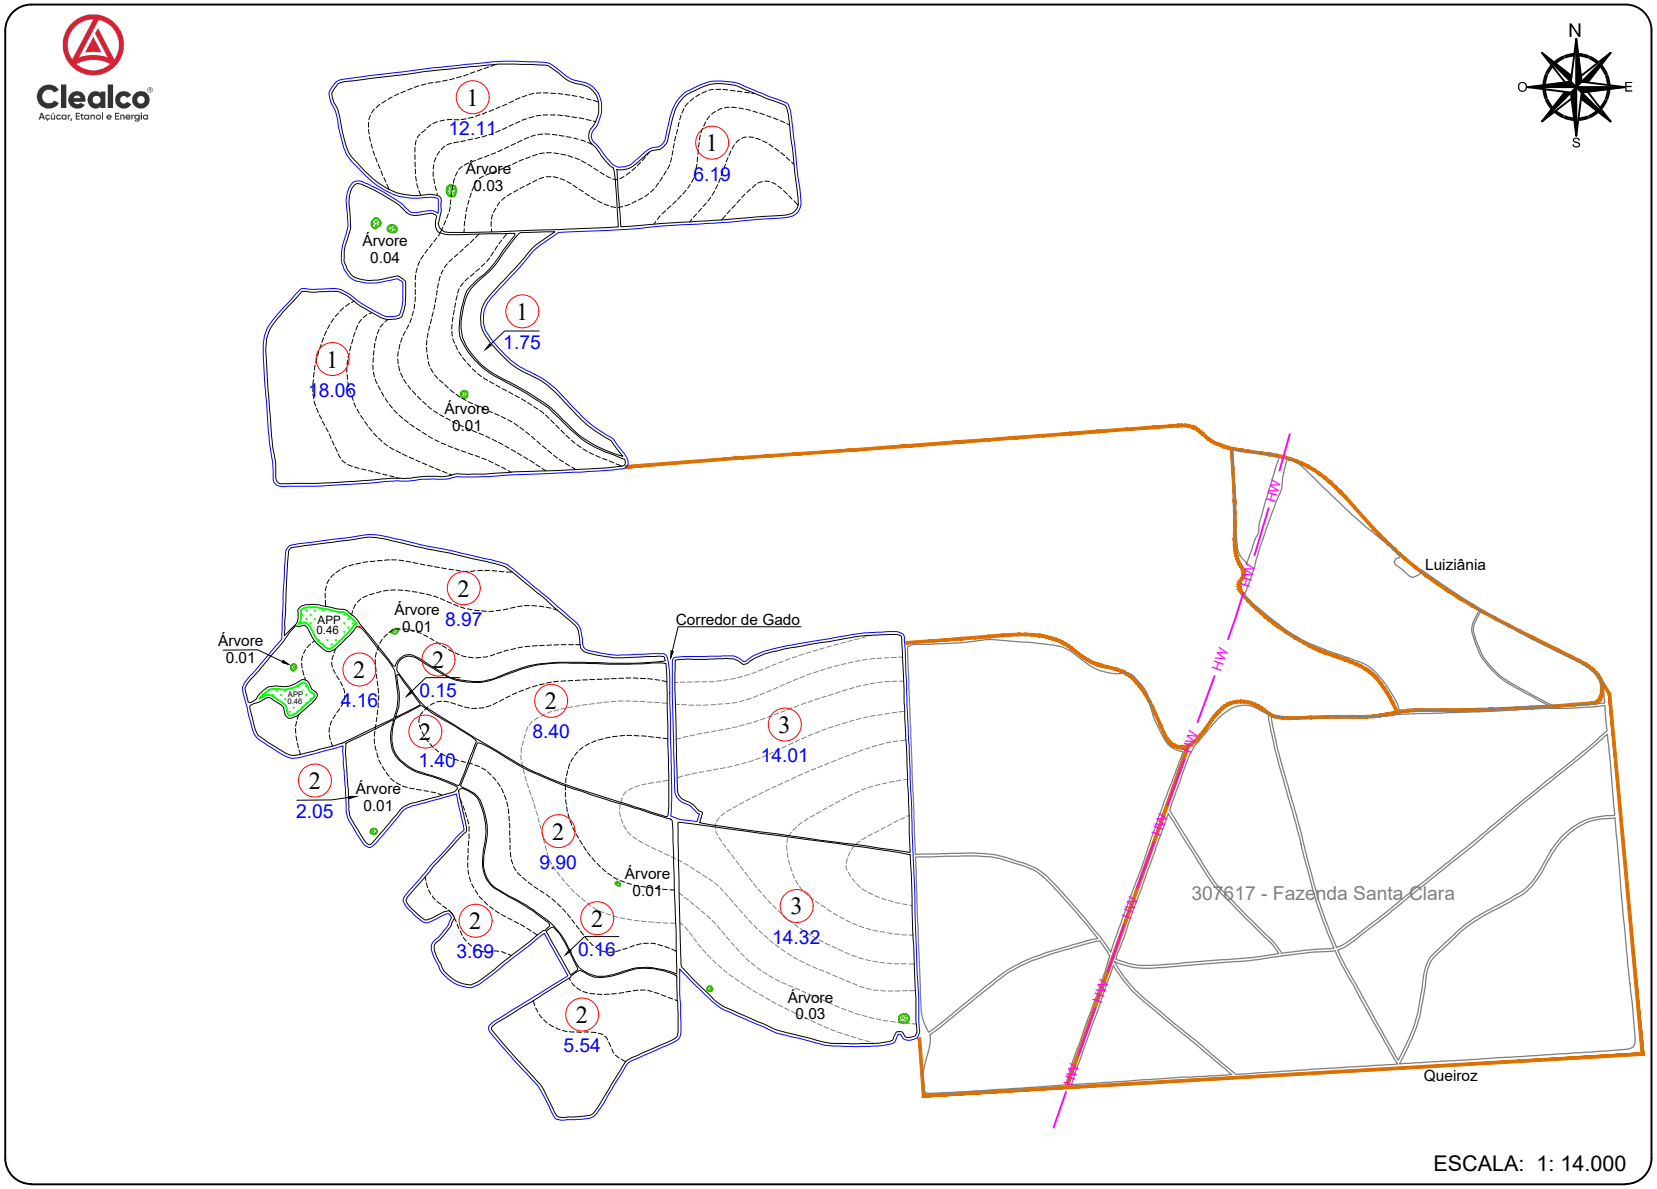

ESCALA: 1: 14.000

CROQUI DE ACESSO

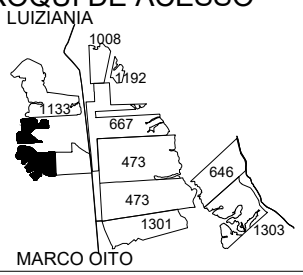

FAZENDA SANTA CLARA IV

PROPRIETÁRIO: FRANCISCO GARCIA SOLER FILHO
COMPRADOR: CLEALCO S/A
MUNICÍPIO: ARCO-IRIS

DISTÂNCIAS (km):
UNID. I - Asfalto: 33.30 Terra.: 12.00
UNID.I I - Asfalto: 16.50 Terra.: 15.00

COORDENADAS: E(X): 567500.45 N(Y): 7594936.56
LAT: -21°44'52.3589" LONG: -50°20'49.9771"

CLEALCO - AÇÚCAR E ALCOOL S/A - DEPARTAMENTO DE GEOTECNOLOGIA

UNIDADE: II

PARTE: A/A

FUNDO AGRÍCOLA: 307757