| D.V. | Nº TAL. | DATA PL. | ÁREA (ha) | VARIEDADE |
|---|---|---|---|---|
| 4.67% | 1 | 03/2025 | 23.61 | RB 975242 |
|  |  |  |  |  |
|  |  |  |  |  |
| TOTAL PLANTIO |  |  | 23.61 |  |

| ÁREAS | (ha) | (%) |
|---|---|---|
| PLANTIO | 23.61 | 95.50 |
| CARREADORES | 1.00 | 4.06 |
| OUTROS | 0.00 | 0.00 |
| SUB TOTAL AGRICULTÁVEL | 24.61 | 99.56 |
| AP.P. | 0.00 | 0.00 |
| ÁRVORES | 0.11 | 0.44 |
| OUTROS | 0.00 | 0.00 |
| SUB TOTAL NÃO AGRICULT. | 0.11 | 0.44 |
| ÁREA TOTAL | 24.72 | 100.00 |

| C. NÍVEL: | 3383.19 m/l | 0.78 ha | 3.15 % |
|---|---|---|---|

## LEGENDA

- 🟦 FAZENDA
- ▬ TALHÃO
- -·- REDE ELÉTRICA
- ▪▪▪▪ TERRAÇO BASE LARGA
- — TERRAÇO EMBUTIDO

| | |
|---|---|
| ESPAÇAMENTO: | 1.50 x 1.50 |
| TIRO MÉDIO ESTIMADO: | 290.90 m |

**Clealco**
Açúcar, Etanol e Energia

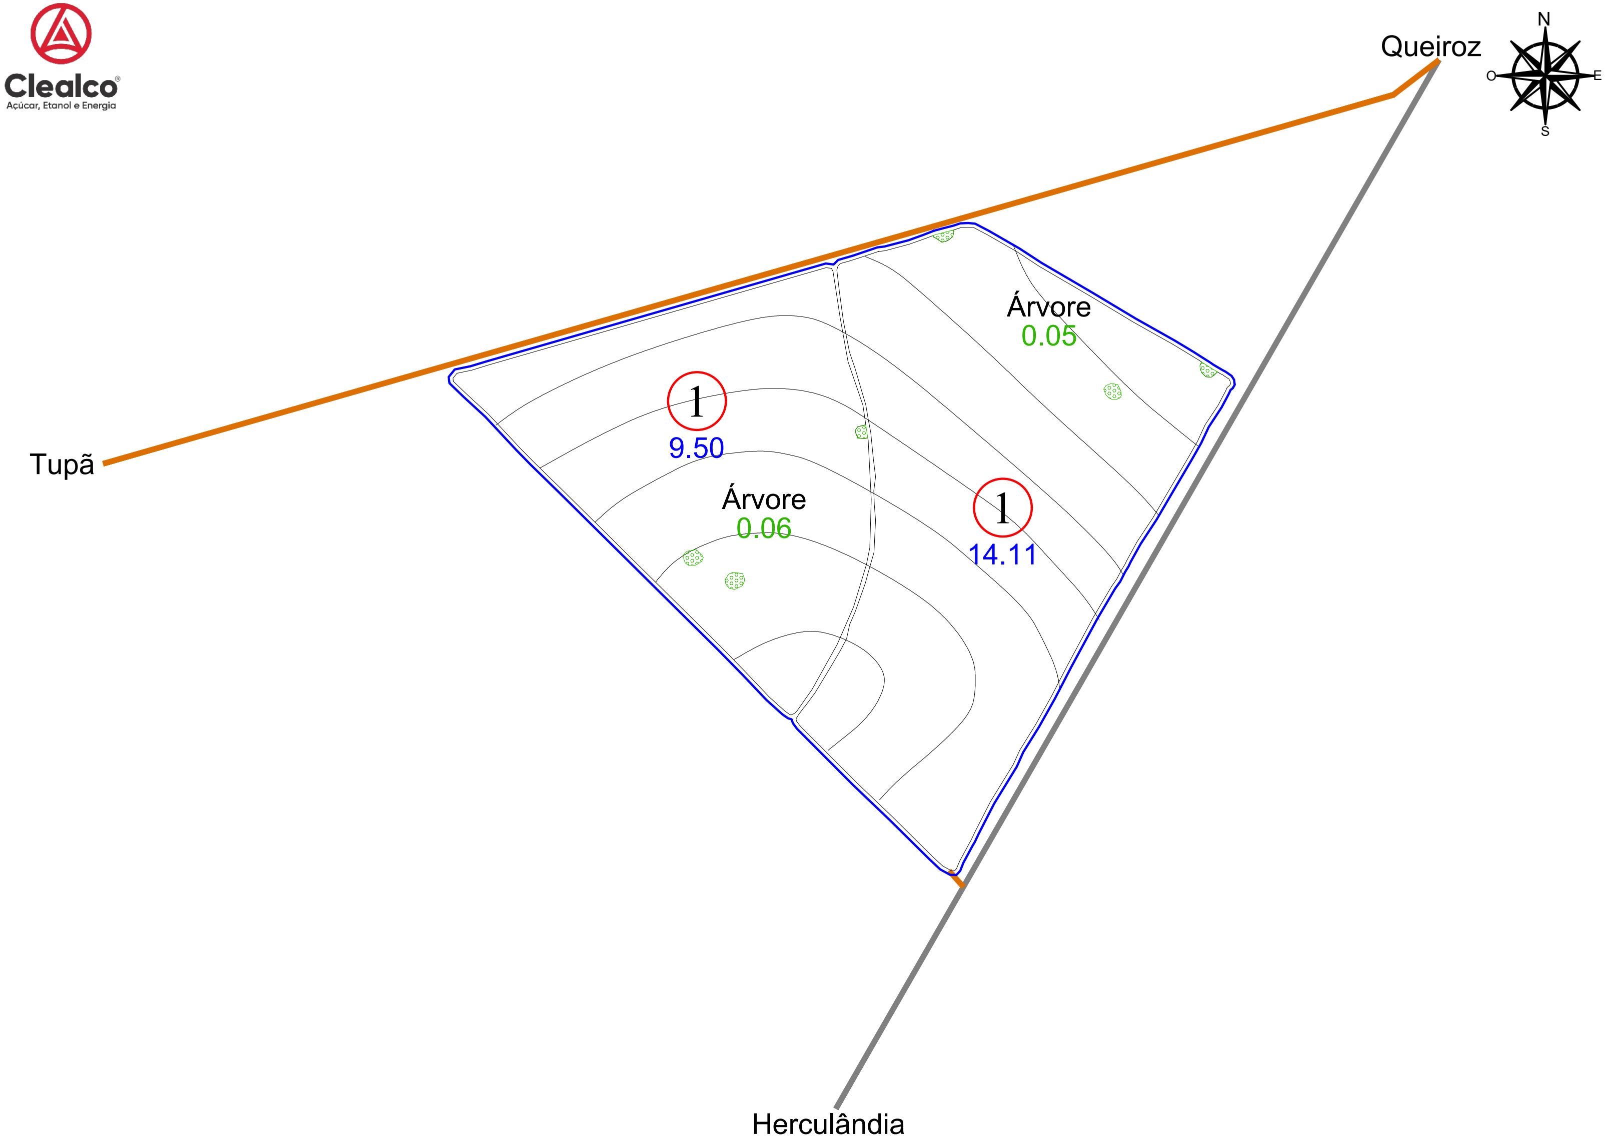

ESCALA: 1: 7.500

## CROQUI DE ACESSO

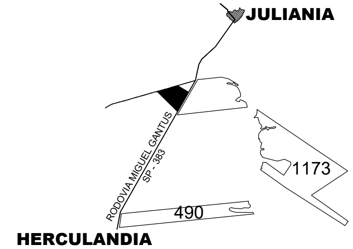

# SÍTIO SÃO SEBASTIÃO

PROPRIETÁRIO: REGINALDO VIANA RODRIGUES
COMPRADOR: CLEALCO S/A
MUNICÍPIO: TUPÃ- SP

DISTÂNCIAS (km):

| | | | | |
|---|---|---|---|---|
| UNID. I - | Asfalto: | 41.00 | Terra.: | 23.50 |
| UNID.I I - | Asfalto: | 25.50 | Terra.: | 1.00 |
| UNID. III - | Asfalto: | 145.00 | Terra.: | 1.00 |

COORDENADAS: E(X): 564019.59 N(Y): 7575882.31
LAT: -21°55'12.5295" LONG: -50°22'48.4884"

CLEALCO - AÇÚCAR E ALCOOL S/A - DEPARTAMENTO DE GEOTECNOLOGIA

UNIDADE:
II

PARTE:
A/A

FUNDO AGRÍCOLA:
307759

M:\01-Mapa de safra\Mapas Atualizados\Spot\307759 - Sítio São Sebastião - Reginaldo Viana Rodrigues\307759 - Sítio São Sebastião - Reginaldo Viana Rodrigues.dwg

Benati 11/07/2025