
Clealco
Açúcar, Etanol e Energia

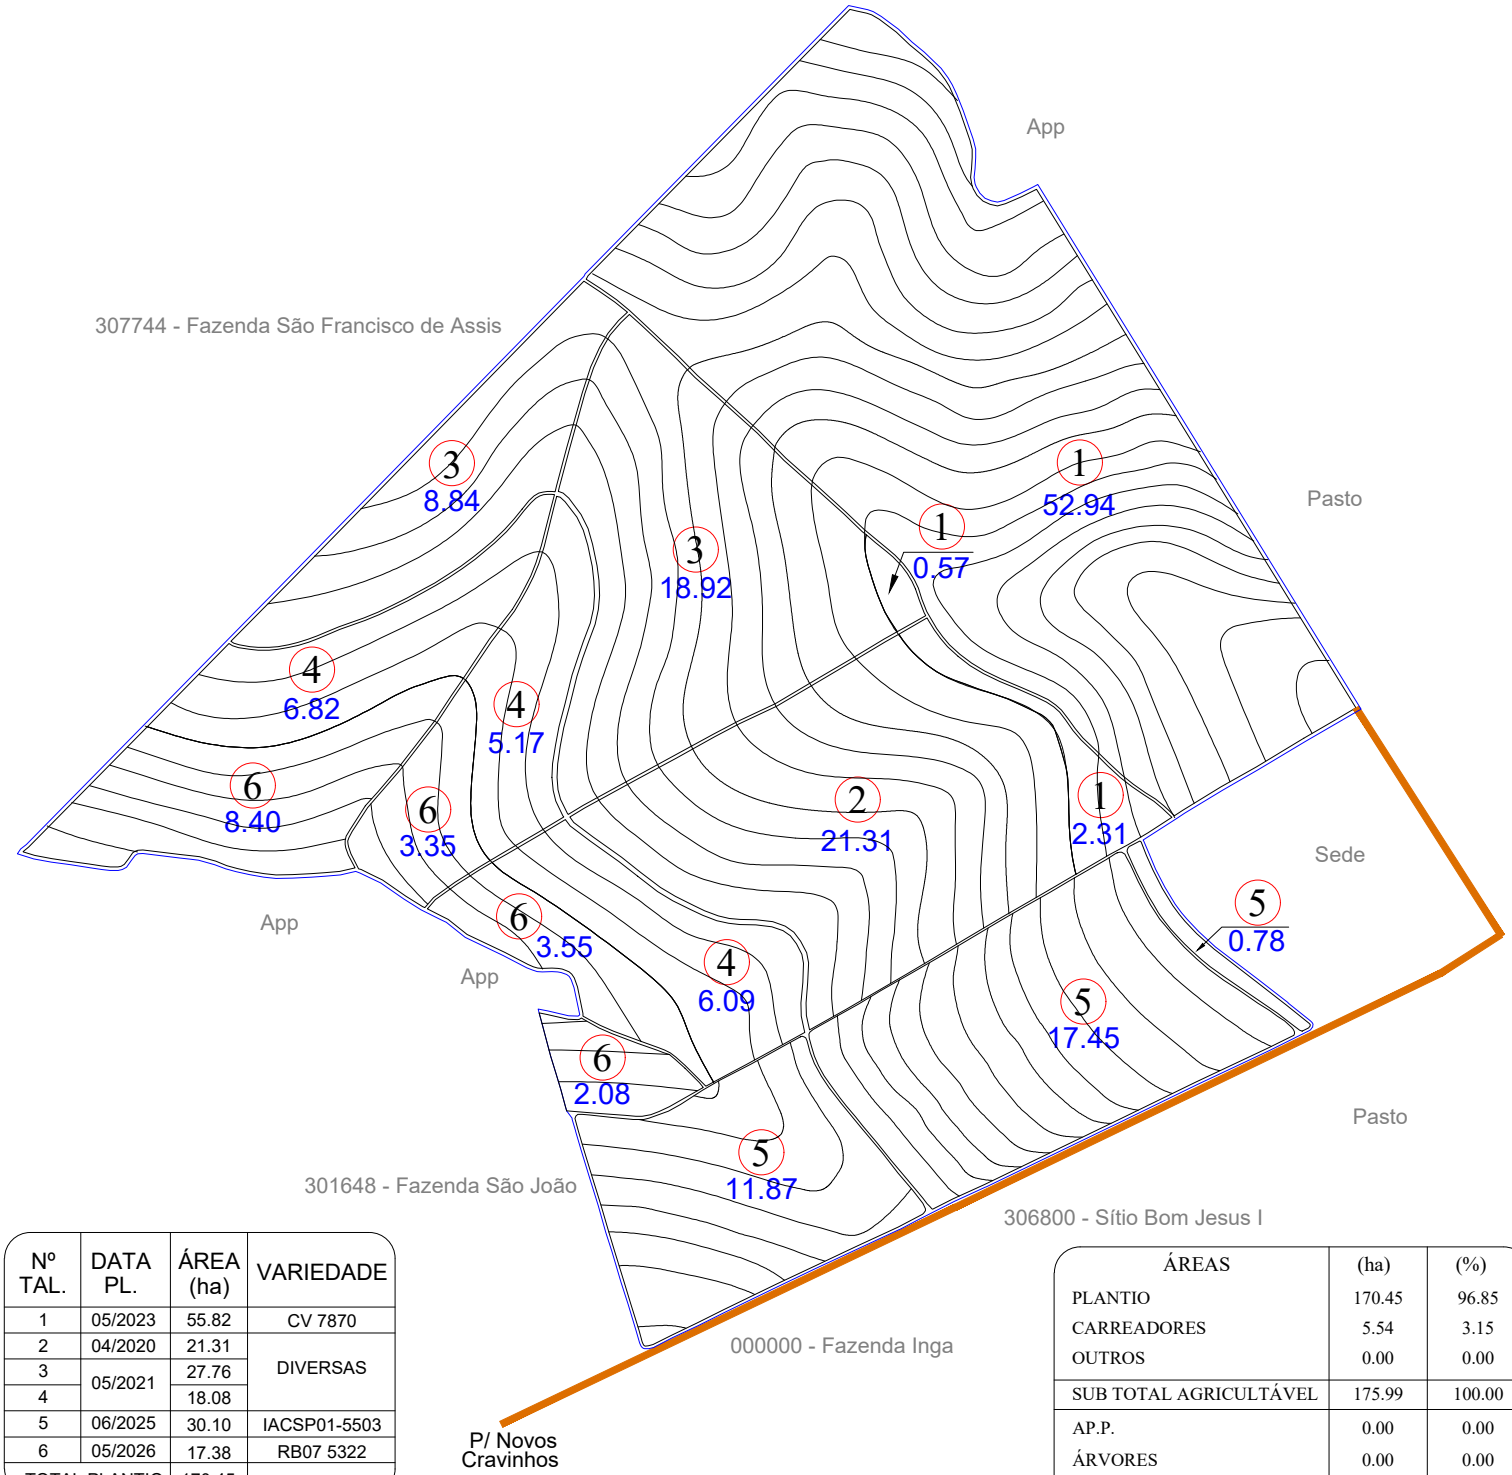

Nº TAL.	DATA PL.	ÁREA (ha)	VARIEDADE
1	05/2023	55.82	CV 7870
2	04/2020	21.31	DIVERSAS
3	05/2021	27.76	
4		18.08	
5	06/2025	30.10	IACSP01-5503
6	05/2026	17.38	RB07 5322
TOTAL PLANTIO		170.45	

ÁREAS	(ha)	(%)
PLANTIO	170.45	96.85
CARREADORES	5.54	3.15
OUTROS	0.00	0.00
SUB TOTAL AGRICULTÁVEL	175.99	100.00
AP.P.	0.00	0.00
ÁRVORES	0.00	0.00
OUTROS	0.00	0.00
SUB TOTAL NÃO AGRICULT.	0.00	0.00
ÁREA TOTAL	175.99	100.00

LEGENDA


- FAZENDA
- TALHÃO
- REDE ELÉTRICA
- TERRAÇO BASE LARGA
- TERRAÇO EMBUTIDO
- (P.O.A) PATIO DE OPERAÇÃO

ESPAÇAMENTO: 1.50 x 1.50
TIRO MÉDIO ESTIMADO: 305.87 m
D.V: 5.49 %

C. NÍVEL: 36011.57 m/l 8.28 ha 4.71 %

ESCALA: 1: 11.000

CROQUI DE ACESSO

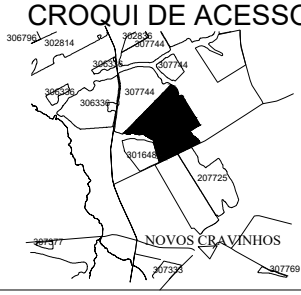

FAZENDA NOSSA SENHORA DE FÁTIMA

PROPRIETÁRIO: ARNALDO ZANCHETTIN
COMPRADOR: CLEALCO
MUNICÍPIO: POMPÉIA - SP

DISTÂNCIAS (km):
UNID. I - Asfalto: 83.30 Terra.: 1.20
UNID.I I - Asfalto: 26.30 Terra.: 1.20

COORDENADAS: E(X): 590859.79 N(Y): 7571525.86
LAT: -21°57'29.9406" LONG: -50°7'12.1277"

CLEALCO - AÇÚCAR E ALCOOL S/A - DEPARTAMENTO DE GEOTECNOLOGIA

LEVANTAMENTO VIA:
- SATÉLITE
- GPS / VANT
- GOOGLE

UNIDADE: II
PARTE: A/A
FUNDO AGRÍCOLA: 307827

M:\01-Mapa de safra\Mapas Atualizados\Terceiro\307827 - Fazenda Nossa Senhora De Fátiama (Arnaldo Zanchettin)\307827 - Fazenda Nossa Senhora De Fátiama (Arnaldo Zanchettin).dwg

Bruno Gamboa 08/07/26