
Clealco
Açúcar, Etanol e Energia

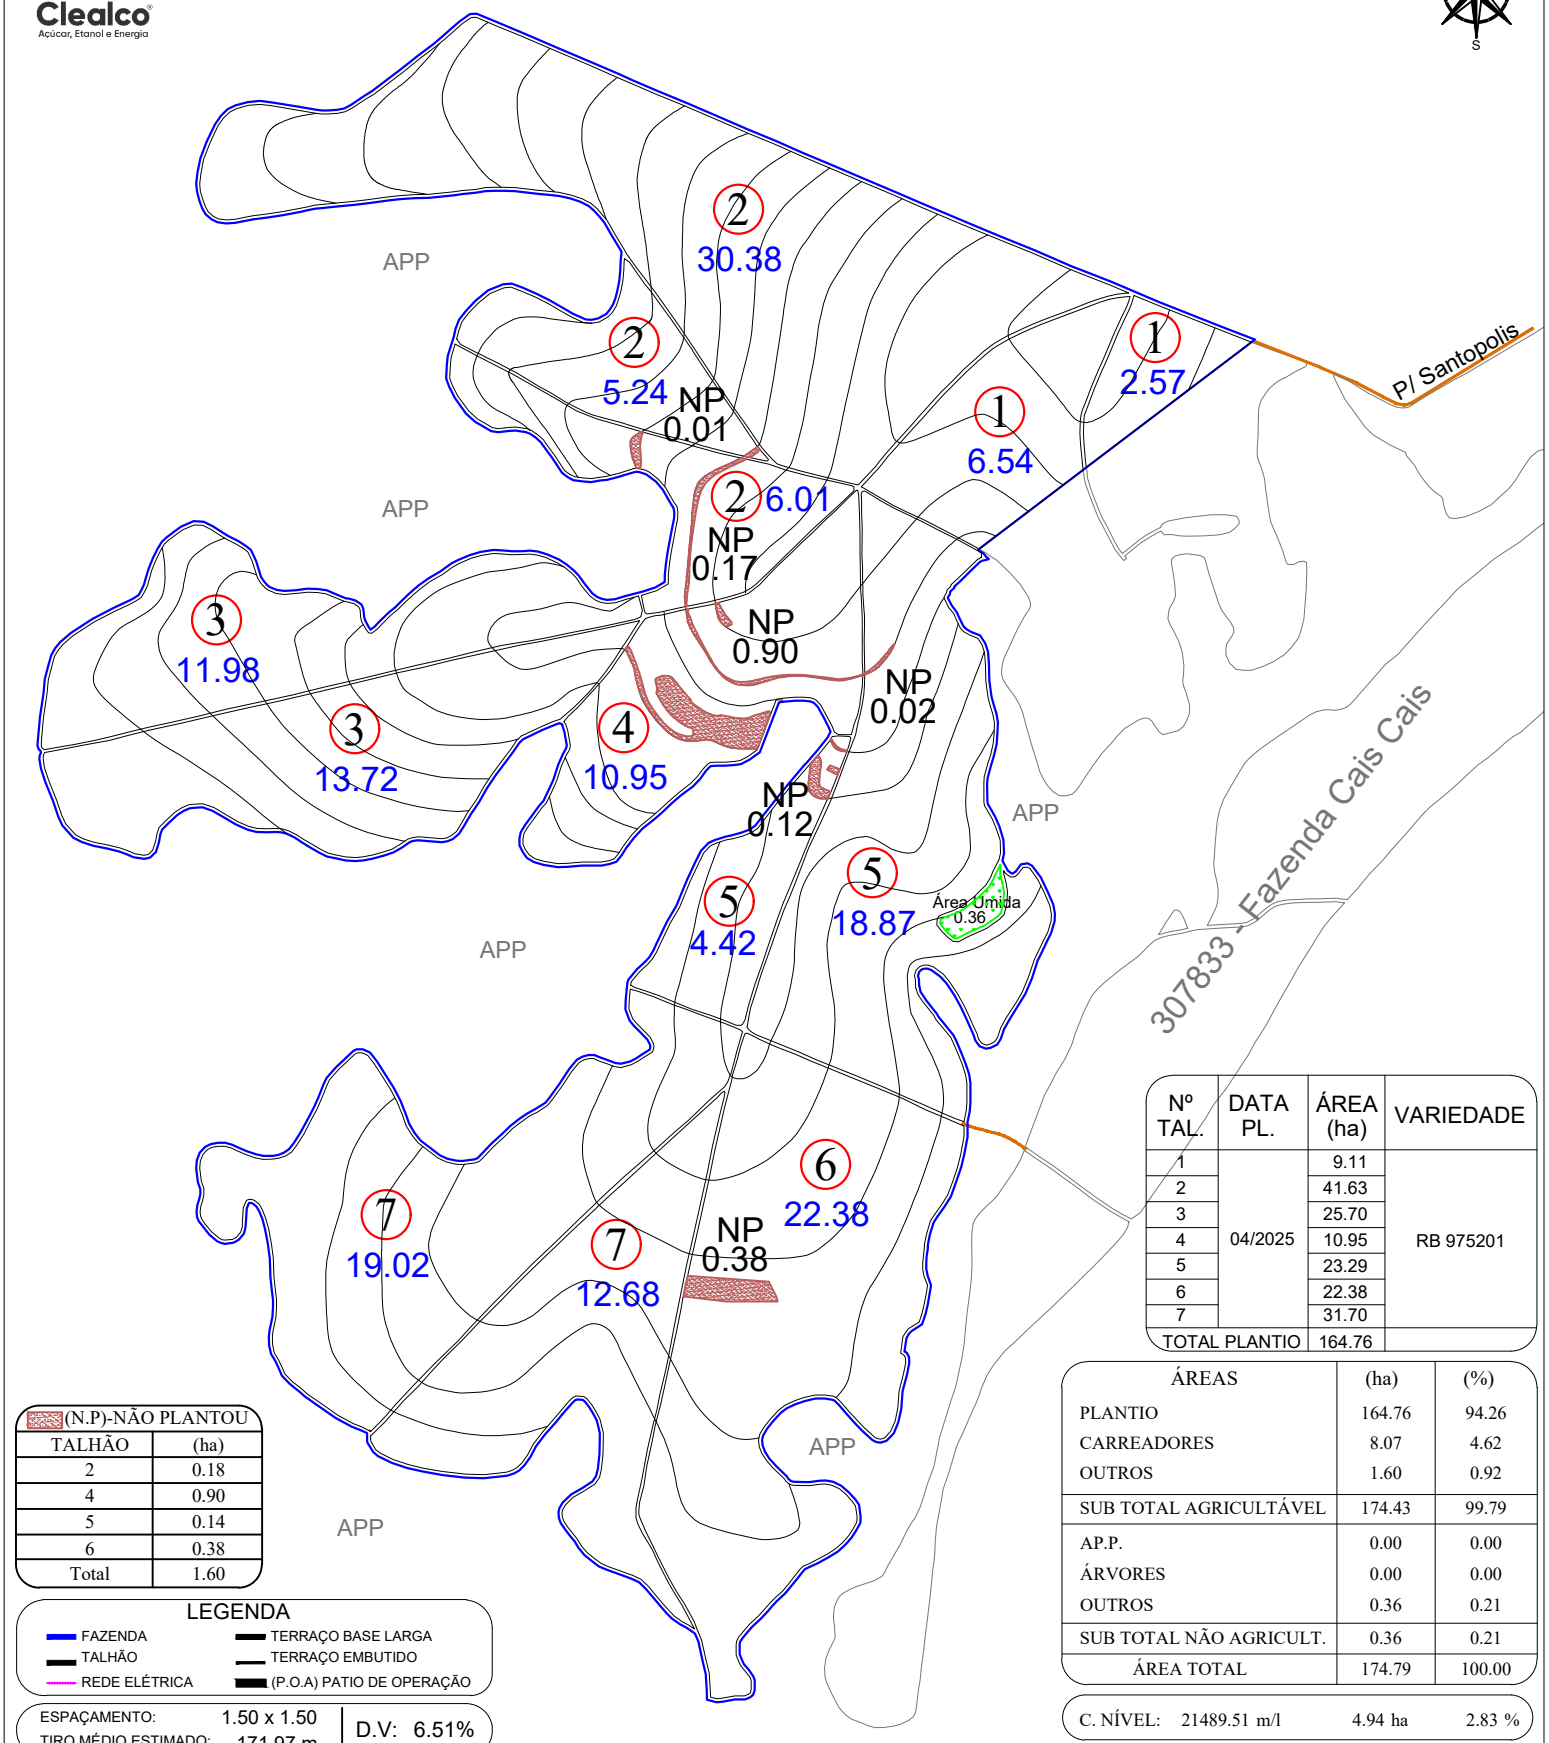

Nº TAL.	DATA PL.	ÁREA (ha)	VARIEDADE
1	04/2025	9.11	RB 975201
2		41.63	
3		25.70	
4		10.95	
5		23.29	
6		22.38	
7		31.70	
TOTAL PLANTIO		164.76	

(N.P)-NÃO PLANTOU	
TALHÃO	(ha)
2	0.18
4	0.90
5	0.14
6	0.38
Total	1.60

ÁREAS	(ha)	(%)
PLANTIO	164.76	94.26
CARREADORES	8.07	4.62
OUTROS	1.60	0.92
SUB TOTAL AGRICULTÁVEL	174.43	99.79
AP.P.	0.00	0.00
ÁRVORES	0.00	0.00
OUTROS	0.36	0.21
SUB TOTAL NÃO AGRICULT.	0.36	0.21
ÁREA TOTAL	174.79	100.00

LEGENDA


- FAZENDA
- TALHÃO
- REDE ELÉTRICA
- TERRAÇO BASE LARGA
- TERRAÇO EMBUTIDO
- (P.O.A) PATIO DE OPERAÇÃO

ESPAÇAMENTO: 1.50 x 1.50
TIRO MÉDIO ESTIMADO: 171.97 m
D.V: 6.51%

C. NÍVEL: 21489.51 m/l 4.94 ha 2.83 %

ESCALA: 1: 11.000

CROQUI DE ACESSO

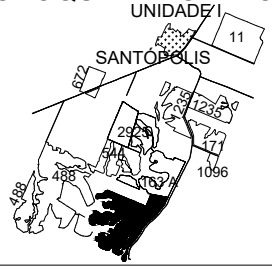

FAZENDA BEIRA RIO

PROPRIETÁRIO: JOSÉ SOARES
COMPRADOR: CLEALCO
MUNICÍPIO: SANTÓPOLIS DO AGUAPEÍ

DISTÂNCIAS (km):
UNID. I - Asfalto: 12.00 Terra.: 05.00
UNID.I I - Asfalto: 45.00 Terra.: 05.00

COORDENADAS: E(X): 549993.00 N(Y): 7600836.59
LAT: -21°41'42.5563" LONG: -50°31'0.1195"

CLEALCO - AÇÚCAR E ALCOOL S/A - DEPARTAMENTO DE GEOTECNOLOGIA

UNIDADE: I
PARTE: A/A
FUNDO AGRÍCOLA: 307832

M:\01-Mapa de safra\Mapas Atualizados\Terceiro\307832 - Fazenda Beira Rio - (José Soares)\307832 - Fazenda Beira Rio - (José Soares).dwg

Bruno Gamboa 01/07/25