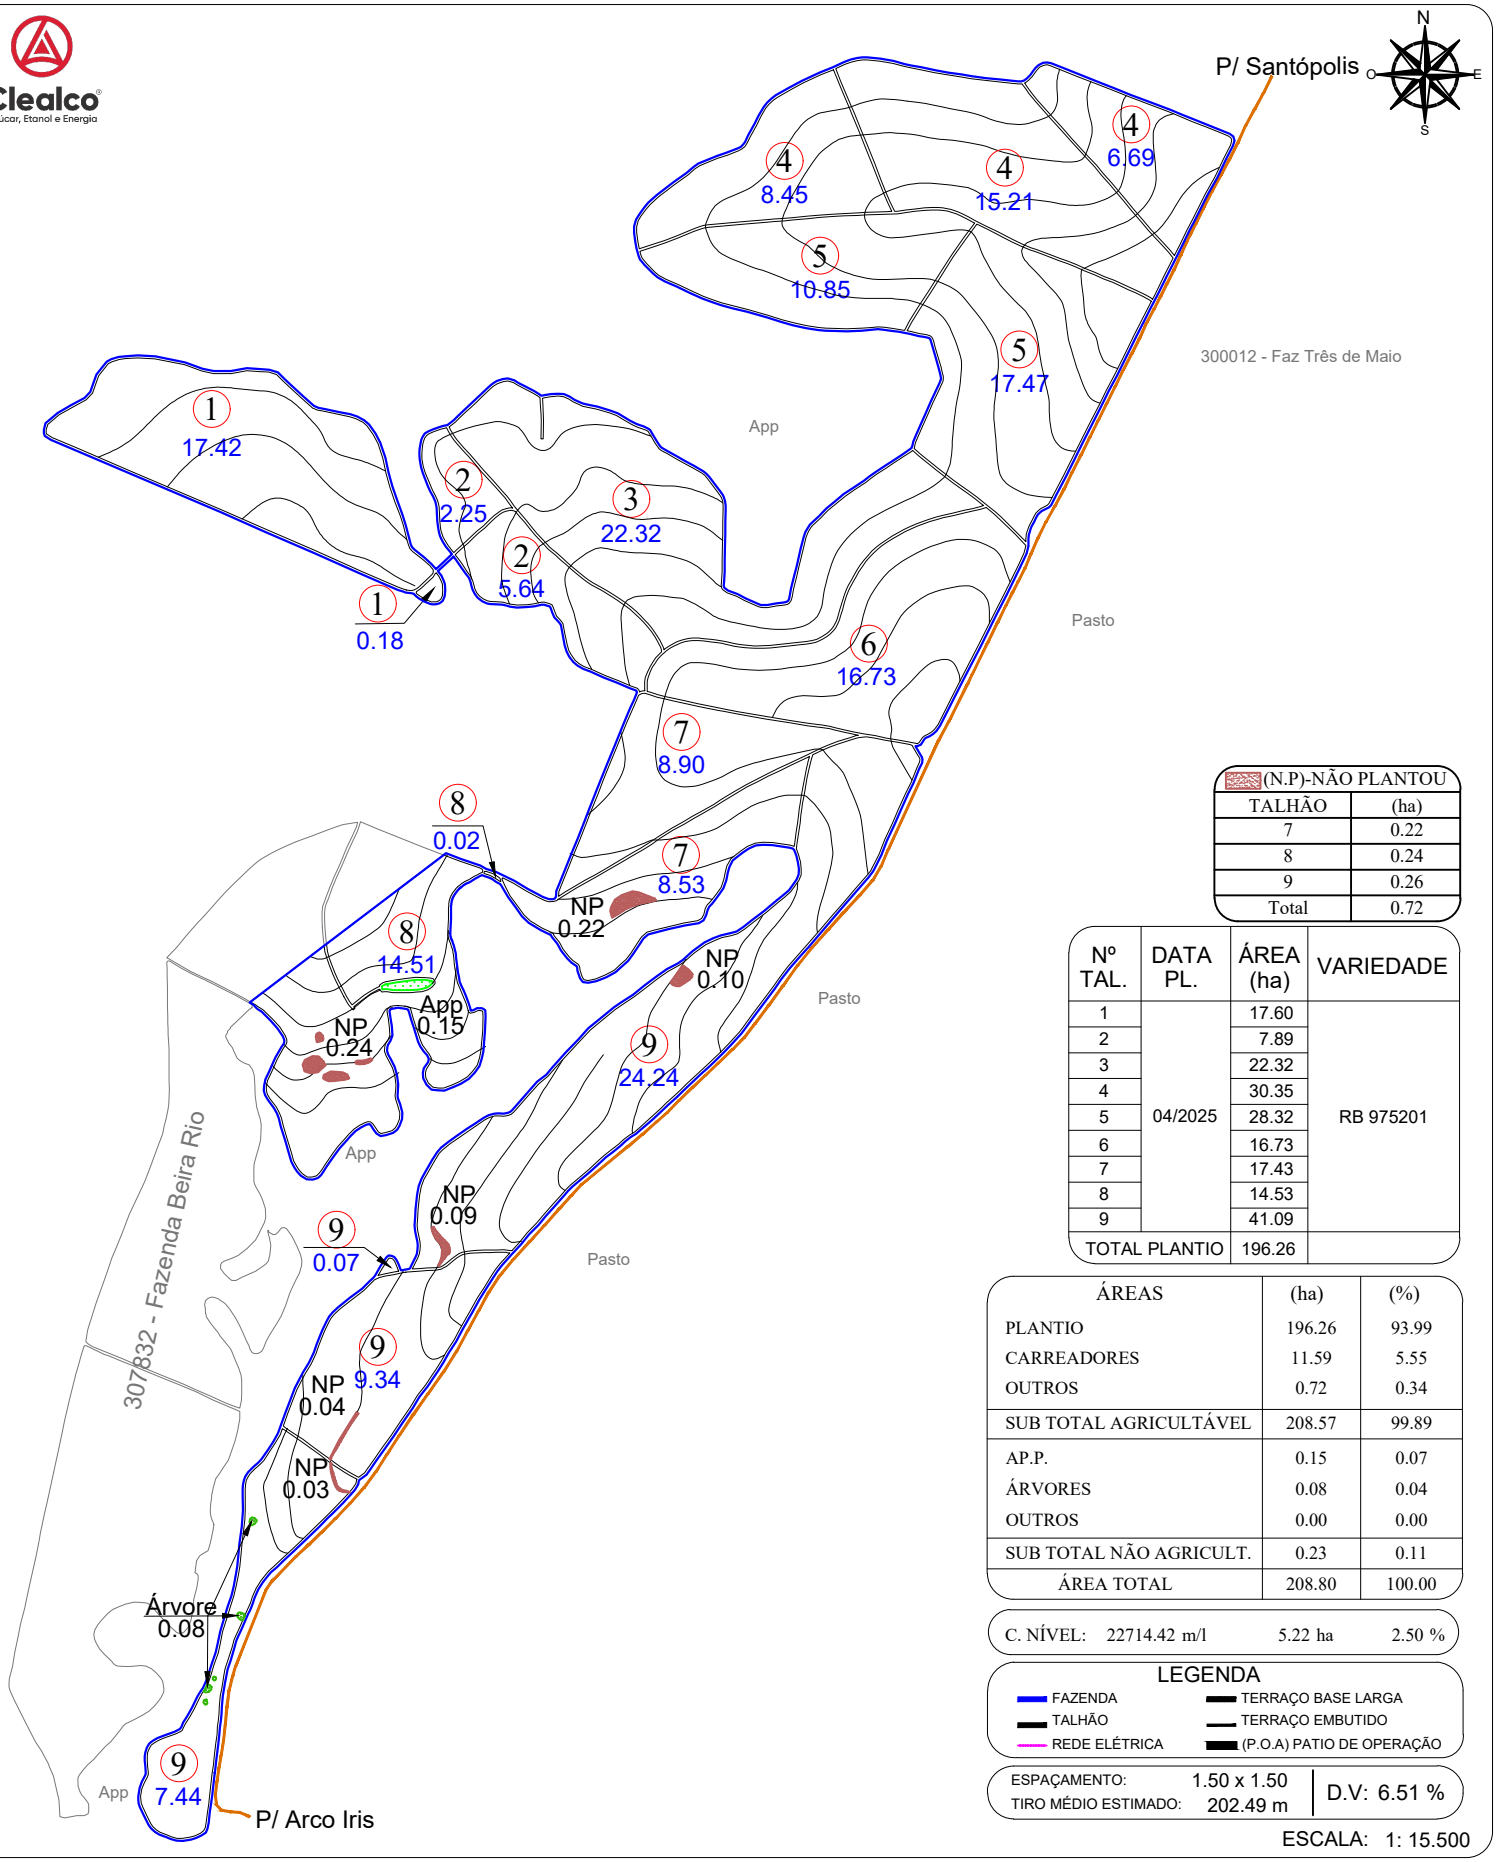


(N.P)-NÃO PLANTOU	
TALHÃO	(ha)
7	0.22
8	0.24
9	0.26
Total	0.72

Nº TAL.	DATA PL.	ÁREA (ha)	VARIEDADE
1	04/2025	17.60	RB 975201
2		7.89	
3		22.32	
4		30.35	
5		28.32	
6		16.73	
7		17.43	
8		14.53	
9		41.09	
TOTAL PLANTIO		196.26	

ÁREAS	(ha)	(%)
PLANTIO	196.26	93.99
CARREADORES	11.59	5.55
OUTROS	0.72	0.34
SUB TOTAL AGRICULTÁVEL	208.57	99.89
AP.P.	0.15	0.07
ÁRVORES	0.08	0.04
OUTROS	0.00	0.00
SUB TOTAL NÃO AGRICULT.	0.23	0.11
ÁREA TOTAL	208.80	100.00

C. NÍVEL: 22714.42 m/l 5.22 ha 2.50 %


LEGENDA

- FAZENDA
- TALHÃO
- REDE ELÉTRICA
- TERRAÇO BASE LARGA
- TERRAÇO EMBUTIDO
- (P.O.A) PATIO DE OPERAÇÃO

ESPAÇAMENTO: 1.50 x 1.50
TIRO MÉDIO ESTIMADO: 202.49 m
D.V: 6.51 %

ESCALA: 1: 15.500

CROQUI DE ACESSO

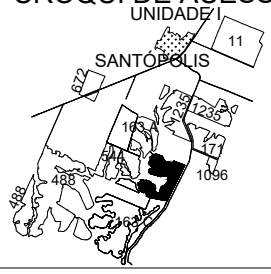

FAZENDA CAIS CAIS

PROPRIETÁRIO: JOSE SOARES
COMPRADOR: CLEALCO
MUNICÍPIO: SANTÓPOLIS DO AGUAPEÍ

DISTÂNCIAS (km):
UNID. I - Asfalto: 12.00 Terra.: 5.00
UNID.I I - Asfalto: 45.00 Terra.: 5.00

COORDENADAS: E(X): 550448.22 N(Y): 7601377.06
LAT: -21°41'24.9316" LONG: -50°30'44.3364"

CLEALCO - AÇÚCAR E ALCOOL S/A - DEPARTAMENTO DE GEOTECNOLOGIA

UNIDADE: I
PARTE: A/A
FUNDO AGRÍCOLA: 307833

M:\01-Mapa de safra\Mapas Atualizados\Terceiro\307833 - Fazenda Cais Cais (José Soares)\307833 - Fazenda Cais Cais - (Jose Soares).dwg

Bruno Gamboa 03/07/25