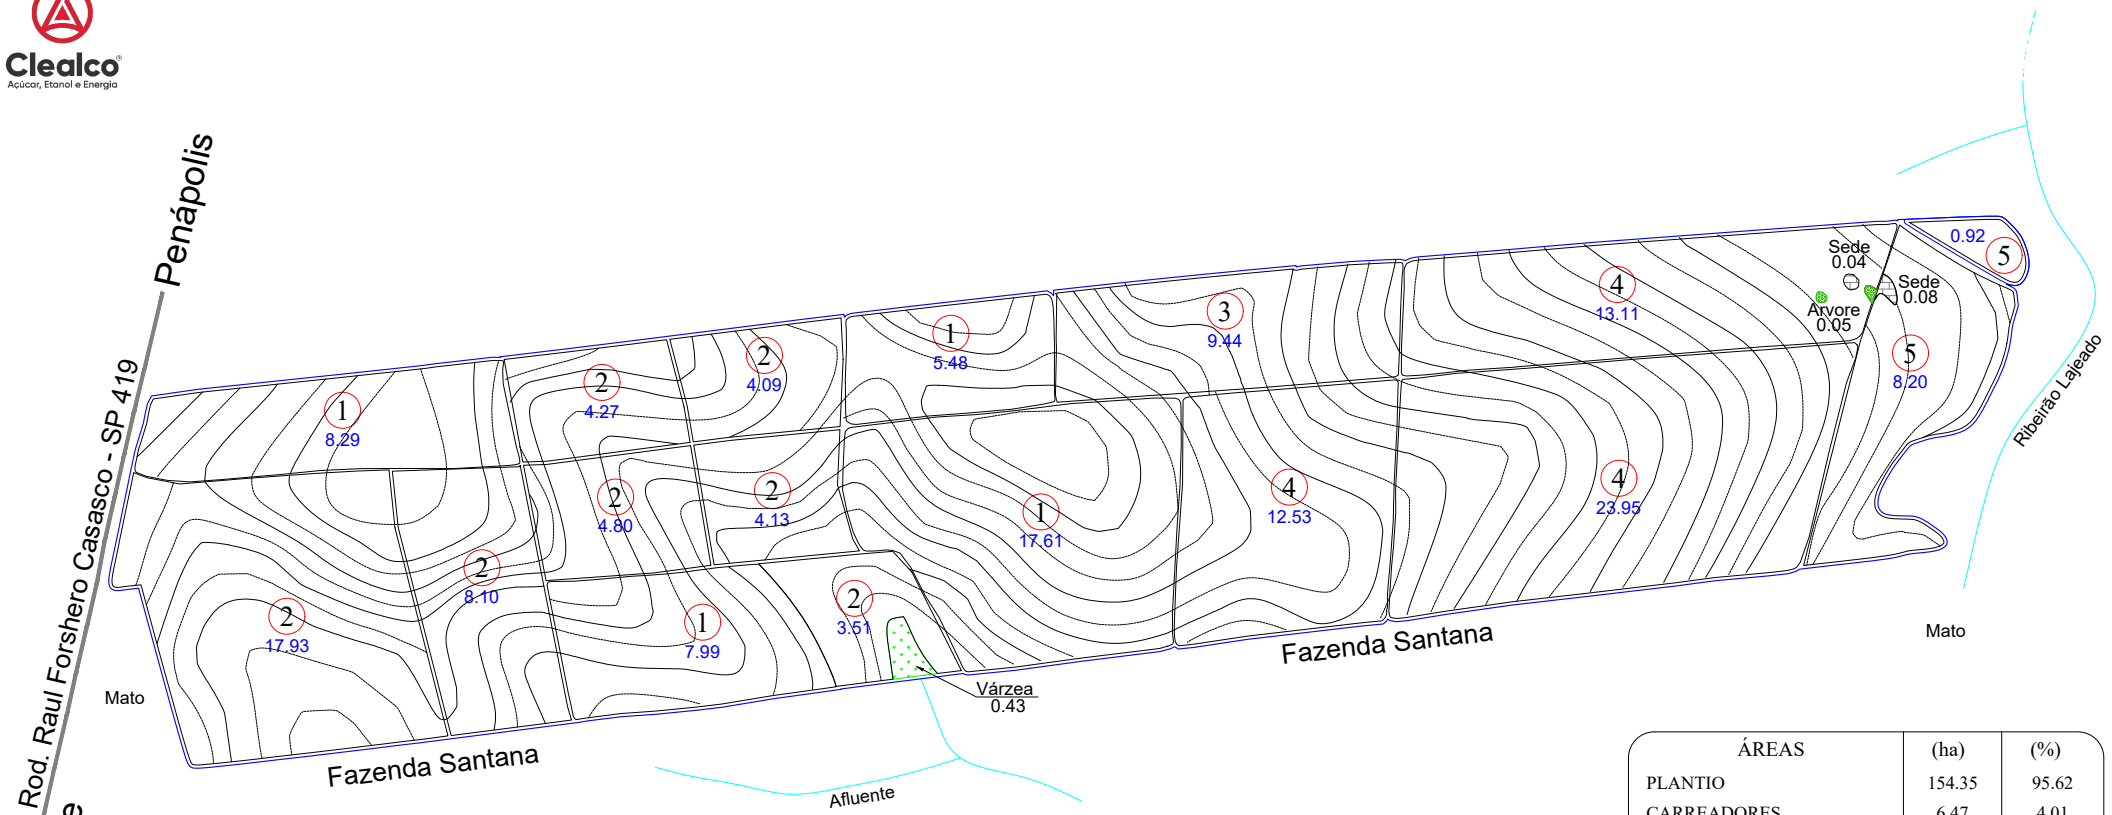


Nº TAL.	DATA PL.	ÁREA (ha)	VARIEDADE
1	03/2025	39.37	CV 7870
2	04/2022	46.83	RB867515
3	05/2024	9.44	CTC 04
4	03/2025	49.59	
5	2026	9.12	REFORMA
TOTAL PLANTIO		154.35	

ÁREAS	(ha)	(%)
PLANTIO	154.35	95.62
CARREADORES	6.47	4.01
OUTROS	0.00	0.00
SUB TOTAL AGRICULTÁVEL	160.82	99.63
AP.P.	0.00	0.00
ÁRVORES	0.00	0.00
OUTROS	0.60	0.37
SUB TOTAL NÃO AGRICULT.	0.60	0.37
ÁREA TOTAL	161.42	100.00

C. NÍVEL: 17159.09 m/l 3.95 ha 2.44 %


ESCALA: 1: 12.000

LEGENDA

- FAZENDA
- TALHÃO
- REDE ELÉTRICA
- TERRAÇO BASE LARGA
- TERRAÇO EMBUTIDO

ESPAÇAMENTO: 1.50 x 1.50 D.V: 0.00 %
TIRO MÉDIO ESTIMADO: 000.00 m

CROQUI DE ACESSO

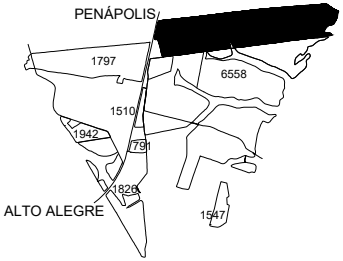

SITIO SÃO SEBASTIÃO

PROPRIETÁRIO: DANIEL G. DE ANDRADE
COMPRADOR: CLEALCO
MUNICÍPIO: PENAPOLIS - SP

DISTÂNCIAS (km):
UNID. I - Asfalto: 43.30 Terra.: 9.40
UNID.I I - Asfalto: 54.80 Terra.: 9.40

COORDENADAS: E(X): 592222.26 N(Y): 7617195.40
LAT: -21°32'44.4438" LONG: -50°6'33.8014"

CLEALCO - AÇÚCAR E ALCOOL S/A - DEPARTAMENTO DE GEOTECNOLOGIA

LEVANTAMENTO VIA:
SATÉLITE
GPS / VANT
GOOGLE

UNIDADE: II
PARTE: A/A
FUNDO AGRÍCOLA: 307839

M:\01-Mapa de safra\Mapas Atualizados\Terceiro\307839 - Sítio São Sebastião (Daniel Gallinari De Andrade)\307839 - Sítio São Sebastião (Daniel Gallinari De Andrade).dwg

Benati 04/03/2026