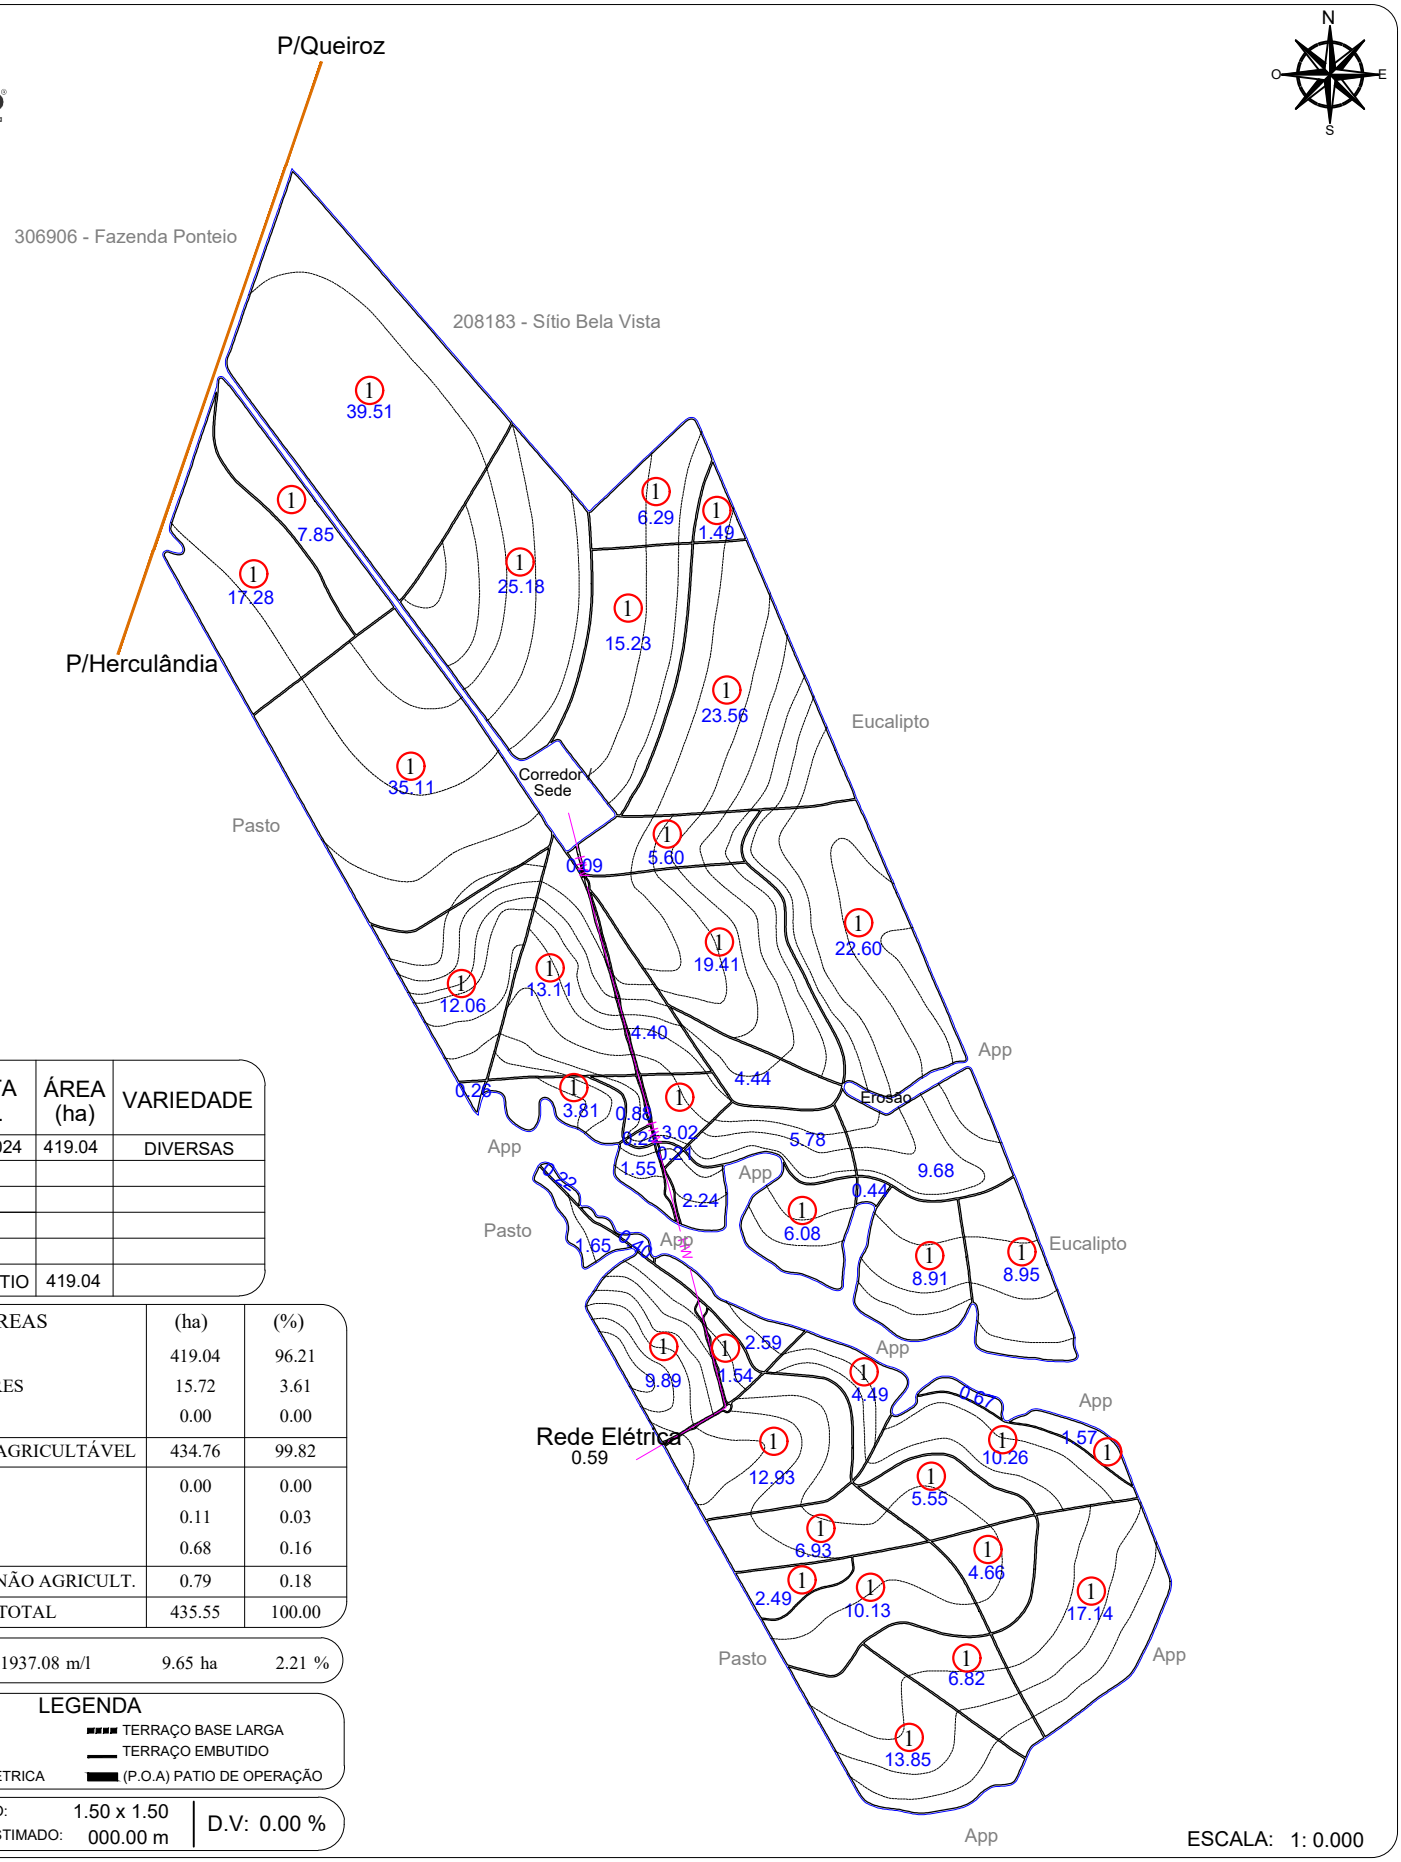


Nº TAL.	DATA PL.	ÁREA (ha)	VARIEDADE
1	04/2024	419.04	DIVERSAS
TOTAL PLANTIO		419.04	

ÁREAS	(ha)	(%)
PLANTIO	419.04	96.21
CARREADORES	15.72	3.61
OUTROS	0.00	0.00
SUB TOTAL AGRICULTÁVEL	434.76	99.82
AP.P.	0.00	0.00
ÁRVORES	0.11	0.03
OUTROS	0.68	0.16
SUB TOTAL NÃO AGRICULT.	0.79	0.18
ÁREA TOTAL	435.55	100.00

C. NÍVEL: 41937.08 m/l 9.65 ha 2.21 %


LEGENDA

- FAZENDA
- TALHÃO
- REDE ELÉTRICA
- TERRAÇO BASE LARGA
- TERRAÇO EMBUTIDO
- (P.O.A) PATIO DE OPERAÇÃO

ESPAÇAMENTO: 1.50 x 1.50
TIRO MÉDIO ESTIMADO: 000.00 m
D.V: 0.00 %

ESCALA: 1: 0.000

CROQUI DE ACESSO

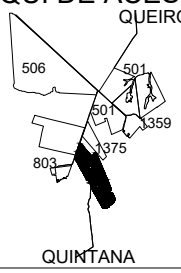

FAZENDA ESMERALDO

PROPRIETÁRIO: FELIPE FERRAZ E OUTROS
COMPRADOR: CLEALCO
MUNICÍPIO: HERCULÂNDIA - SP

DISTÂNCIAS (km):
UNID. I - Asfalto: 59.00 Terra.: 9.20
UNID.I I - Asfalto: 16.20 Terra.: 10.60

COORDENADAS: E(X): 575039.26 N(Y): 7572068.08
LAT: -21°57'15.0042" LONG: -50°16'23.7709"

CLEALCO - AÇÚCAR E ALCOOL S/A - DEPARTAMENTO DE GEOTECNOLOGIA

UNIDADE: II
PARTE: A/A
FUNDO AGRÍCOLA: 307846

M:\01-Mapa de safra\Mapas Atualizados\Spot\307846 - Fazenda Esmeralda (Felipe Ferraz)\307846 - Fazenda Esmeralda (Felipe Ferraz).dwg

Bruno Gamboa 12/08/26