
Clealco
Açúcar, Etanol e Energia

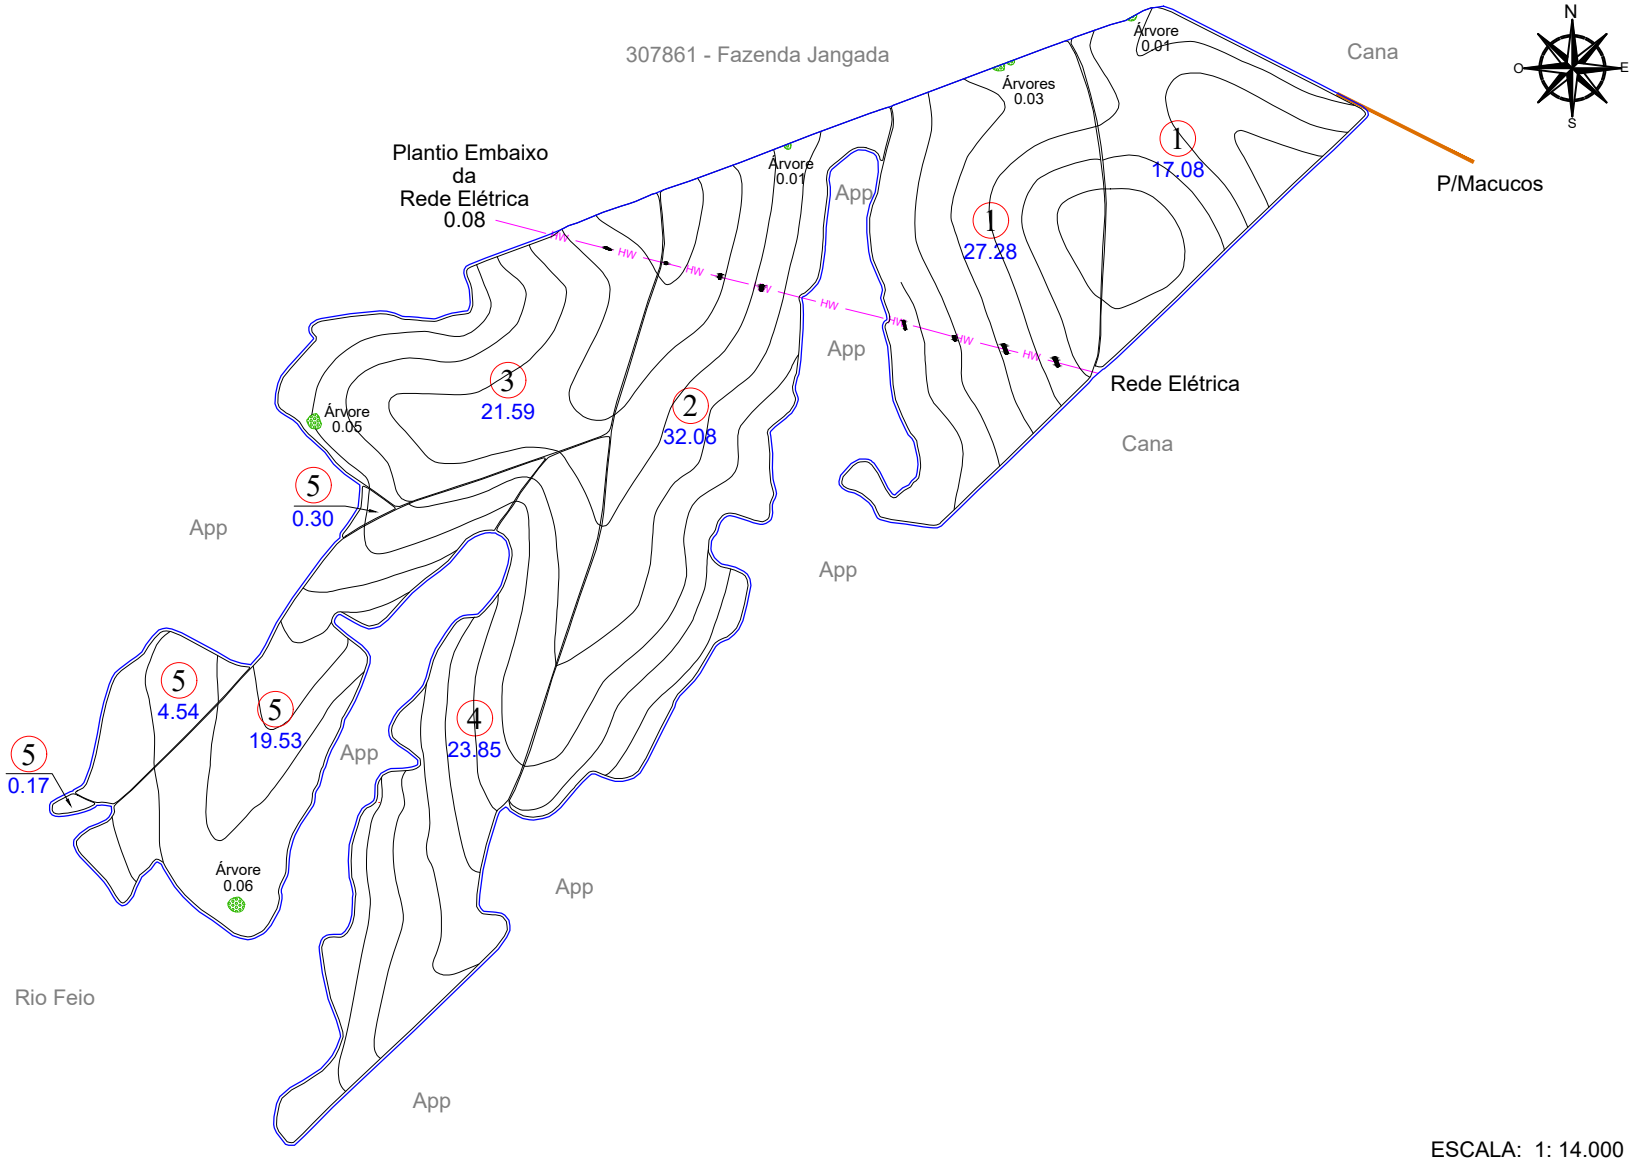

Nº TAL.	DATA PL.	ÁREA (ha)	VARIEDADE
1	05/2025	44.36	DIVERSAS
2	06/2025	32.08	
3		21.59	
4		23.85	
5		24.54	
TOTAL PLANTIO		146.42	

ÁREAS	(ha)	(%)
PLANTIO	146.42	96.06
CARREADORES	5.77	3.79
OUTROS	0.00	0.00
SUB TOTAL AGRICULTÁVEL	152.19	99.84
AP.P.	0.00	0.00
ÁRVORES	0.16	0.10
OUTROS	0.08	0.05
SUB TOTAL NÃO AGRICULT.	0.24	0.16
ÁREA TOTAL	152.43	100.00

C. NÍVEL: 19927.32 m/l 4.58 ha 3.01 %


ESCALA: 1: 14.000

LEGENDA

- FAZENDA
- TALHÃO
- REDE ELÉTRICA
- TERRAÇO BASE LARGA
- TERRAÇO EMBUTIDO

ESPAÇAMENTO: 1.50 x 1.50
TIRO MÉDIO ESTIMADO: 000.00 m
D.V: 0.00 %

CROQUI DE ACESSO

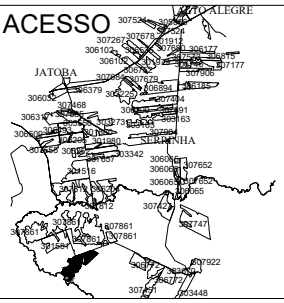

FAZENDA JANGADA

PROPRIETÁRIO: WILLIAN AVILA P. E OUTROS
COMPRADOR: CLEALCO
MUNICÍPIO: GETULINA - SP

DISTÂNCIAS (km):
UNID. I - Asfalto: 68.00 Terra.: 15.70
UNID.I I - Asfalto: 14.60 Terra.: 12.00

COORDENADAS: E(X): 579165.72 N(Y): 7596254.77
LAT: -21°44'7.7476" LONG: -50°14'4.1044"

CLEALCO - AÇÚCAR E ALCOOL S/A - DEPARTAMENTO DE GEOTECNOLOGIA

LEVANTAMENTO VIA:
SATÉLITE
GPS / VANT
GOOGLE

UNIDADE: II
PARTE: A/A
FUNDO AGRÍCOLA: 307856

M:\01-Mapa de safra\Mapas Atualizados\Terceiro\307856 - Fazenda Jangada (Willian Avila Pereira e Outros)\307856 - Fazenda Jangada (Willian Avila Pereira e Outros).dwg

Bruno Gamboa 12/01/26