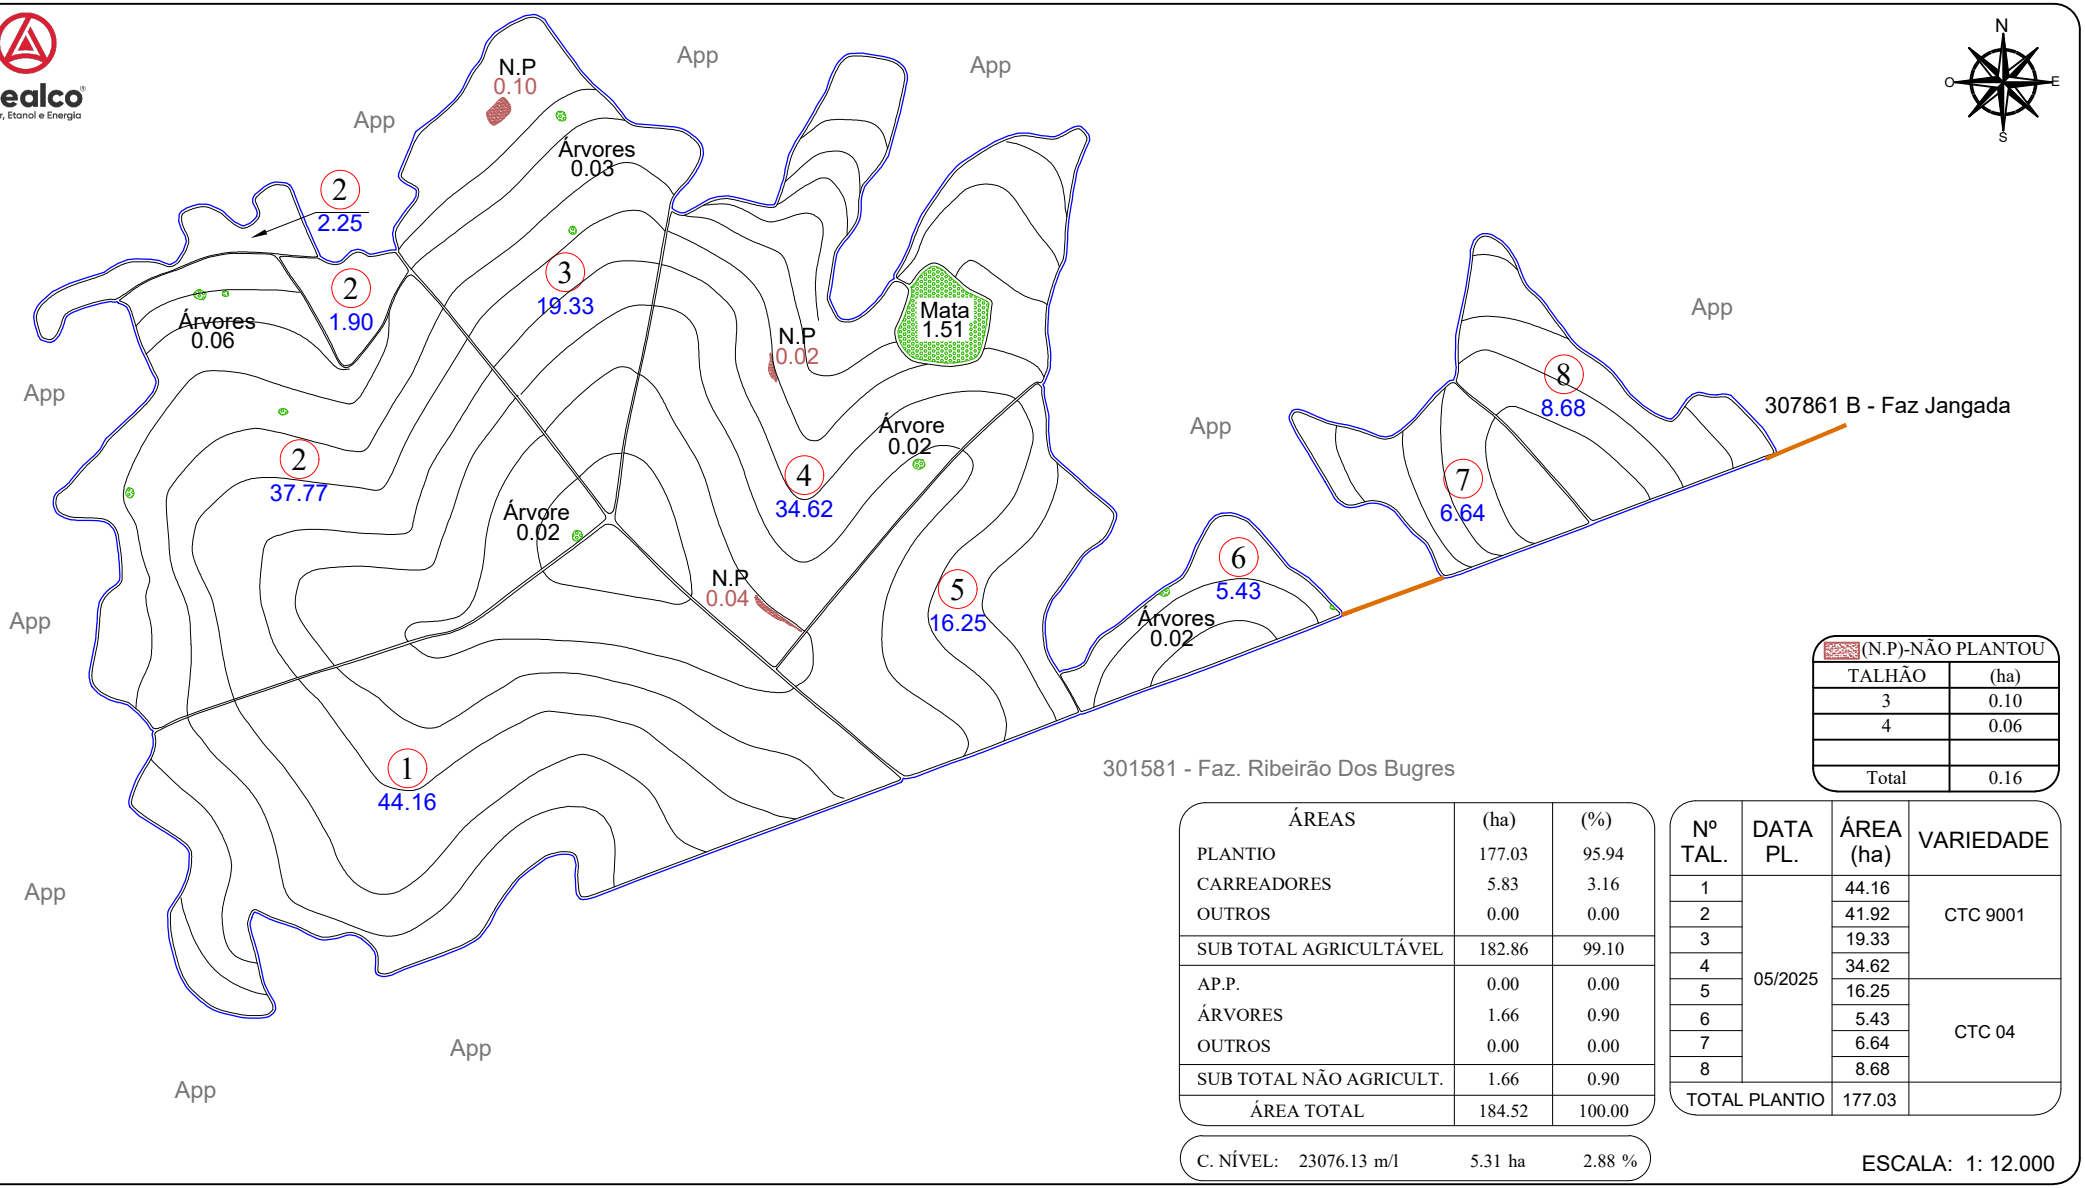


(N.P)-NÃO PLANTOU	
TALHÃO	(ha)
3	0.10
4	0.06
Total	0.16

ÁREAS	(ha)	(%)
PLANTIO	177.03	95.94
CARREADORES	5.83	3.16
OUTROS	0.00	0.00
SUB TOTAL AGRICULTÁVEL	182.86	99.10
AP.P.	0.00	0.00
ÁRVORES	1.66	0.90
OUTROS	0.00	0.00
SUB TOTAL NÃO AGRICULT.	1.66	0.90
ÁREA TOTAL	184.52	100.00

Nº TAL.	DATA PL.	ÁREA (ha)	VARIEDADE
1	05/2025	44.16	CTC 9001
2		41.92	
3		19.33	
4		34.62	
5		16.25	CTC 04
6		5.43	
7		6.64	
8		8.68	
TOTAL PLANTIO		177.03	


C. NÍVEL: 23076.13 m/l 5.31 ha 2.88 %

ESCALA: 1: 12.000

LEGENDA
- FAZENDA
- TALHÃO
- REDE ELÉTRICA
- TERRAÇO BASE LARGA
- TERRAÇO EMBUTIDO

ESPAÇAMENTO: 1.50 x 1.50
TIRO MÉDIO ESTIMADO: 000.00 m
D.V: 5.91%

CROQUI DE ACESSO

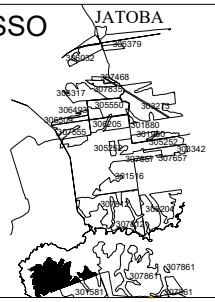

FAZENDA JANGADA

PROPRIETÁRIO: WILLIAN AVILA P. E OUTROS
COMPRADOR: CLEALCO
MUNICÍPIO: GETULINA - SP

DISTÂNCIAS (km):
UNID. I - Asfalto: 68.00 Terra.: 15.70
UNID.I I - Asfalto: 14.60 Terra.: 12.00

COORDENADAS: E(X): 576417.62 N(Y): 7598498.43
LAT: -21°42'55.2119" LONG: -50°15'40.1371"
CLEALCO - AÇÚCAR E ALCOOL S/A - DEPARTAMENTO DE GEOTECNOLOGIA

LEVANTAMENTO VIA:
- SATÉLITE
- GPS / VANT
- GOOGLE

UNIDADE: II
PARTE: A/B
FUNDO AGRÍCOLA: 307861

M:\01-Mapa de safra\Mapas Atualizados\Terceiro\307861 - Fazenda Jangada (Willian Avila Pereira)\307861 A - Fazenda Jangada (Willian Avila Pereira).dwg

Bruno Gamboa 17/12/25