
Clealco
Açúcar, Etanol e Energia

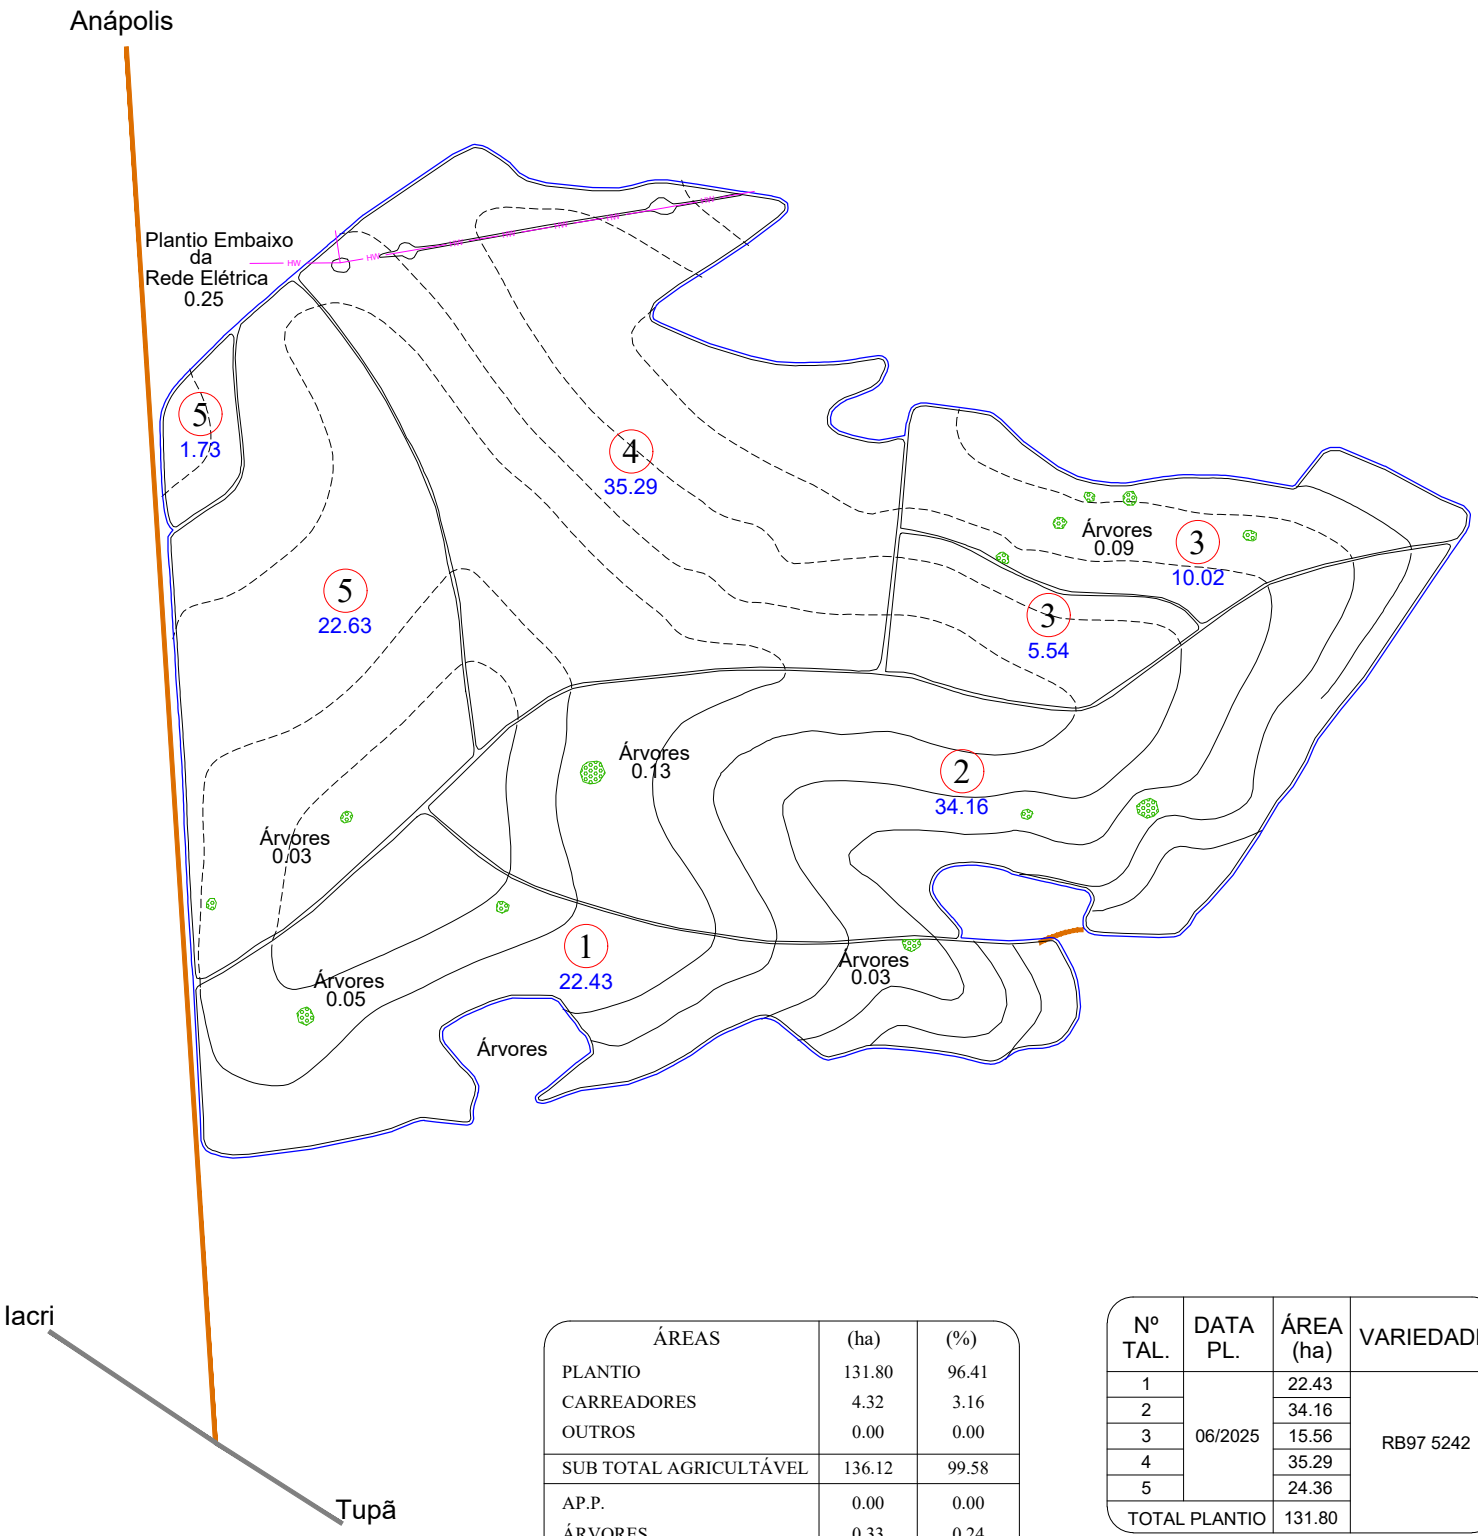

ÁREAS	(ha)	(%)
PLANTIO	131.80	96.41
CARREADORES	4.32	3.16
OUTROS	0.00	0.00
SUB TOTAL AGRICULTÁVEL	136.12	99.58
AP.P.	0.00	0.00
ÁRVORES	0.33	0.24
OUTROS	0.25	0.18
SUB TOTAL NÃO AGRICULT.	0.58	0.42
ÁREA TOTAL	136.70	100.00

C. NÍVEL: 7314.15 m/l 1.68 ha 1.23 %


Nº TAL.	DATA PL.	ÁREA (ha)	VARIEDADE
1	06/2025	22.43	RB97 5242
2		34.16	
3		15.56	
4		35.29	
5		24.36	
TOTAL PLANTIO		131.80	

LEGENDA
- FAZENDA
- TALHÃO
- REDE ELÉTRICA
- TERRAÇO BASE LARGA
- TERRAÇO EMBUTIDO
- (P.O.A) PATIO DE OPERAÇÃO

ESPAÇAMENTO: 1.50 x 1.50
TIRO MÉDIO ESTIMADO: 290.18 m
D.V: 5.62%

ESCALA: 1: 10.000

CROQUI DE ACESSO

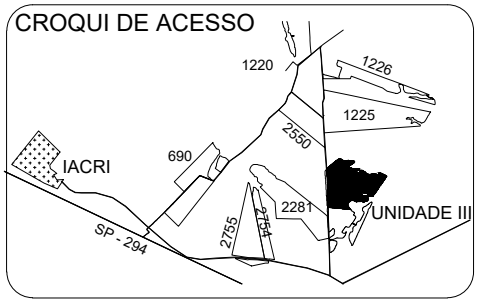

FAZENDA SÃO PAULO

PROPRIETÁRIO: CLAUDEMIR STEFANELI
COMPRADOR: CLEALCO
MUNICÍPIO: TUPÃ - SP

DISTÂNCIAS (km):
UNID. I - Asfalto: 36.50 Terra.: 12.00
UNID.I I - Asfalto: 29.00 Terra.: 25.00

COORDENADAS: E(X): 541094.91 N(Y): 7581584.29
LAT: -21°52'9.5503" LONG: -50°36'8.0626"

CLEALCO - AÇÚCAR E ALCOOL S/A - DEPARTAMENTO DE GEOTECNOLOGIA

LEVANTAMENTO VIA:
- SATÉLITE
- GPS / VANT
- GOOGLE

UNIDADE: II
PARTE: A/A
FUNDO AGRÍCOLA: 307915

M:\01-Mapa de safra\Mapas Atualizados\Terceiro\307915 - Fazenda Sao Paulo (Claudemir Stefaneli)\307915 - Fazenda Sao Paulo (Claudemir Stefaneli).dwg

Bruno Gamboa 04/02/26