
Clealco
Açúcar, Etanol e Energia

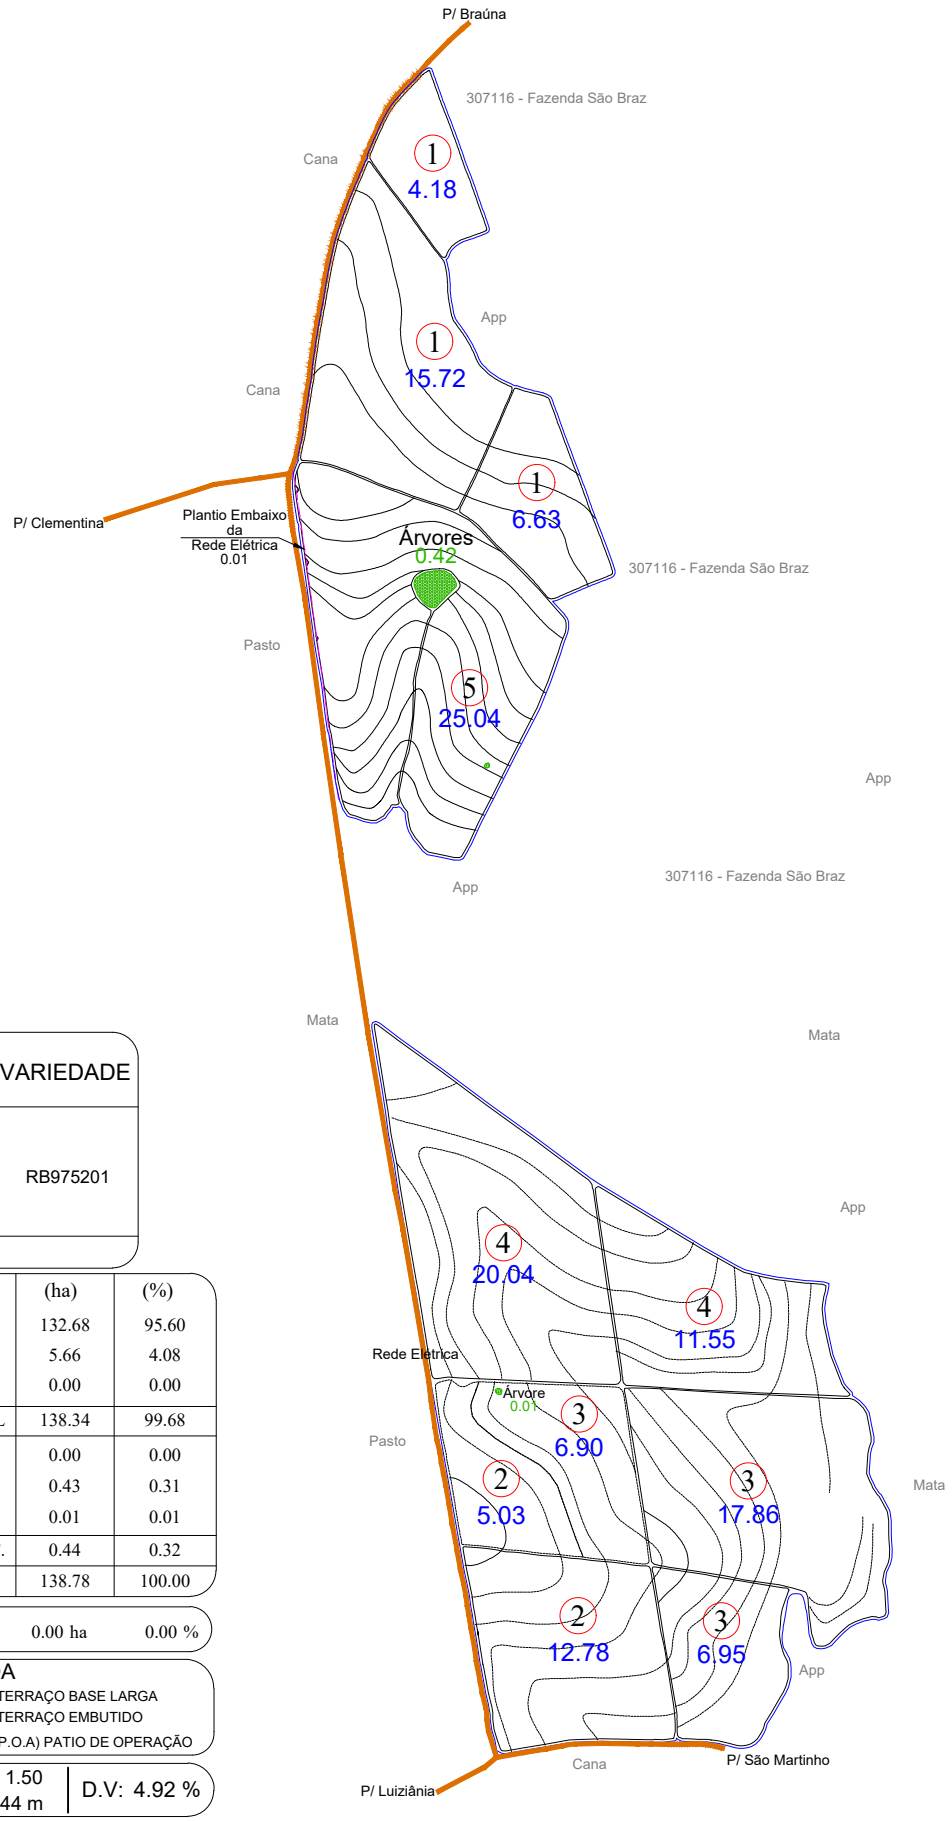

Nº TAL.	DATA PL.	ÁREA (ha)	VARIEDADE
1	03/2024	26.53	RB975201
2		17.81	
3	03/2025	31.71	
4		31.59	
5		25.04	
TOTAL PLANTIO		132.68	

ÁREAS	(ha)	(%)
PLANTIO	132.68	95.60
CARREADORES	5.66	4.08
OUTROS	0.00	0.00
SUB TOTAL AGRICULTÁVEL	138.34	99.68
AP.P.	0.00	0.00
ÁRVORES	0.43	0.31
OUTROS	0.01	0.01
SUB TOTAL NÃO AGRICULT.	0.44	0.32
ÁREA TOTAL	138.78	100.00

C. NÍVEL: 0.00 m/l 0.00 ha 0.00 %


LEGENDA

- FAZENDA
- TALHÃO
- REDE ELÉTRICA
- TERRAÇO BASE LARGA
- TERRAÇO EMBUTIDO
- (P.O.A) PATIO DE OPERAÇÃO

ESPAÇAMENTO: 1.50 x 1.50
TIRO MÉDIO ESTIMADO: 216.44 m
D.V: 4.92 %

ESCALA: 1: 15.000

CROQUI DE ACESSO

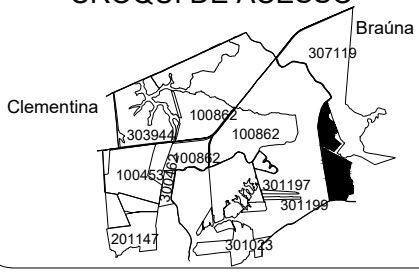

FAZENDA SILVANIA

PROPRIETÁRIO: ALESSANDRO RODRIGO MORETO
COMPRADOR: CLEALCO
MUNICÍPIO: BRAÚNA - SP

DISTÂNCIAS (km):
UNID. I - Asfalto: 18.50 Terra.: 0.00
UNID.I I - Asfalto: 69.50 Terra.: 0.00

COORDENADAS: E(X): 572293.61 N(Y): 7614620.87
LAT: -21°34'11.4778" LONG: -50°18'6.1953"

CLEALCO - AÇÚCAR E ALCOOL S/A - DEPARTAMENTO DE GEOTECNOLOGIA

LEVANTAMENTO VIA:
- SATÉLITE
- GPS / VANT
- GOOGLE

UNIDADE: I
PARTE: A/A
FUNDO AGRÍCOLA: 307943

M:\01-Mapa de safra\Mapas Atualizados\Terceiro\307943 - Fazenda Silvania (Alessandro Rodrigo Moreto)\307943 - Fazenda Silvania (Alessandro Rodrigo Moreto).dwg

BrunoGamboa 13/08/26