Clealco
Açúcar, Etanol e Energia


Nº TAL.	DATA PL.	ÁREA (ha)	VARIEDADE
1	06/2025	6.79	RB975201
2		30.29	
TOTAL PLANTIO		37.08	

ÁREAS	(ha)	(%)
PLANTIO	37.08	92.28
CARREADORES	2.39	5.95
OUTROS	0.00	0.00
SUB TOTAL AGRICULTÁVEL	39.47	98.23
AP.P.	0.00	0.00
ÁRVORES	0.57	1.42
OUTROS	0.14	0.35
SUB TOTAL NÃO AGRICULT.	0.71	1.77
ÁREA TOTAL	40.18	100.00

C. NÍVEL: 4558.82 m/l 1.05 ha 2.61 %


LEGENDA
- FAZENDA
- TALHÃO
- REDE ELÉTRICA
- TERRAÇO BASE LARGA
- TERRAÇO EMBUTIDO
- (P.O.A) PATIO DE OPERAÇÃO

ESPAÇAMENTO: 1.50 x 1.50
TIRO MÉDIO ESTIMADO: 171.40 m
D.V: 5.56 %

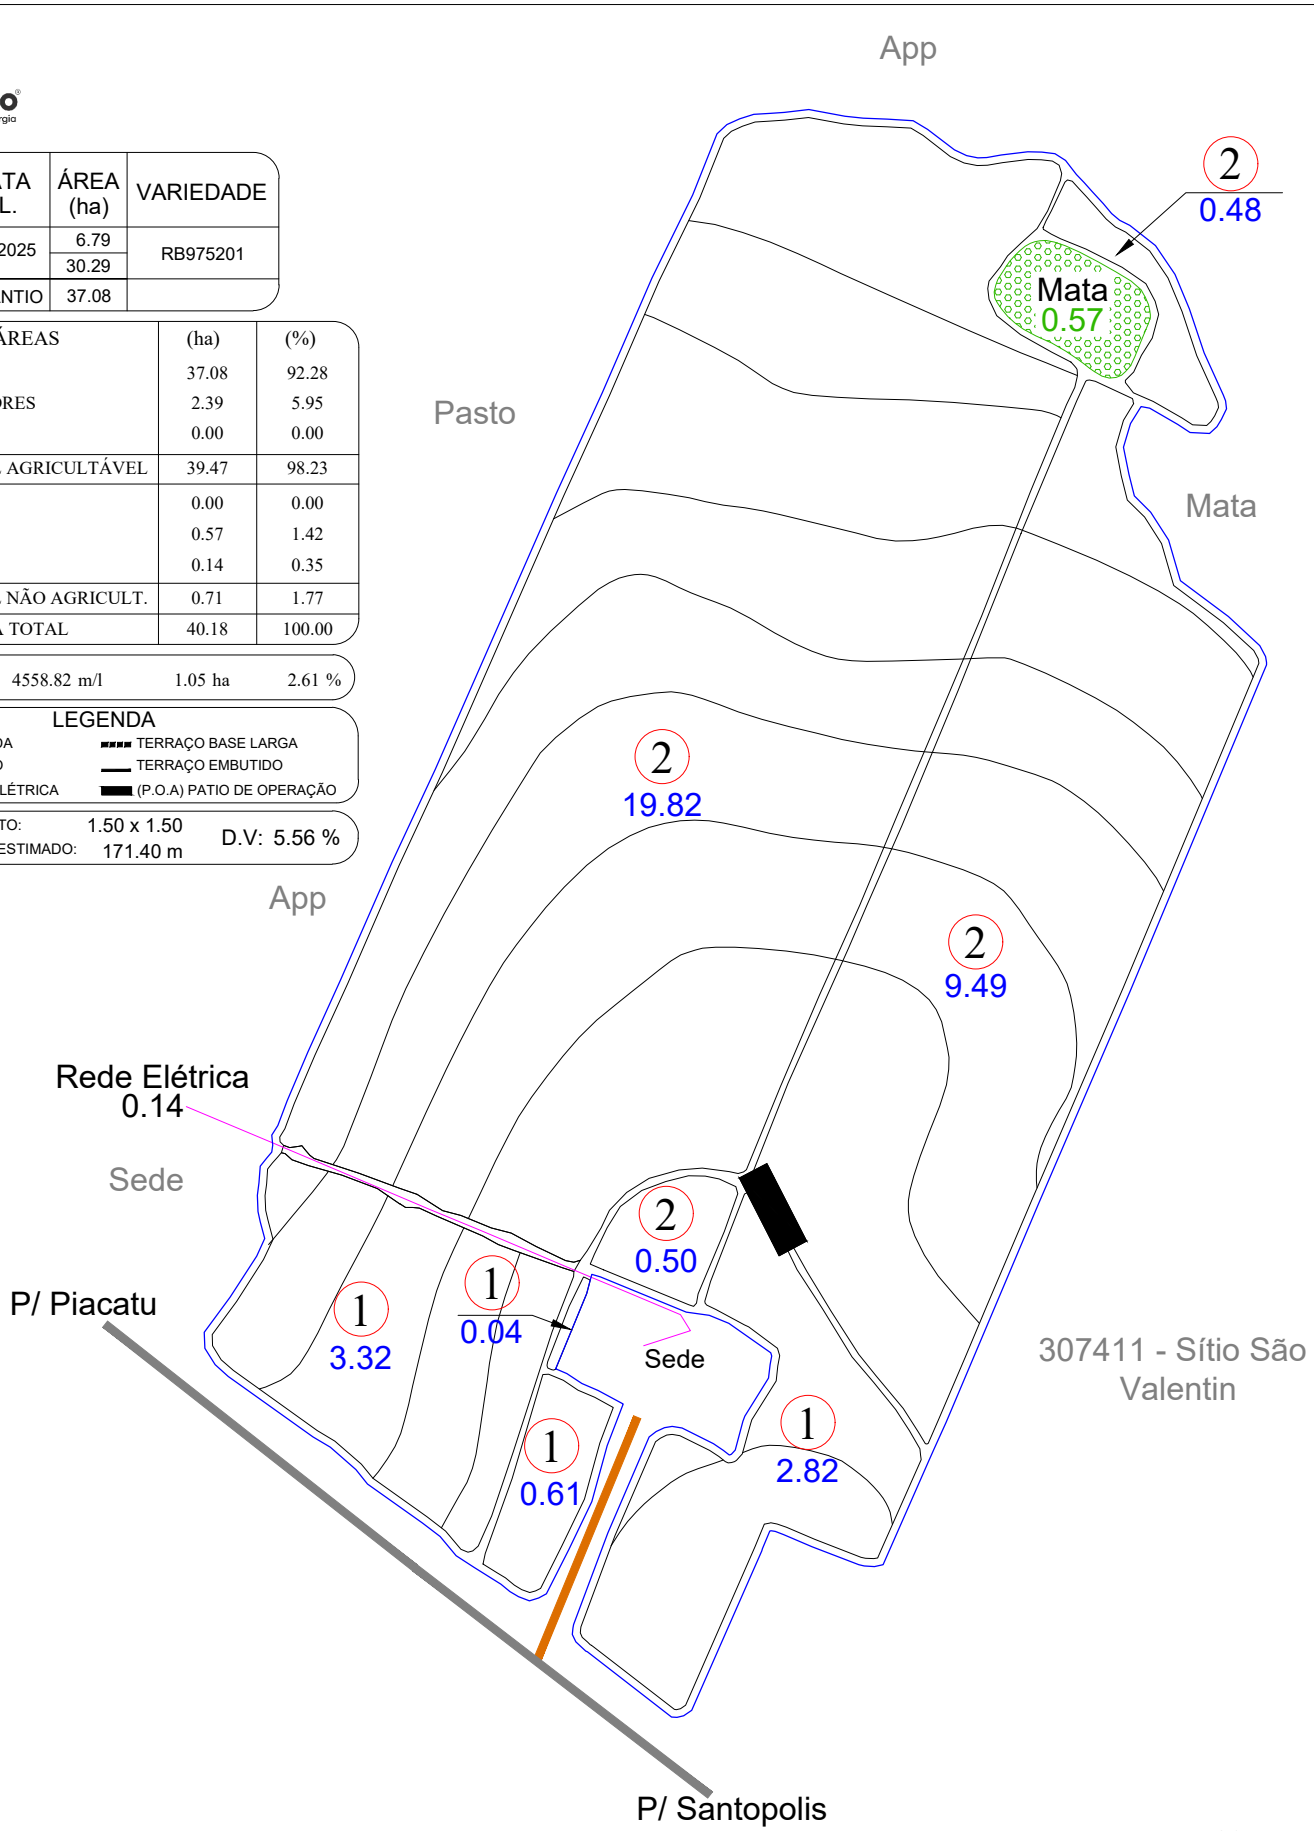

ESCALA: 1: 5.000

CROQUI DE ACESSO

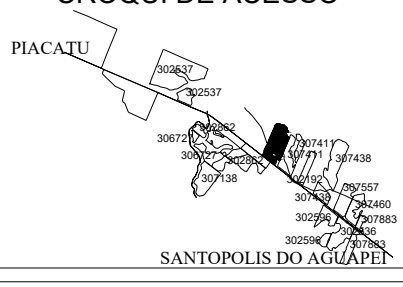

SÍTIO SANTA GENI

PROPRIETÁRIO: HAROLDO ALVES PIO
COMPRADOR: CLEALCO
MUNICÍPIO: SANTÓPOLIS - SP

DISTÂNCIAS (km):
UNID. I - Asfalto: 17.00 Terra.: 1.00
UNID.I I - Asfalto: 53.00 Terra.: 1.00

COORDENADAS: E(X): 547726.92 N(Y): 7609306.66
LAT: -21°37'7.2943" LONG: -50°32'19.8582"

CLEALCO - AÇÚCAR E ALCOOL S/A - DEPARTAMENTO DE GEOTECNOLOGIA

UNIDADE: I
PARTE: A/A
FUNDO AGRÍCOLA: 307952

M:\01-Mapa de safra\Mapas Atualizados\Terceiro\307952 - Sítio Santa Geni (Haroldo Alves Pio)\307952 - Sítio Santa Geni (Haroldo Alves Pio).dwg

Bruno Gamboa 10/12/25