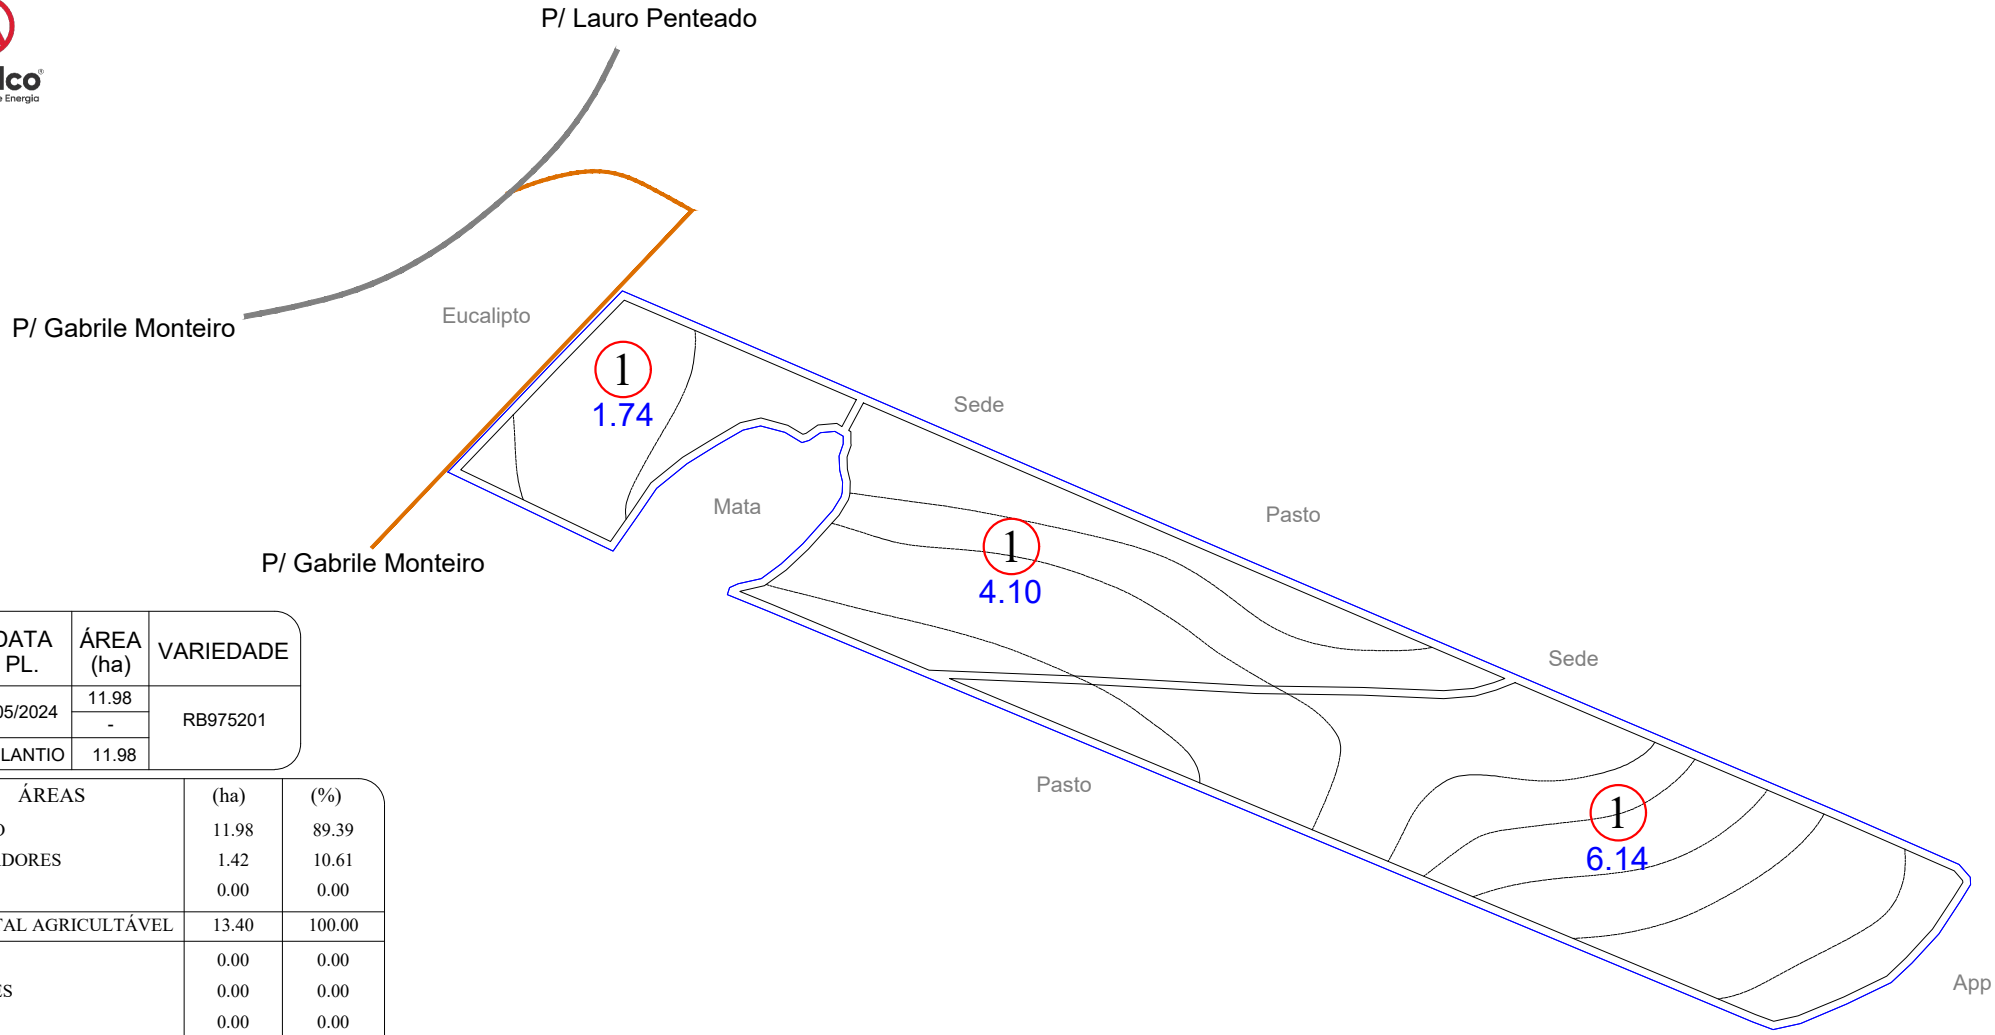


Nº TAL.	DATA PL.	ÁREA (ha)	VARIEDADE
1	05/2024	11.98	RB975201
-		-	
TOTAL PLANTIO		11.98	

ÁREAS	(ha)	(%)
PLANTIO	11.98	89.39
CARREADORES	1.42	10.61
OUTROS	0.00	0.00
SUB TOTAL AGRICULTÁVEL	13.40	100.00
AP.P.	0.00	0.00
ÁRVORES	0.00	0.00
OUTROS	0.00	0.00
SUB TOTAL NÃO AGRICULT.	0.00	0.00
ÁREA TOTAL	13.40	100.00

C. NÍVEL: 0.00 m/l 0.00 ha 0.00 %


ESCALA: 1: 5.000

LEGENDA

- FAZENDA
- TALHÃO
- REDE ELÉTRICA
- TERRAÇO BASE LARGA
- TERRAÇO EMBUTIDO

ESPAÇAMENTO: 1.50 x 1.50
TIRO MÉDIO ESTIMADO: 134.59 m
D.V: 6.09 %

CROQUI DE ACESSO

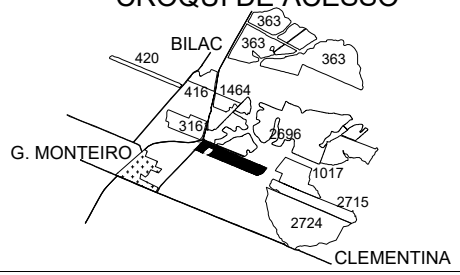

ESTÂNCIA PAIQUERE I

PROPRIETÁRIO: RAFAEL ZANDONA
COMPRADOR: CLEALCO
MUNICÍPIO: GABRIEL MONTEIRO - SP

DISTÂNCIAS (km):
UNID. I - Asfalto: 30.00 Terra.: 1.00
UNID.I I - Asfalto: 63.30 Terra.: 7.70

COORDENADAS: E(X): 548225.78 N(Y): 7619561.98
LAT: -21°31'33.6911" LONG: -50°32'3.5724"

CLEALCO - AÇÚCAR E ALCOOL S/A - DEPARTAMENTO DE GEOTECNOLOGIA

UNIDADE: I
PARTE: A/A
FUNDO AGRÍCOLA: 307971

M:\01-Mapa de safra\Mapas Atualizados\Terceiro\307971 - Estancia Paiquere I (Rafael Zandona)\307971 - Estancia Paiquere I (Rafael Zandona).dwg

Peterson Santos 23/07/2025