
Clealco
Açúcar, Etanol e Energia

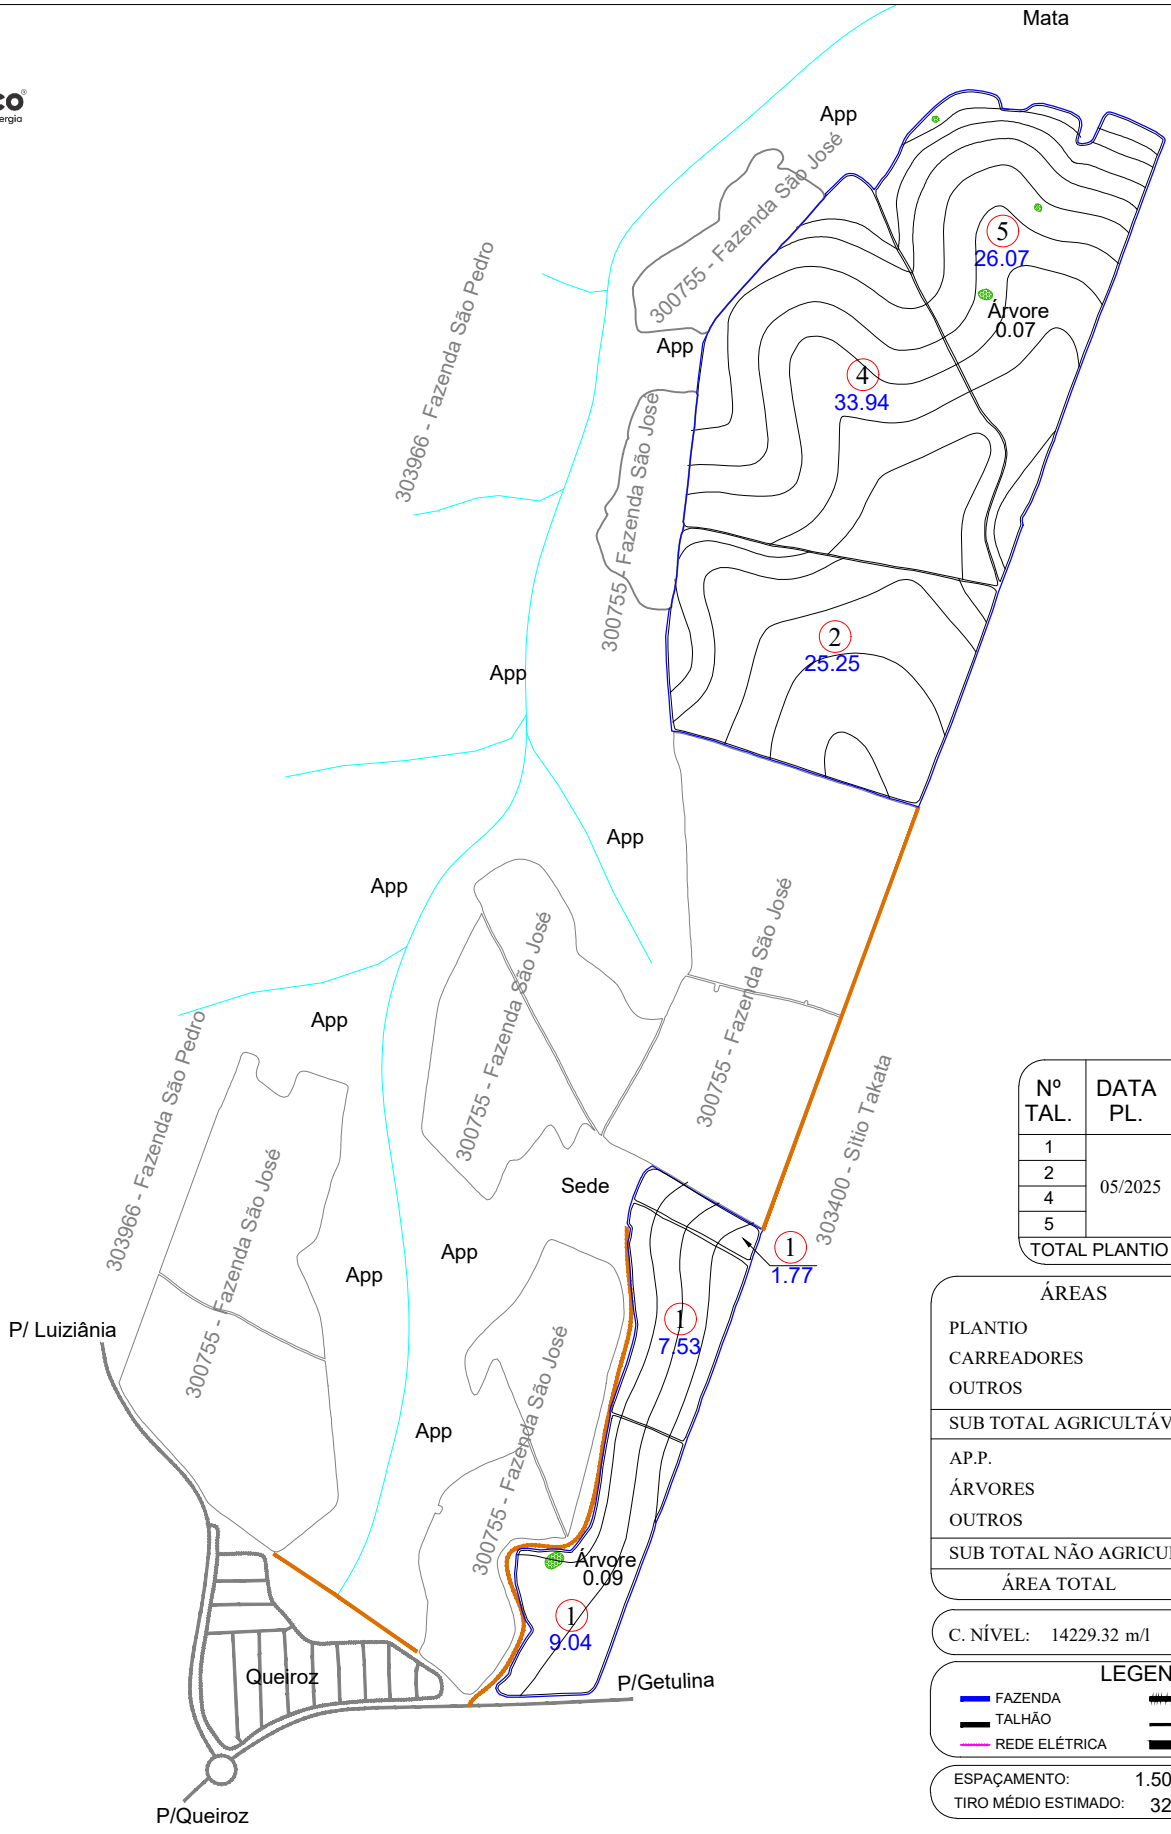

Nº TAL.	DATA PL.	ÁREA (ha)	VARIEDADE
1	05/2025	18.34	RB 975242
2		25.25	CV 7870
4		33.94	CTC 04
5		26.07	
TOTAL PLANTIO		103.60	

ÁREAS	(ha)	(%)
PLANTIO	103.60	96.93
CARREADORES	3.12	2.92
OUTROS	0.00	0.00
SUB TOTAL AGRICULTÁVEL	106.72	99.85
AP.P.	0.00	0.00
ÁRVORES	0.16	0.15
OUTROS	0.00	0.00
SUB TOTAL NÃO AGRICULT.	0.16	0.15
ÁREA TOTAL	106.88	100.00

C. NÍVEL: 14229.32 m/l 3.27 ha 3.06 %


LEGENDA

- FAZENDA
- TALHÃO
- REDE ELÉTRICA
- TERRAÇO BASE LARGA
- TERRAÇO EMBUTIDO
- (P.O.A) PATIO DE OPERAÇÃO

ESPAÇAMENTO: 1.50 x 1.50
TIRO MÉDIO ESTIMADO: 326.33 m
D.V: 4.89%

ESCALA: 1: 15.500

CROQUI DE ACESSO

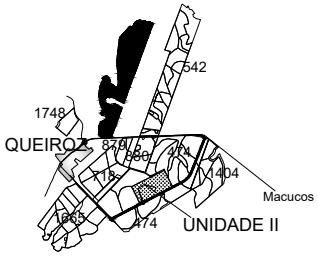

FAZENDA SÃO JOSÉ

PROPRIETÁRIO: CLAUDIO MEDEIROS GRISOLIA
COMPRADOR: CLEALCO
MUNICÍPIO: QUEIROZ - SP

DISTÂNCIAS (km):
UNID. I - Asfalto: 51.00 Terra.: 6.00
UNID.I I - Asfalto: 5.60 Terra.: 1.00

COORDENADAS: E(X): 578971.44 N(Y): 7590600.92
LAT: -21°47'11.6561" LONG: -50°14'9.8943"

CLEALCO - AÇÚCAR E ALCOOL S/A - DEPARTAMENTO DE GEOTECNOLOGIA

SATÉLITE
GPS / VANT
GOOGLE

UNIDADE: II
PARTE: A/A
FUNDO AGRÍCOLA: 308007

M:\01-Mapa de safra\Mapas Atualizados\Terceiro\308007 - Fazenda São Jose (Cláudio Medeiros Grisolia)\308007 - Fazenda São Jose (Cláudio Medeiros Grisolia).dwg

Bruno Gamboa 30/01/26