
Clealco
Açúcar, Etanol e Energia

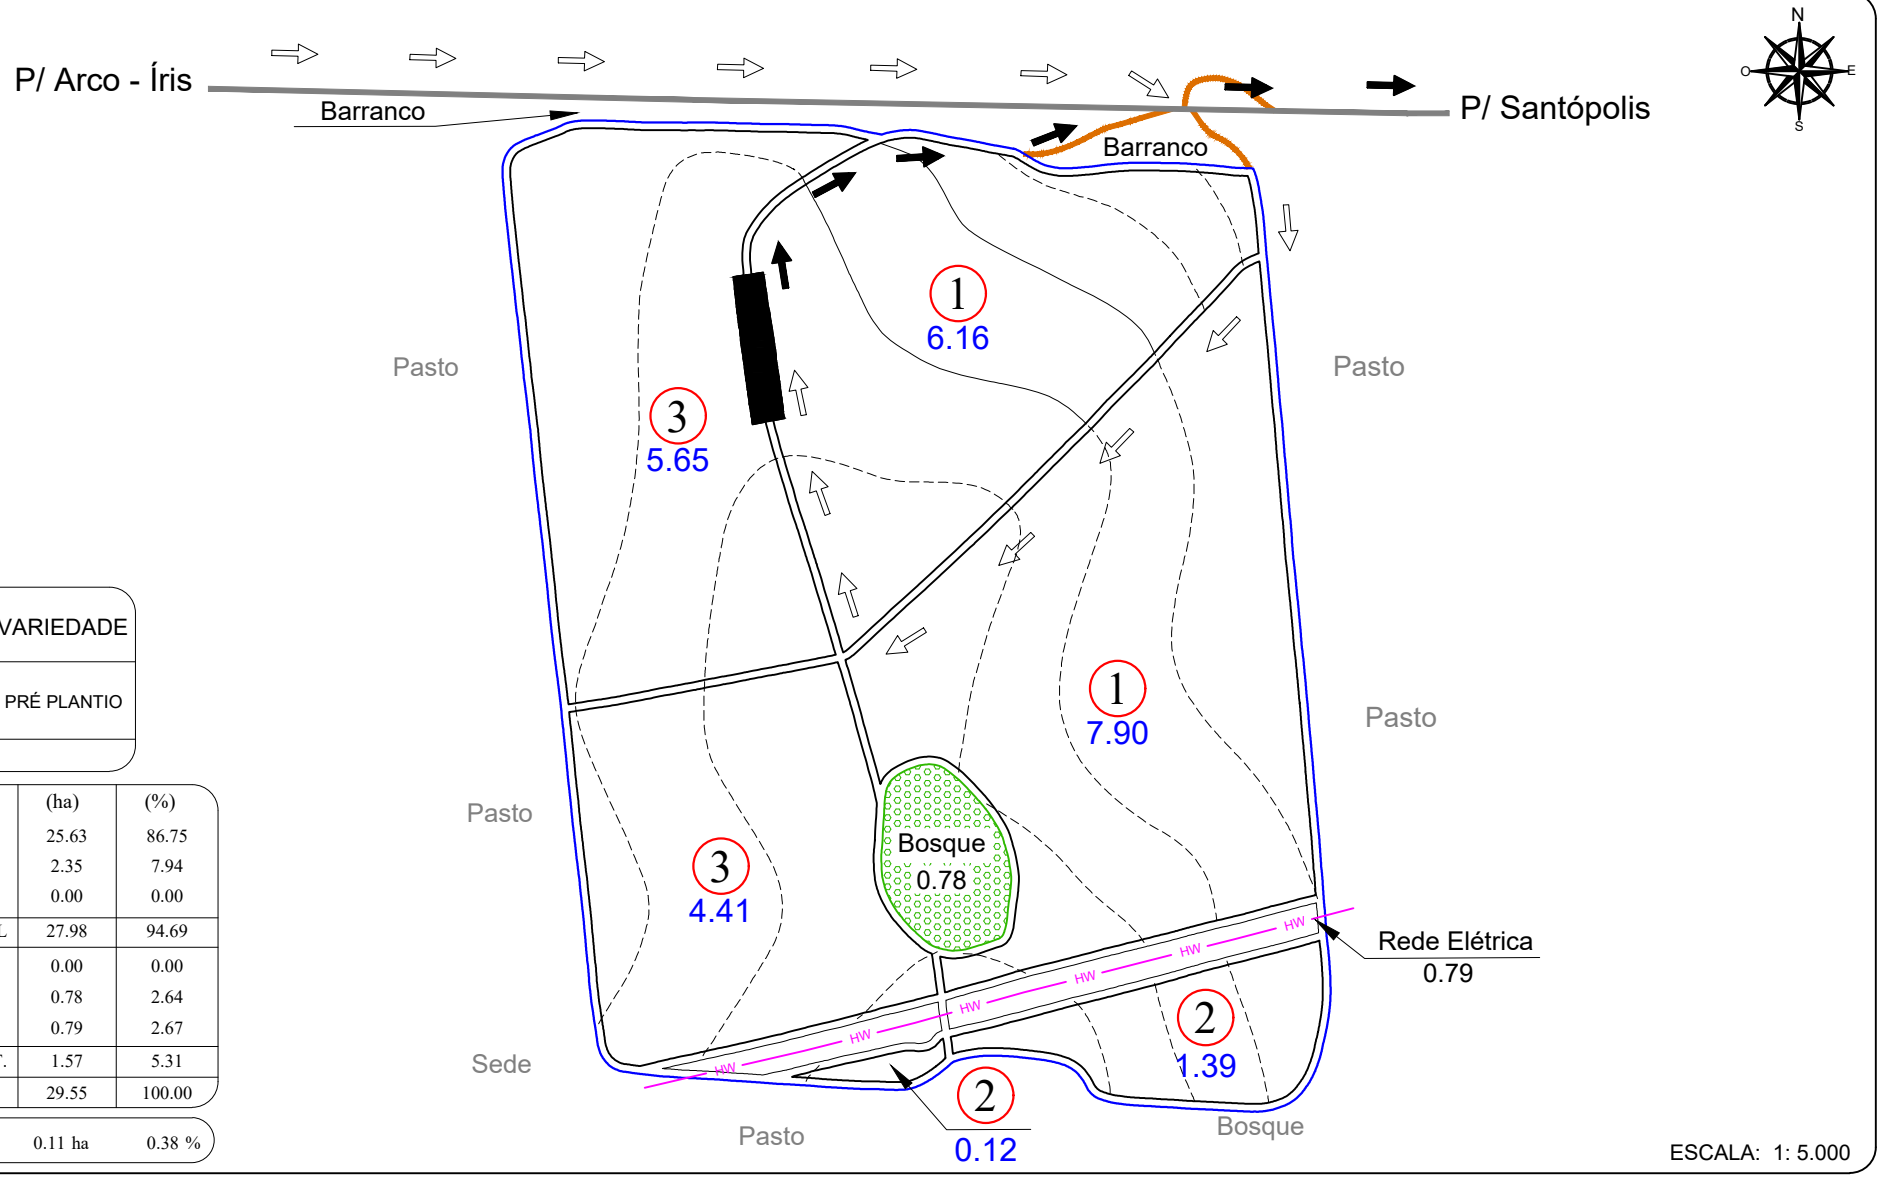

Nº TAL.	DATA PL.	ÁREA (ha)	VARIEDADE
1	2026	14.06	PRÉ PLANTIO
2		1.51	
3		10.06	
TOTAL PLANTIO		25.63	

ÁREAS	(ha)	(%)
PLANTIO	25.63	86.75
CARREADORES	2.35	7.94
OUTROS	0.00	0.00
SUB TOTAL AGRICULTÁVEL	27.98	94.69
AP.P.	0.00	0.00
ÁRVORES	0.78	2.64
OUTROS	0.79	2.67
SUB TOTAL NÃO AGRICULT.	1.57	5.31
ÁREA TOTAL	29.55	100.00


C. NÍVEL: 489.84 m/l 0.11 ha 0.38 %

ESCALA: 1: 5.000

LEGENDA
- FAZENDA
- TALHÃO
- REDE ELÉTRICA
- TERRAÇO BASE LARGA
- TERRAÇO EMBUTIDO
- VAZIO
- CARREGADO

ESPAÇAMENTO: 1.50 x 1.50
TIRO MÉDIO ESTIMADO: 193.92 m
D.V: 5.60 %

CROQUI DE ACESSO

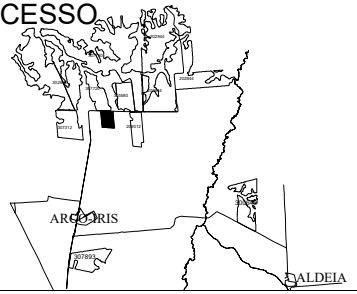

SÍTIO YUNOMAE

PROPRIETÁRIO: CLEBER AMARAL HUNGARO
COMPRADOR: CLEALCO
MUNICÍPIO: ARCO ÍRIS - SP

DISTÂNCIAS (km):
UNID. I - Asfalto: 25.70 Terra.: 0.00
UNID.I I - Asfalto: 47.00 Terra.: 0.00

COORDENADAS: E(X): 556313.02 N(Y): 7596023.52
LAT: -21°44'18.4157" LONG: -50°27'19.5852"
CLEALCO - AÇÚCAR E ALCOOL S/A - DEPARTAMENTO DE GEOTECNOLOGIA

LEVANTAMENTO VIA:
SATÉLITE
GPS / VANT
GOOGLE

UNIDADE: II
PARTE: A/A
FUNDO AGRÍCOLA: 308012

M:\01-Mapa de safra\Mapas Atualizados\Terceiro\308012 - Sítio Yunomae (Cleber Amaral Hungaro)\308012 - Sítio Yunomae (Cleber Amaral Hungaro).dwg

Peterson Santos 13/11/2025