
Clealco
Açúcar, Etanol e Energia

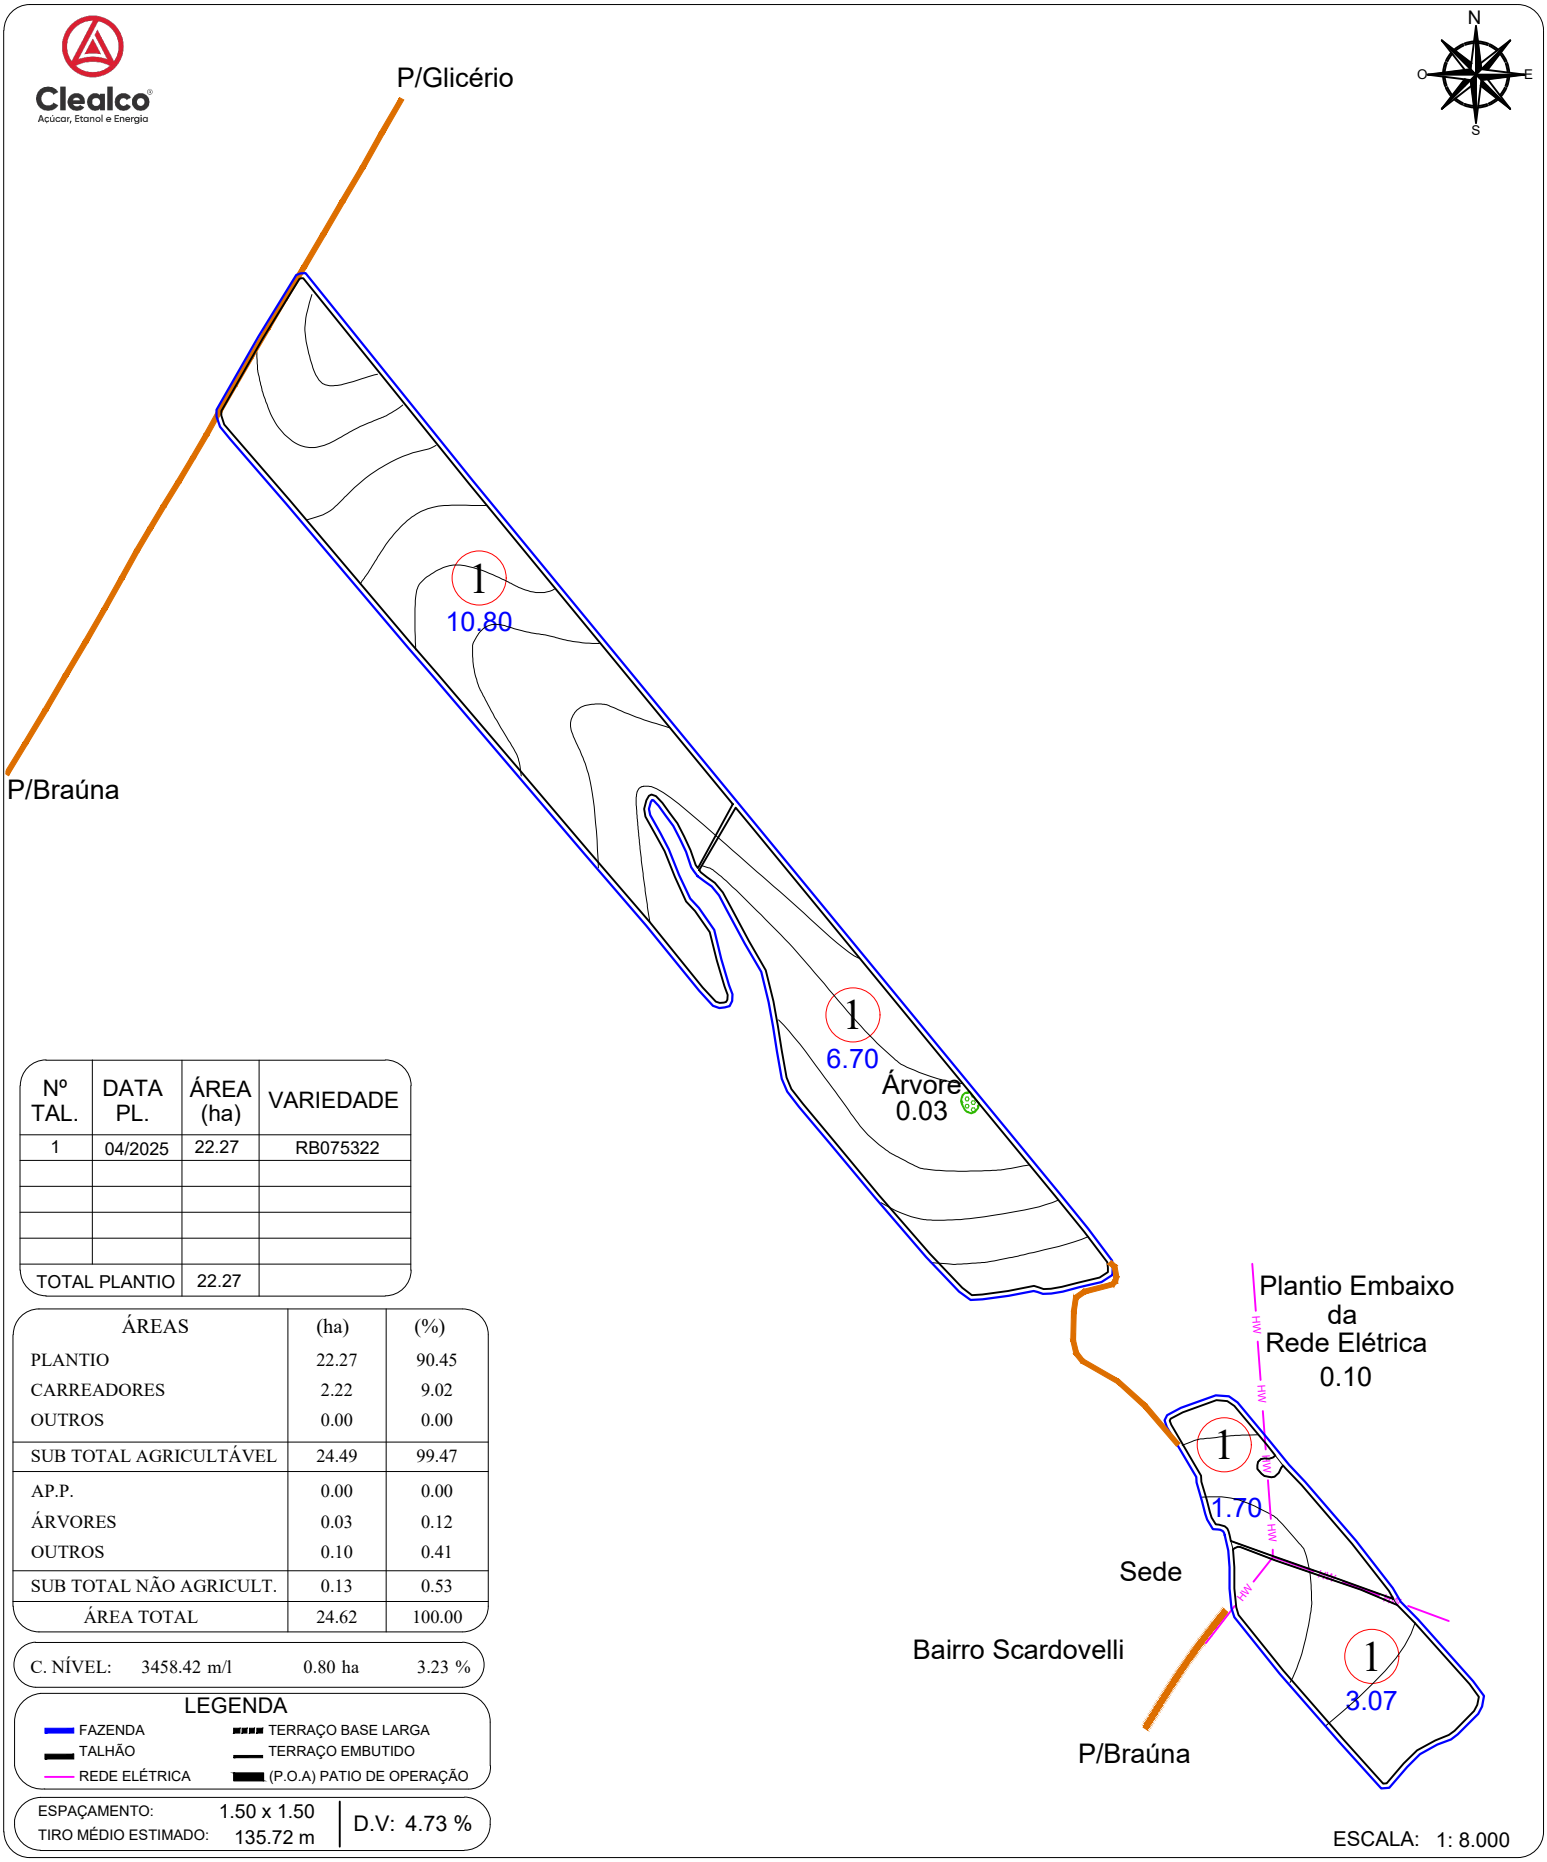

Nº TAL.	DATA PL.	ÁREA (ha)	VARIEDADE
1	04/2025	22.27	RB075322
TOTAL PLANTIO		22.27	

ÁREAS	(ha)	(%)
PLANTIO	22.27	90.45
CARREADORES	2.22	9.02
OUTROS	0.00	0.00
SUB TOTAL AGRICULTÁVEL	24.49	99.47
AP.P.	0.00	0.00
ÁRVORES	0.03	0.12
OUTROS	0.10	0.41
SUB TOTAL NÃO AGRICULT.	0.13	0.53
ÁREA TOTAL	24.62	100.00

C. NÍVEL: 3458.42 m/l 0.80 ha 3.23 %


LEGENDA

- FAZENDA
- TALHÃO
- REDE ELÉTRICA
- TERRAÇO BASE LARGA
- TERRAÇO EMBUTIDO
- (P.O.A) PATIO DE OPERAÇÃO

ESPAÇAMENTO: 1.50 x 1.50
TIRO MÉDIO ESTIMADO: 135.72 m
D.V: 4.73 %

ESCALA: 1: 8.000

CROQUI DE ACESSO

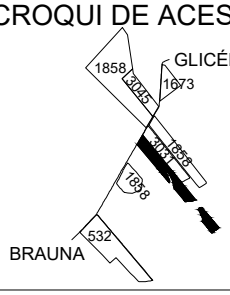

SÍTIO BOA VISTA I

PROPRIETÁRIO: BRUNO MAROLATO DANILUCCI
COMPRADOR: CLEALCO
MUNICÍPIO: GLICÉRIO - SP

DISTÂNCIAS (km):
UNID. I - Asfalto: 18.50 Terra.: 4.57
UNID.I I - Asfalto: 76.50 Terra.: 4.57

COORDENADAS: E(X): 577966.83 N(Y): 7624856.50
LAT: -21°28'37.7202" LONG: -50°14'50.6529"
CLEALCO - AÇÚCAR E ALCOOL S/A - DEPARTAMENTO DE GEOTECNOLOGIA

SATÉLITE
GPS / VANT
GOOGLE

UNIDADE: I
PARTE: A/A
FUNDO AGRÍCOLA: 308025

M:\01-Mapa de safra\Mapas Atualizados\Terceiro\308025 - Sitio Boa Vista I (Bruno Marolato Danilucci)\308025 - Sitio Boa Vista I (Bruno Marolato Danilucci).dwg

Bruno Gamboa 30/01/26