
Clealco
Açúcar, Etanol e Energia

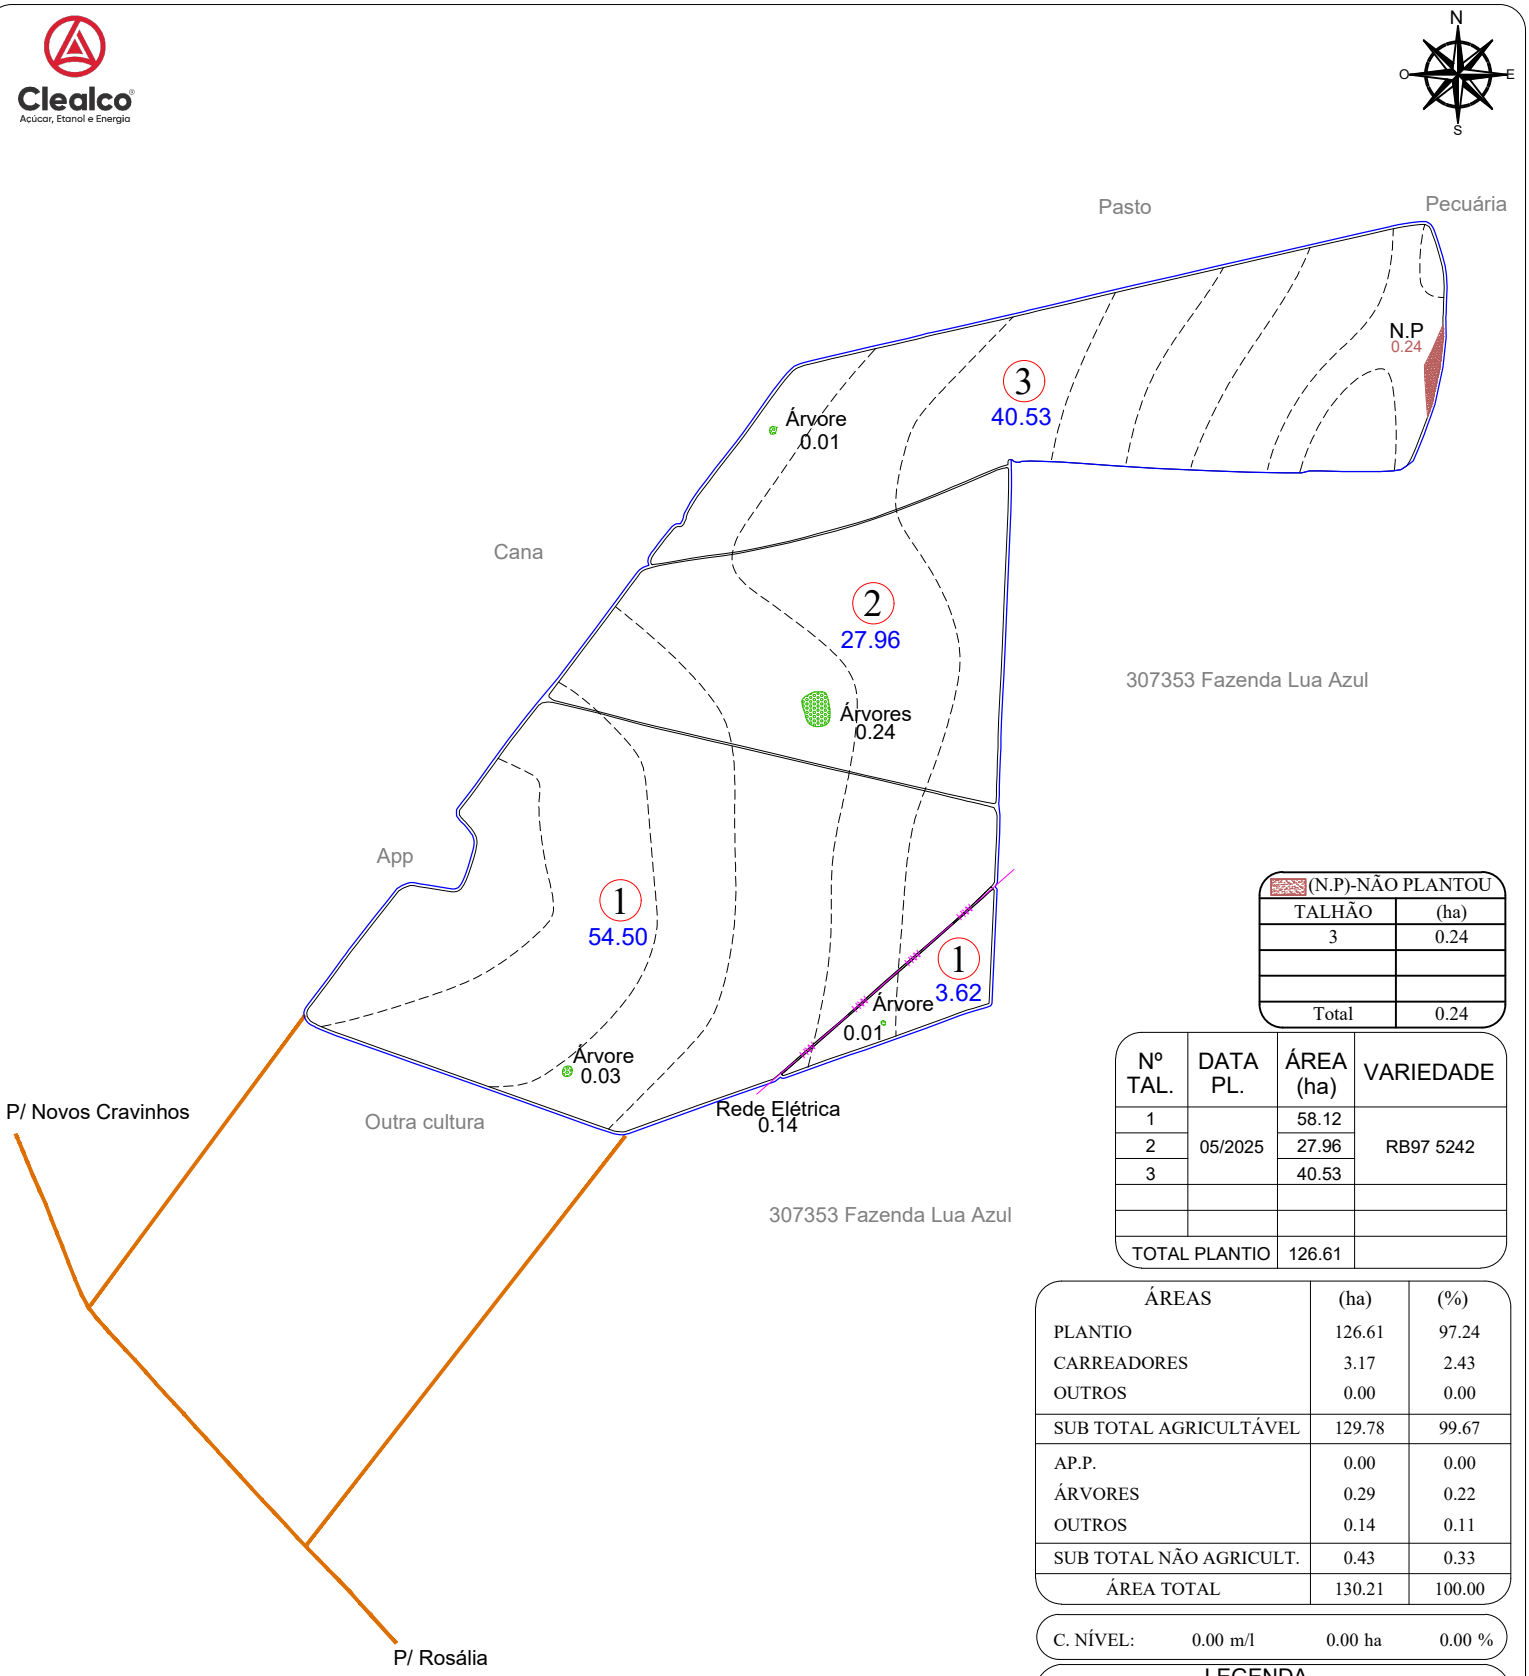

(N.P)-NÃO PLANTOU	
TALHÃO	(ha)
3	0.24
Total	0.24

Nº TAL.	DATA PL.	ÁREA (ha)	VARIEDADE
1	05/2025	58.12	RB97 5242
2		27.96	
3		40.53	
TOTAL PLANTIO		126.61	

ÁREAS	(ha)	(%)
PLANTIO	126.61	97.24
CARREADORES	3.17	2.43
OUTROS	0.00	0.00
SUB TOTAL AGRICULTÁVEL	129.78	99.67
AP.P.	0.00	0.00
ÁRVORES	0.29	0.22
OUTROS	0.14	0.11
SUB TOTAL NÃO AGRICULT.	0.43	0.33
ÁREA TOTAL	130.21	100.00

C. NÍVEL:	0.00 m/l	0.00 ha	0.00 %


LEGENDA

- FAZENDA
- TALHÃO
- REDE ELÉTRICA
- TERRAÇO BASE LARGA
- TERRAÇO EMBUTIDO
- (P.O.A) PATIO DE OPERAÇÃO

ESPAÇAMENTO:	1.50 x 1.50	D.V: 3.69 %
TIRO MÉDIO ESTIMADO:	443.87	

ESCALA: 1: 13.500

CROQUI DE ACESSO

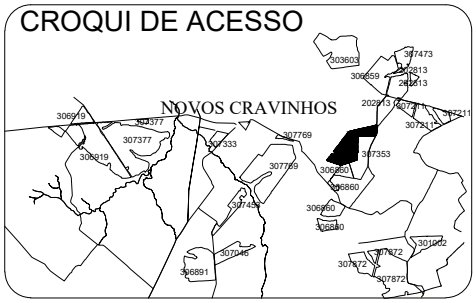

FAZENDA CHAPADÃO

PROPRIETÁRIO: NIVALDO PICINELLI
COMPRADOR: CLEALCO
MUNICÍPIO: POMPEIA - SP

DISTÂNCIAS (km):
UNID. I - Asfalto: 84.00 Terra.: 14.00
UNID.I I - Asfalto: 22.00 Terra.: 14.00

COORDENADAS: E(X): 596004.53 N(Y): 7567559.29
LAT: -21°59'37.9460" LONG: -50°4'11.9313"

CLEALCO - AÇÚCAR E ALCOOL S/A - DEPARTAMENTO DE GEOTECNOLOGIA

LEVANTAMENTO VIA:
- SATÉLITE
- GPS / VANT
- GOOGLE

UNIDADE: II
PARTE: A/A
FUNDO AGRÍCOLA: 308044

M:\01-Mapa de safra\Mapas Atualizados\Terceiro\308044 - Fazenda Chapadão (Nilvaldo Picinelli)\308044 - Fazenda Chapadão (Nilvaldo Picinelli).dwg

Bruno Gamboa 08/01/26