
Clealco
Açúcar, Etanol e Energia

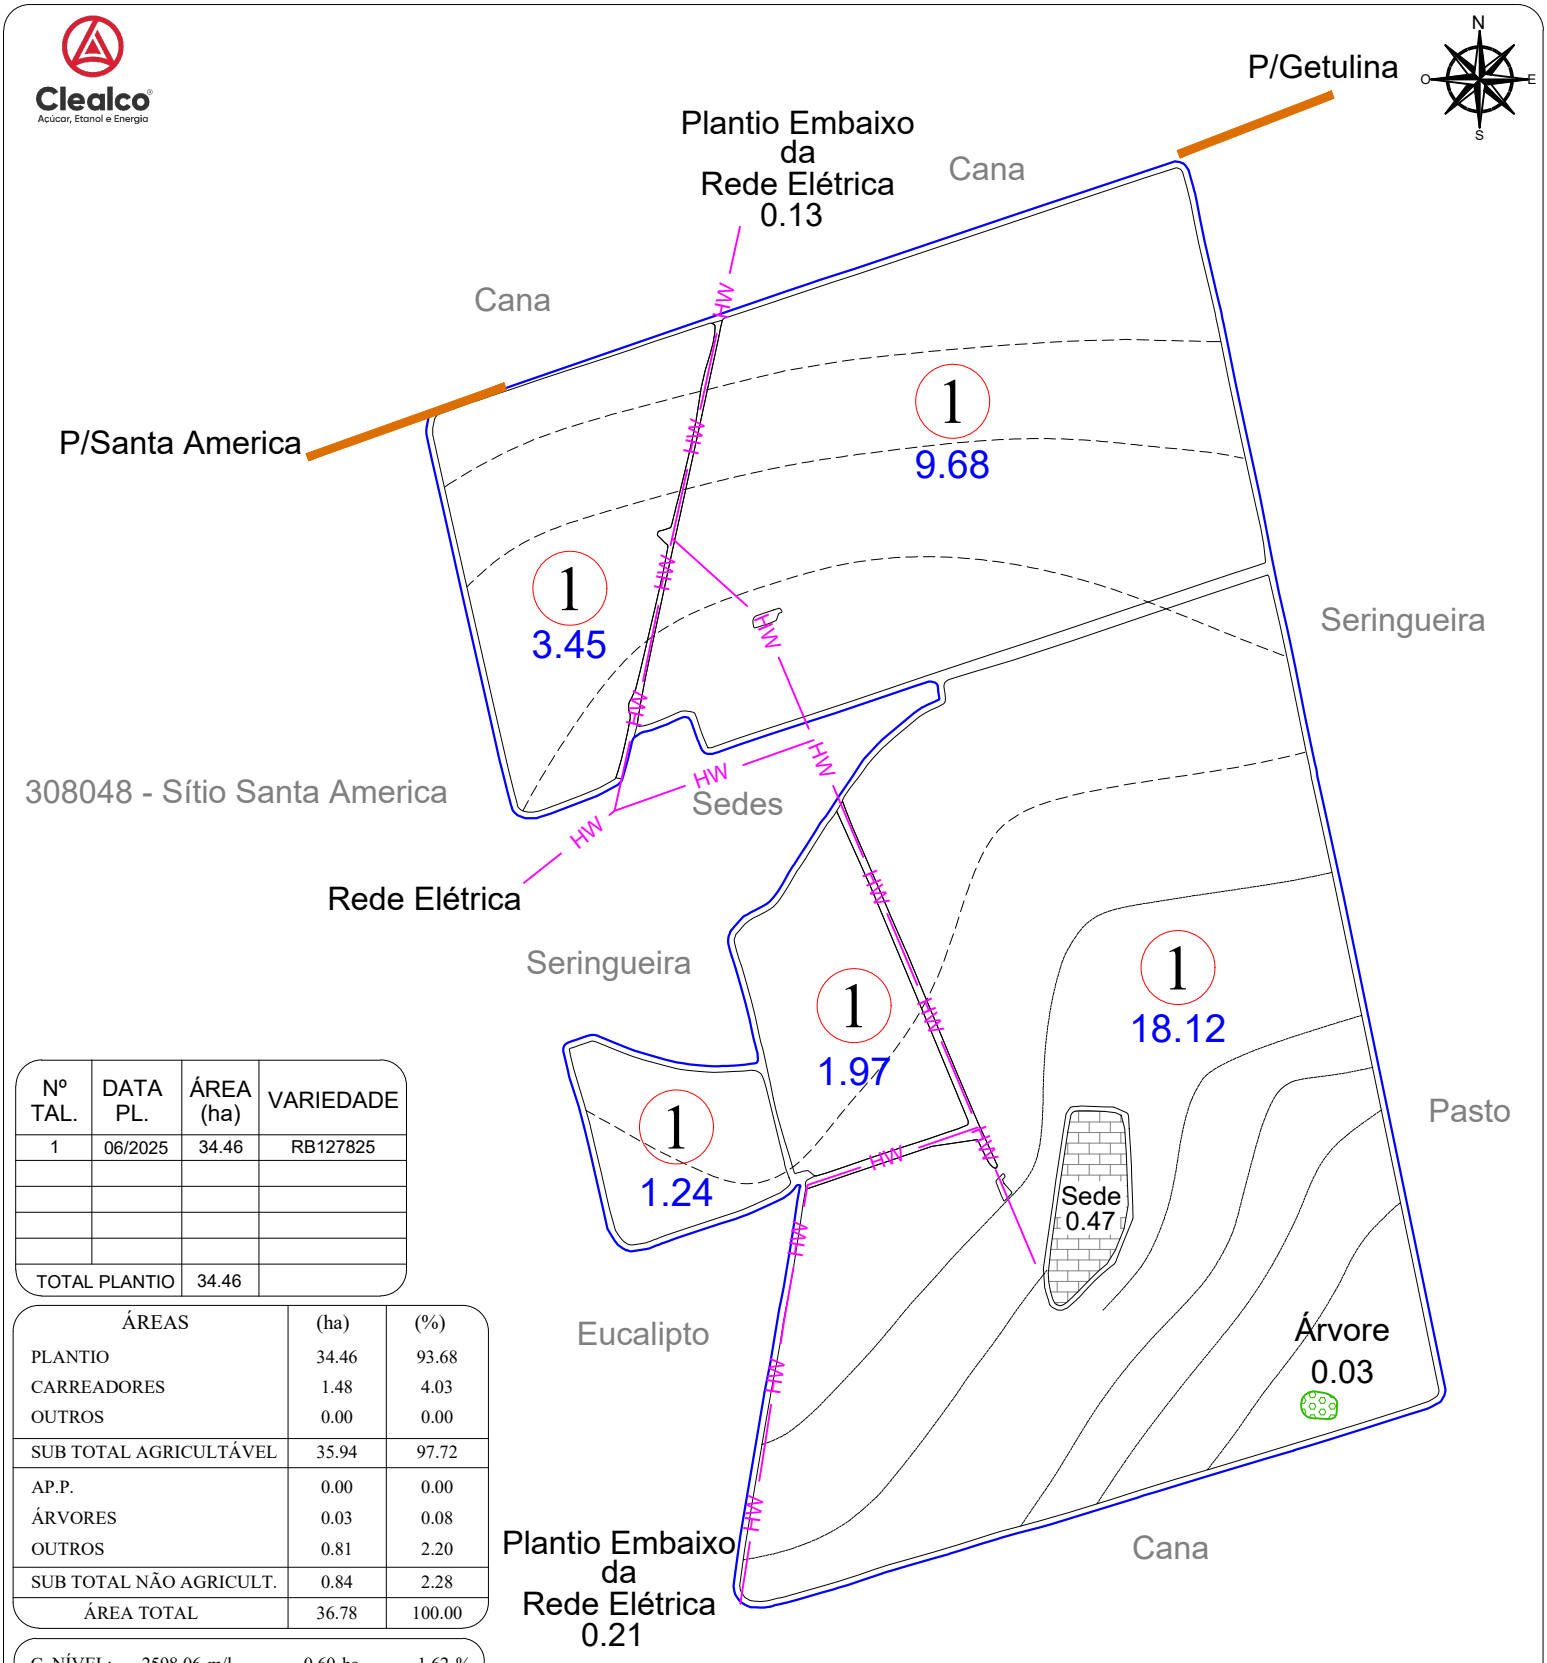

Nº TAL.	DATA PL.	ÁREA (ha)	VARIEDADE
1	06/2025	34.46	RB127825
TOTAL PLANTIO		34.46	

ÁREAS	(ha)	(%)
PLANTIO	34.46	93.68
CARREADORES	1.48	4.03
OUTROS	0.00	0.00
SUB TOTAL AGRICULTÁVEL	35.94	97.72
AP.P.	0.00	0.00
ÁRVORES	0.03	0.08
OUTROS	0.81	2.20
SUB TOTAL NÃO AGRICULT.	0.84	2.28
ÁREA TOTAL	36.78	100.00

C. NÍVEL: 2598.06 m/l 0.60 ha 1.62 %


LEGENDA

- FAZENDA
- TALHÃO
- REDE ELÉTRICA
- TERRAÇO BASE LARGA
- TERRAÇO EMBUTIDO
- (P.O.A) PATIO DE OPERAÇÃO

ESPAÇAMENTO: 1.50 x 1.50
TIRO MÉDIO ESTIMADO: 179.04 m
D.V: 5.53%

ESCALA: 1: 5.000

CROQUI DE ACESSO

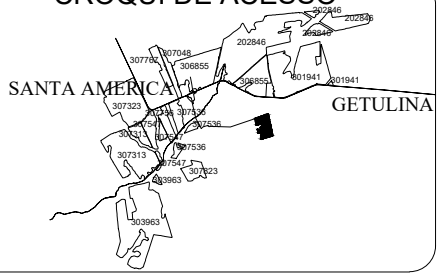

SÍTIO BARRO PRETO

PROPRIETÁRIO: LEONARDO PENARIOL AGOSTINHO
COMPRADOR: CLEALCO
MUNICÍPIO: GETULINA - SP

DISTÂNCIAS (km):
UNID. I - Asfalto: 88.50 Terra.: 5.00
UNID.I I - Asfalto: 32.00 Terra.: 5.00

COORDENADAS: E(X): 600483.50 N(Y): 7588254.26
LAT: -21°48'24.0369" LONG: -50°1'40.3157"

CLEALCO - AÇÚCAR E ALCOOL S/A - DEPARTAMENTO DE GEOTECNOLOGIA

LEVANTAMENTO VIA:
SATÉLITE
GPS / VANT
GOOGLE

UNIDADE: II
PARTE: A/A
FUNDO AGRÍCOLA: 308049

M:\01-Mapa de safra\Mapas Atualizados\Terceiro\308049 - Sitio Barro Preto (Leonardo Penariol Agostinho)\308049 - Sitio Barro Preto (Leonardo Penariol Agostinho).dwg

Bruno Gamboa 06/01/26