
Clealco
Açúcar, Etanol e Energia

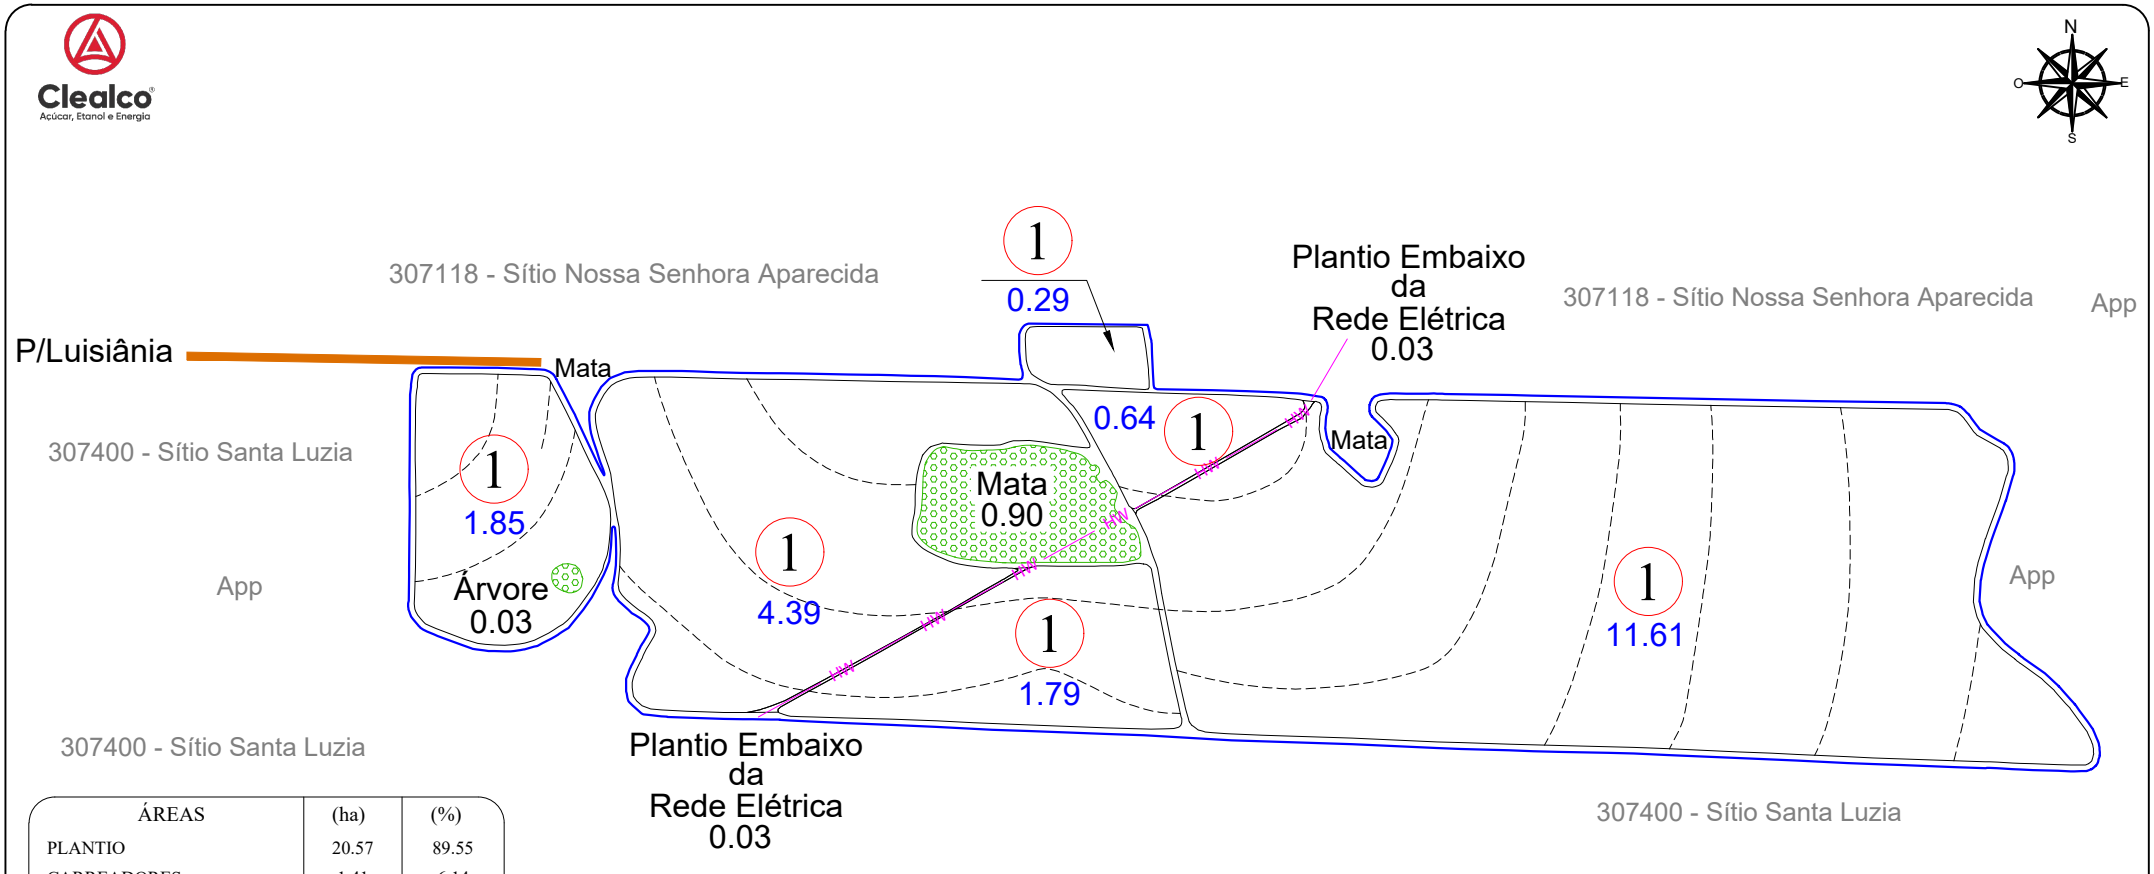

ÁREAS	(ha)	(%)
PLANTIO	20.57	89.55
CARREADORES	1.41	6.14
OUTROS	0.00	0.00
SUB TOTAL AGRICULTÁVEL	21.98	95.69
AP.P.	0.00	0.00
ÁRVORES	0.93	4.05
OUTROS	0.06	0.26
SUB TOTAL NÃO AGRICULT.	0.99	4.31
ÁREA TOTAL	22.97	100.00

C. NÍVEL: 2780.64 m/l 0.64 ha 2.78 %


Nº TAL.	DATA PL.	ÁREA (ha)	VARIEDADE
1	05/2025	20.57	RB 975201
TOTAL PLANTIO		20.57	

ESCALA: 1: 5.000

LEGENDA
- FAZENDA
- TALHÃO
- REDE ELÉTRICA
- TERRAÇO BASE LARGA
- TERRAÇO EMBUTIDO

ESPAÇAMENTO: 1.50 x 1.50
TIRO MÉDIO ESTIMADO: 159.60 m
D.V: 2.90 %

CROQUI DE ACESSO

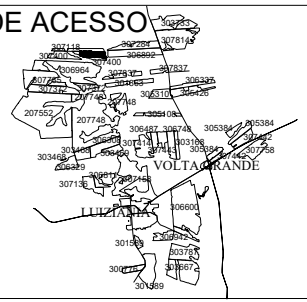

SÍTIO N.S. DA CONCEIÇÃO MONTESINA

PROPRIETÁRIO: DENILSON MIRON SERRANO
COMPRADOR: CLEALCO
MUNICÍPIO: CLEMENTINA - SP

DISTÂNCIAS (km):
UNID. I - Asfalto: 13.00 Terra.: 0.00
UNID.I I - Asfalto: 31.00 Terra.: 8.00

COORDENADAS: E(X): 567684.09 N(Y): 7609235.32
LAT: -21°37'7.2873" LONG: -50°20'45.6835"
CLEALCO - AÇÚCAR E ALCOOL S/A - DEPARTAMENTO DE GEOTECNOLOGIA

LEVANTAMENTO VIA:
- SATÉLITE
- GPS / VANT
- GOOGLE

UNIDADE: II
PARTE: A/A
FUNDO AGRÍCOLA: 308051

M:\01-Mapa de safra\Mapas Atualizados\Terceiro\308051 - Sítio Nossa Senhora Da Conceição Montesina (Denilson Miron Serrano)\308051 - Sítio Nossa Senhora Da Conceição Montesina (Denilson Miron Serrano).dwg

Bruno Gamboa 06/01/26