
Clealco
Açúcar, Etanol e Energia

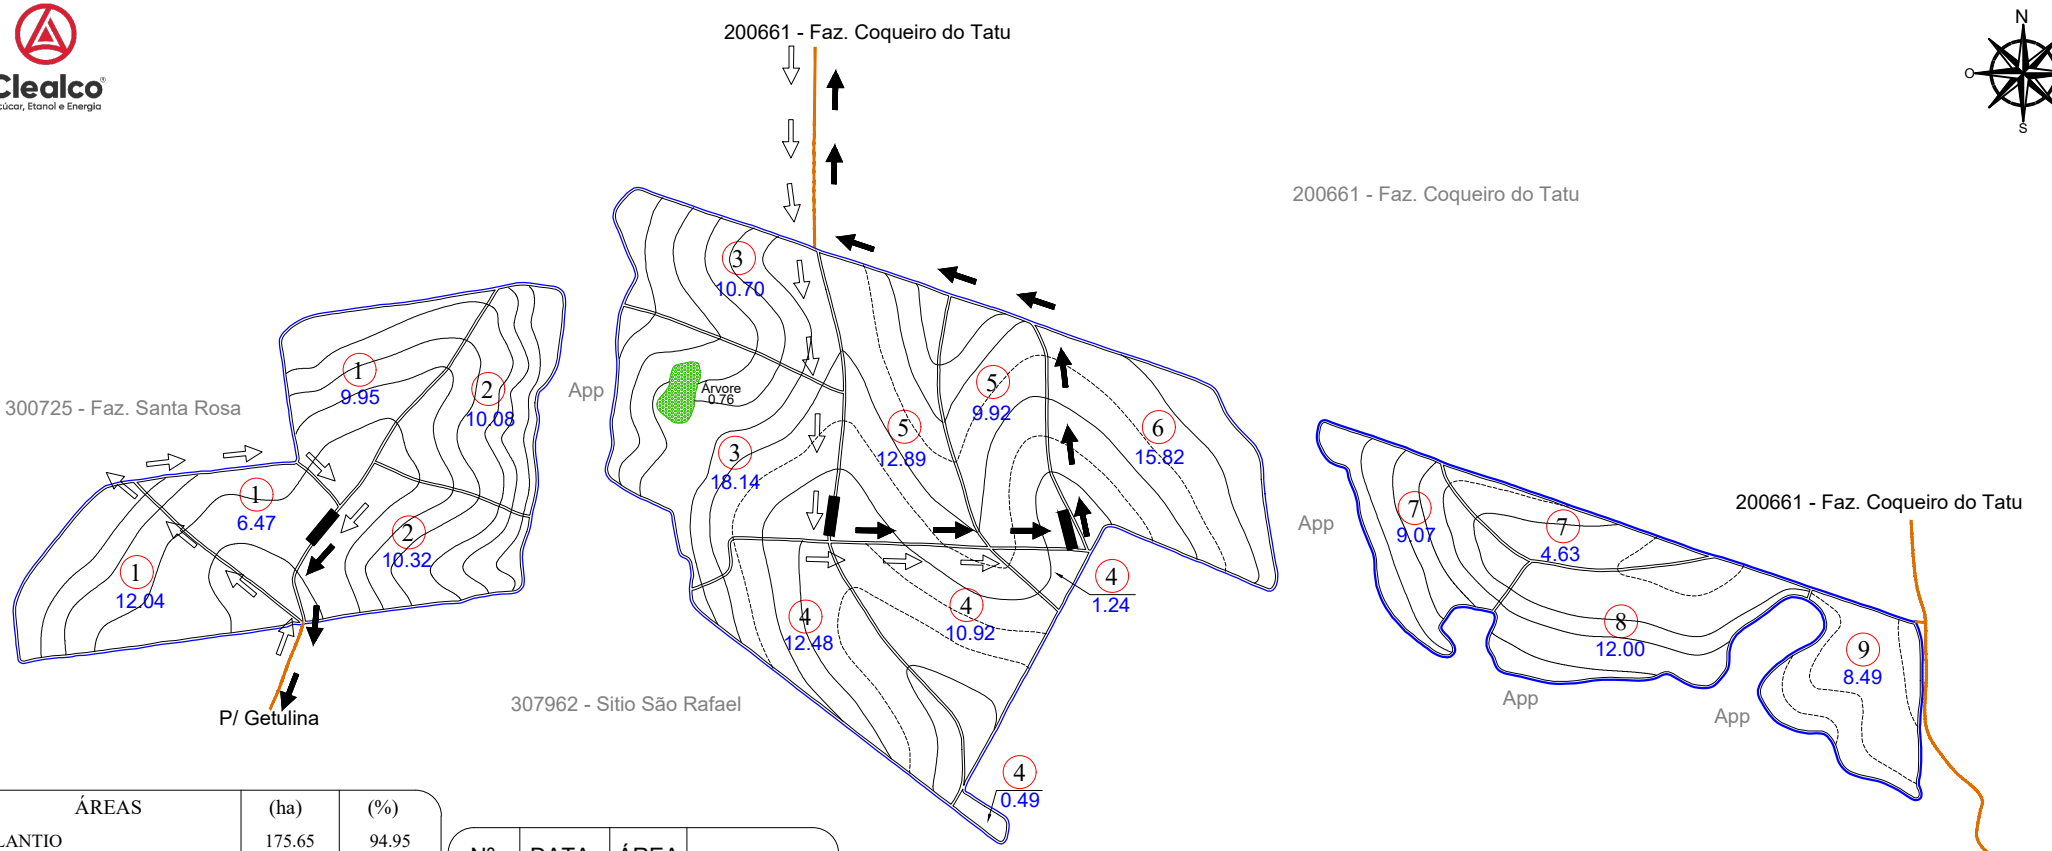

ÁREAS	(ha)	(%)
PLANTIO	175.65	94.95
CARREADORES	8.58	4.64
OUTROS	0.00	0.00
SUB TOTAL AGRICULTÁVEL	184.23	99.59
AP.P.	0.00	0.00
ÁRVORES	0.76	0.41
OUTROS	0.00	0.00
SUB TOTAL NÃO AGRICULT.	0.76	0.41
ÁREA TOTAL	184.99	100.00

C. NÍVEL: 20615.84 m/l 4.74 ha 2.56 %

Nº TAL.	DATA PL.	ÁREA (ha)	VARIEDADE
1	2026	28.46	PRÉ PLANTIO
2		20.40	
3		28.84	
4		25.13	
5		22.81	
6		15.82	
7		13.70	
8		12.00	
9		8.49	
TOTAL PLANTIO		175.65	


ESCALA: 1: 16.000

LEGENDA

- FAZENDA
- TALHÃO
- REDE ELÉTRICA
- TERRAÇO BASE LARGA
- TERRAÇO EMBUTIDO
- VAZIO
- CARREGADO

ESPAÇAMENTO: 1.50 x 1.50
TIRO MÉDIO ESTIMADO: 259.97 m
D.V: 4.39 %

CROQUI DE ACESSO

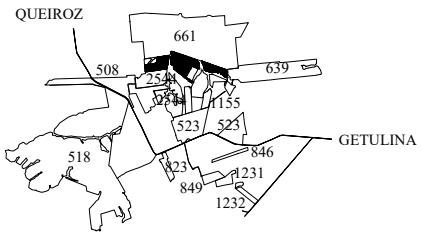

SÍTIO ALVORADA I

PROPRIETÁRIO: CLEBER AMARAL HUNGARO
COMPRADOR: CLEALCO
MUNICÍPIO: GETULINA - SP

DISTÂNCIAS (km):
UNID. I - Asfalto: 74.00 Terra.: 10.80
UNID.I I - Asfalto: 16.00 Terra.: 10.80

COORDENADAS: E(X): 597877.78 N(Y): 7593159.44
LAT: -21°45'45.0437" LONG: -50°3'12.1067"
CLEALCO - AÇÚCAR E ALCOOL S/A - DEPARTAMENTO DE GEOTECNOLOGIA

LEVANTAMENTO VIA:
SATÉLITE
GPS / VANT
GOOGLE

UNIDADE: II
PARTE: A/A
FUNDO AGRÍCOLA: 308070

M:\01-Mapa de safra\Mapas Atualizados\Terceiro\308070 - Sítio Alvorada I (Cleber Amaral Hungaro)\308070 - Sítio Alvorada I (Cleber Amaral Hungaro).dwg

Peterson Santos 12/06/2026