
Clealco
Açúcar, Etanol e Energia

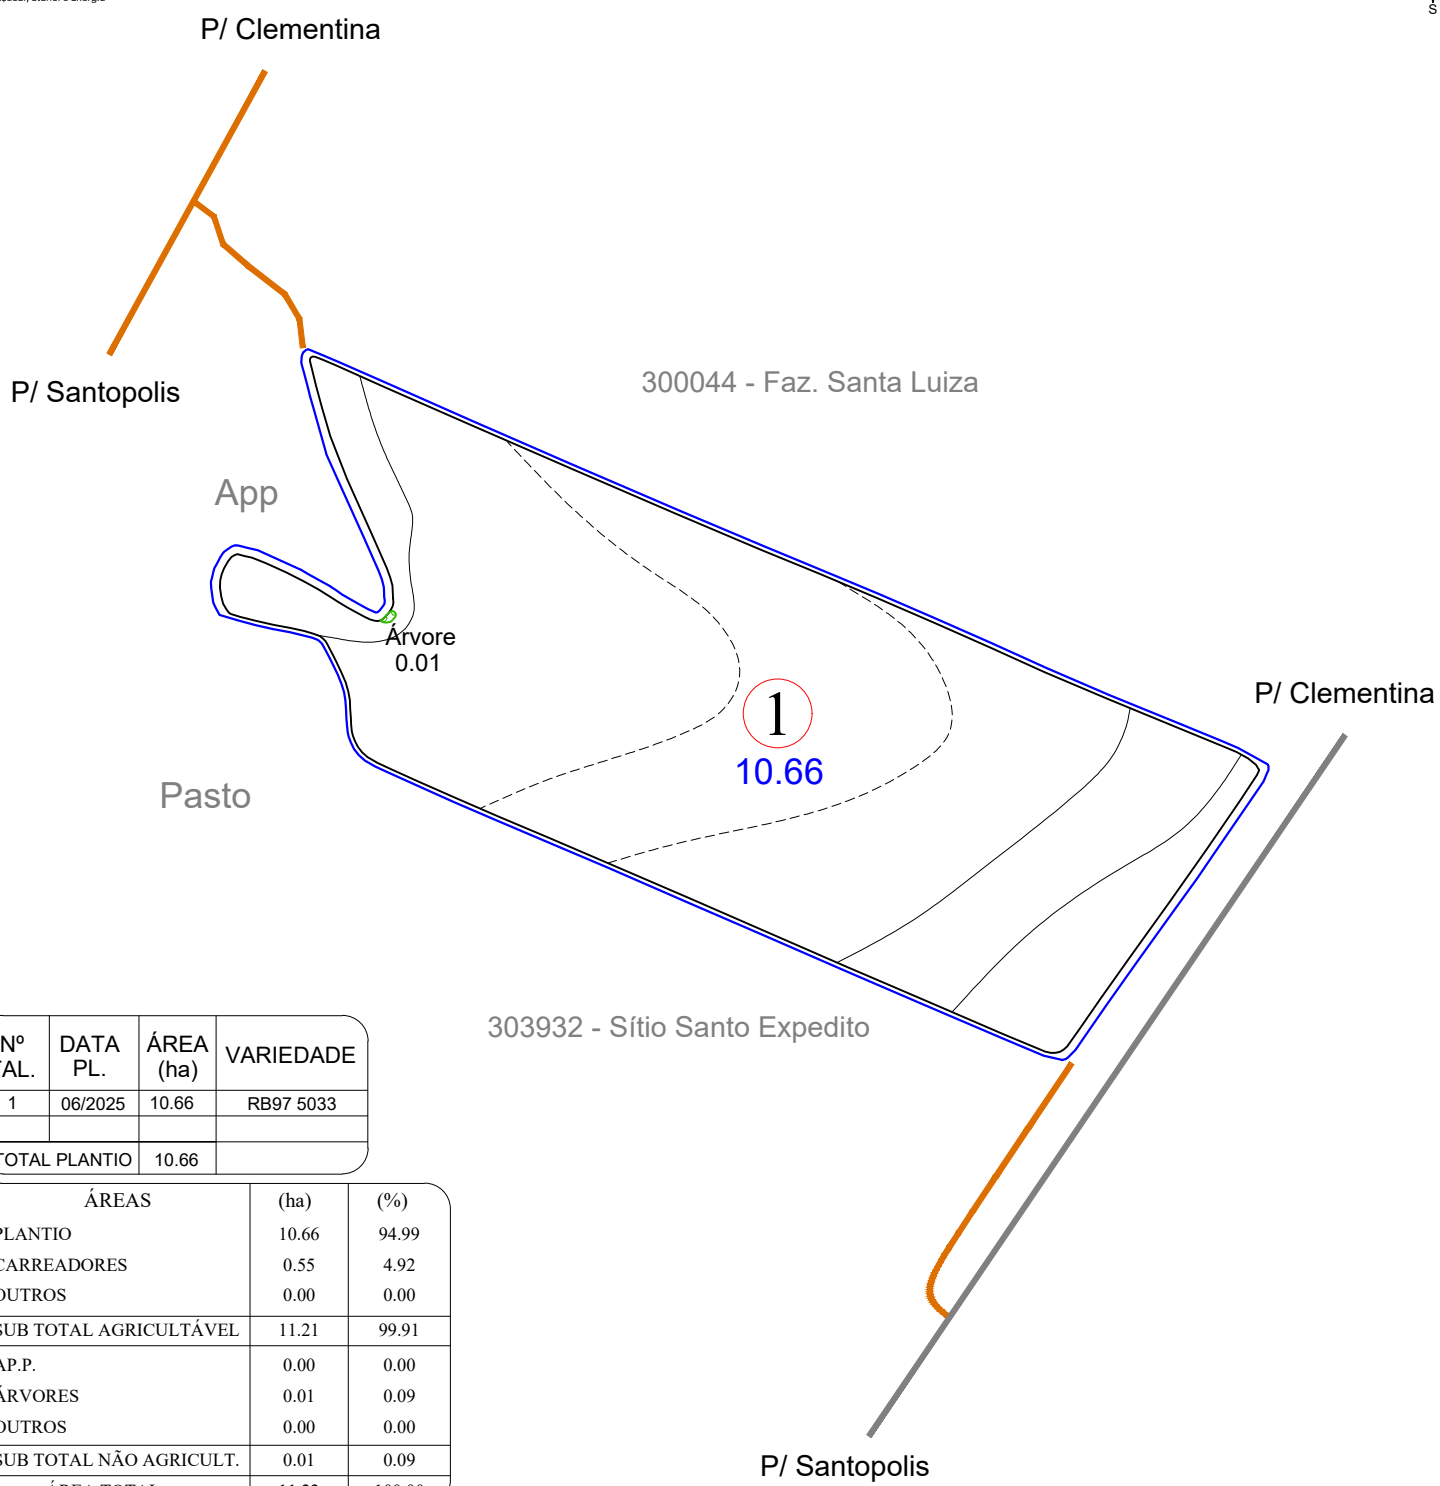

Nº TAL.	DATA PL.	ÁREA (ha)	VARIEDADE
1	06/2025	10.66	RB97 5033
TOTAL PLANTIO		10.66	

ÁREAS	(ha)	(%)
PLANTIO	10.66	94.99
CARREADORES	0.55	4.92
OUTROS	0.00	0.00
SUB TOTAL AGRICULTÁVEL	11.21	99.91
AP.P.	0.00	0.00
ÁRVORES	0.01	0.09
OUTROS	0.00	0.00
SUB TOTAL NÃO AGRICULT.	0.01	0.09
ÁREA TOTAL	11.22	100.00

C. NÍVEL: 667.10 m/l 0.15 ha 1.37 %


LEGENDA

- FAZENDA
- TALHÃO
- REDE ELÉTRICA
- TERRAÇO BASE LARGA
- TERRAÇO EMBUTIDO
- (P.O.A) PATIO DE OPERAÇÃO

ESPAÇAMENTO: 1.50 x 1.50
TIRO MÉDIO ESTIMADO: 146.05 m
D.V: 4.52 %

ESCALA: 1: 4.500

CROQUI DE ACESSO

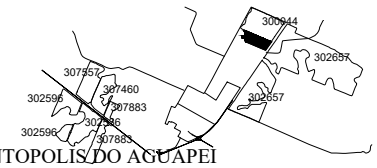

SÍTIO SÃO PEDRO

PROPRIETÁRIO: SIDNEI PEREIRA BRITO
COMPRADOR: CLEALCO
MUNICÍPIO: SANTÓPOLIS DO AGUAPEÍ - SP

DISTÂNCIAS (km):
UNID. I - Asfalto: 11.50 Terra.: 1.00
UNID.I I - Asfalto: 41.50 Terra.: 1.50

COORDENADAS: E(X): 552934.74 N(Y): 7608719.64
LAT: -21°37'25.8572" LONG: -50°29'18.6467"
CLEALCO - AÇÚCAR E ALCOOL S/A - DEPARTAMENTO DE GEOTECNOLOGIA

LEVANTAMENTO VIA:
- SATÉLITE
- GPS / VANT
- GOOGLE

UNIDADE: I
PARTE: A/A
FUNDO AGRÍCOLA: 308072

M:\01-Mapa de safra\Mapas Atualizados\Terceiro\308072 - Sitio Boa Vista e São Pedro (Sidnei Pereira Brito)\308072 - Sitio Boa Vista e São Pedro (Sidnei Pereira Brito).dwg

Bruno Gamboa 04/02/26