
Clealco
Açúcar, Etanol e Energia

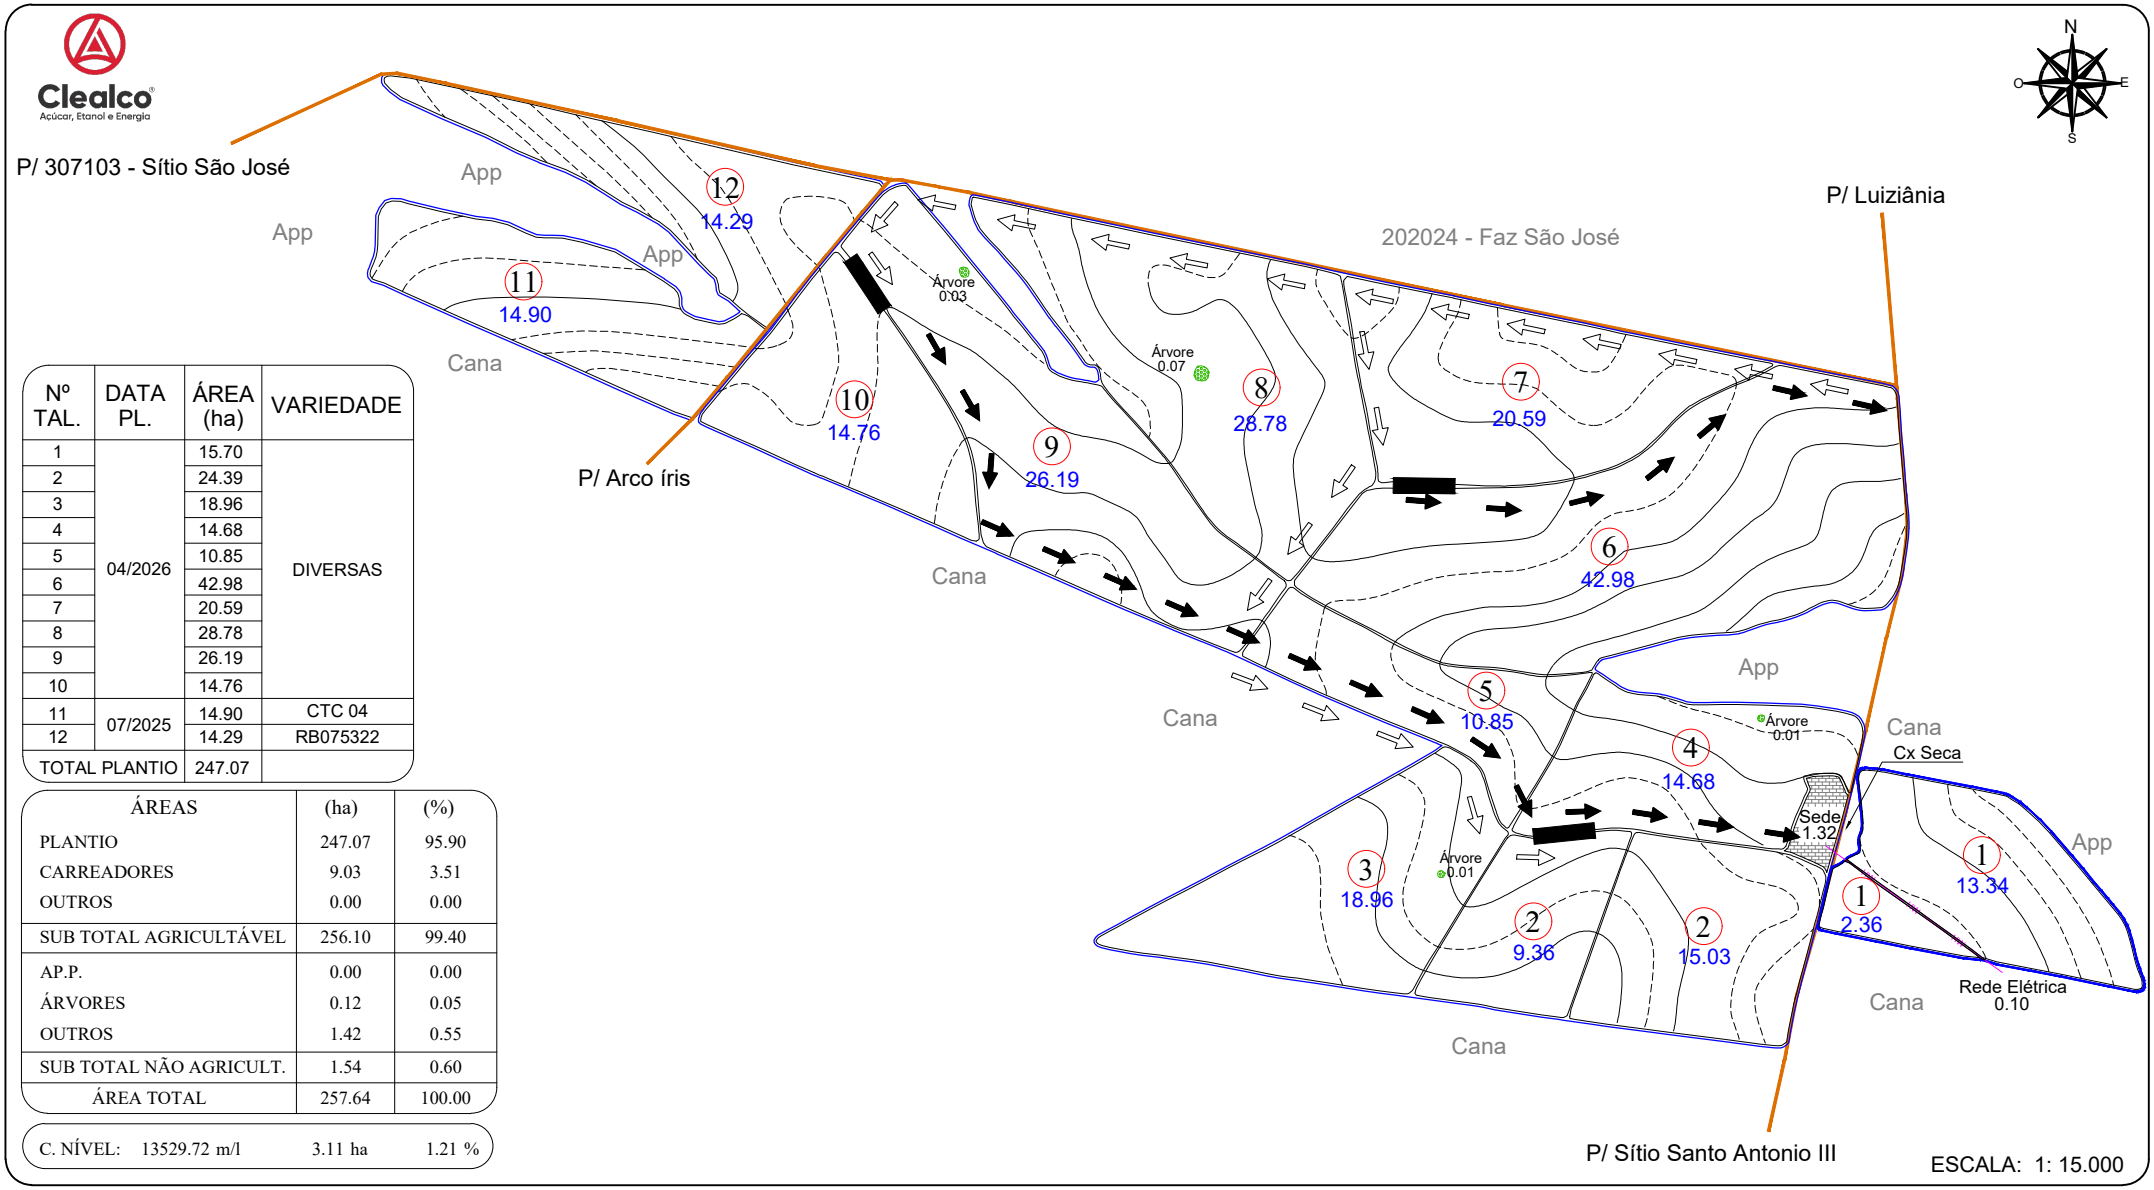


| Nº TAL. | DATA PL. | ÁREA (ha) | VARIEDADE |
|---|---|---|---|
| 1 | 04/2026 | 15.70 | DIVERSAS |
| 2 | | 24.39 | |
| 3 | | 18.96 | |
| 4 | | 14.68 | |
| 5 | | 10.85 | |
| 6 | | 42.98 | |
| 7 | | 20.59 | |
| 8 | | 28.78 | |
| 9 | | 26.19 | |
| 10 | | 14.76 | |
| 11 | 07/2025 | 14.90 | CTC 04 |
| 12 | | 14.29 | RB075322 |
| TOTAL PLANTIO | | 247.07 | |

| ÁREAS | (ha) | (%) |
|---|---|---|
| PLANTIO | 247.07 | 95.90 |
| CARREADORES | 9.03 | 3.51 |
| OUTROS | 0.00 | 0.00 |
| SUB TOTAL AGRICULTÁVEL | 256.10 | 99.40 |
| AP.P. | 0.00 | 0.00 |
| ÁRVORES | 0.12 | 0.05 |
| OUTROS | 1.42 | 0.55 |
| SUB TOTAL NÃO AGRICULT. | 1.54 | 0.60 |
| ÁREA TOTAL | 257.64 | 100.00 |

C. NÍVEL: 13529.72 m/l 3.11 ha 1.21 %


ESCALA: 1: 15.000

## LEGENDA

- FAZENDA
- TALHÃO
- REDE ELÉTRICA
- TERRAÇO BASE LARGA
- TERRAÇO EMBUTIDO
- VAZIO
- CARREGADO

ESPAÇAMENTO: 1.50 x 1.50
TIRO MÉDIO ESTIMADO: 259,75 m
D.V: 4.67 %

## CROQUI DE ACESSO

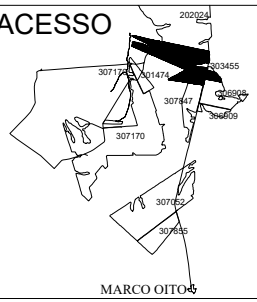


# FAZENDA BARREIRÃO

PROPRIETÁRIO: JOSÉ CARLOS BURANELLO
COMPRADOR: CLEALCO
MUNICÍPIO: ARCO IRIS - SP

DISTÂNCIAS (km):
UNID. I - Asfalto: 33.20 Terra.: 12.00
UNID.I I - Asfalto: 16.00 Terra.: 11.00

COORDENADAS: E(X): 569355.27 N(Y): 7589701.75
LAT: -21°47'42.3531" LONG: -50°19'44.6135"
CLEALCO - AÇÚCAR E ALCOOL S/A - DEPARTAMENTO DE GEOTECNOLOGIA

LEVANTAMENTO VIA:
SATÉLITE
GPS / VANT
GOOGLE

UNIDADE: II
PARTE: A/A
FUNDO AGRÍCOLA: 308080