
Clealco
Açúcar, Etanol e Energia

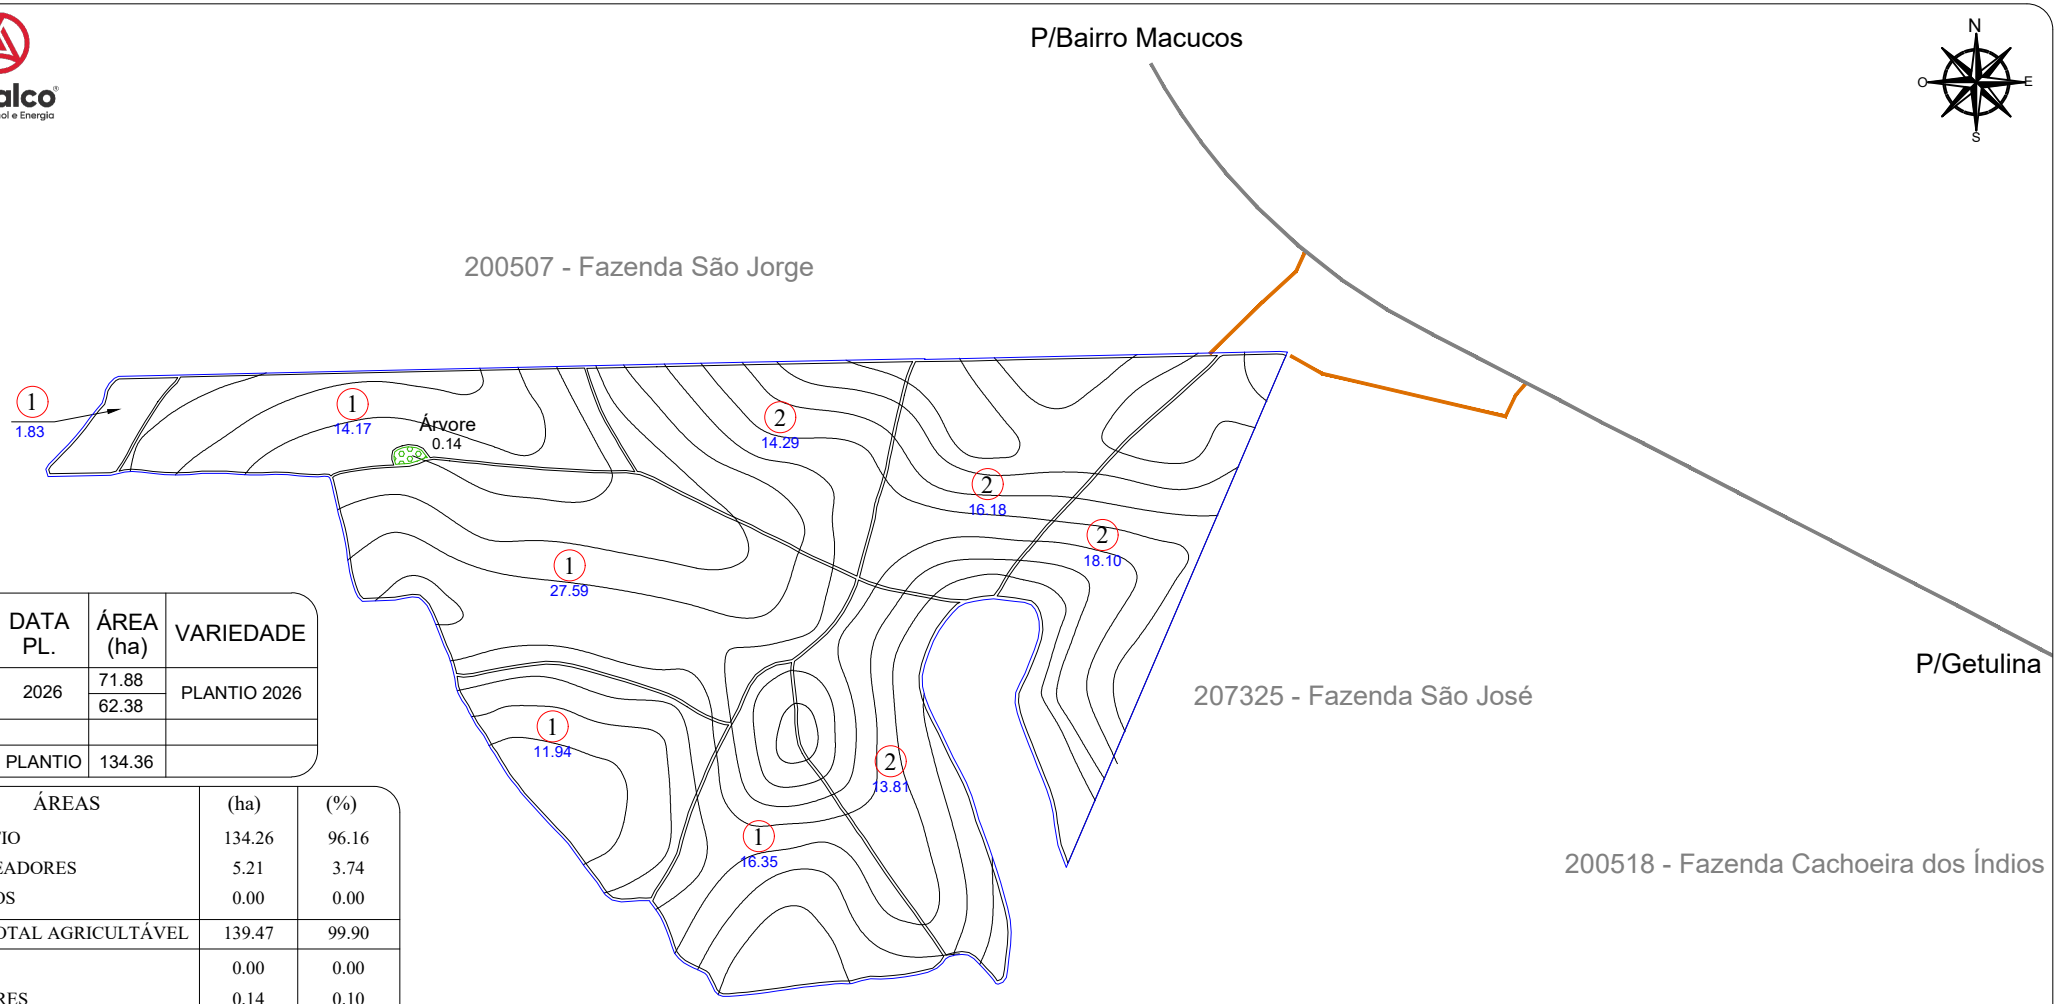

Nº TAL.	DATA PL.	ÁREA (ha)	VARIEDADE
1	2026	71.88	PLANTIO 2026
2		62.38	
TOTAL PLANTIO		134.36	

ÁREAS	(ha)	(%)
PLANTIO	134.26	96.16
CARREADORES	5.21	3.74
OUTROS	0.00	0.00
SUB TOTAL AGRICULTÁVEL	139.47	99.90
AP.P.	0.00	0.00
ÁRVORES	0.14	0.10
OUTROS	0.00	0.00
SUB TOTAL NÃO AGRICULT.	0.14	0.10
ÁREA TOTAL	139.61	100.00

C. NÍVEL: 21310.39 m/l 4.90 ha 3.51 %


ESCALA: 1: 14.000

LEGENDA

- FAZENDA
- TALHÃO
- REDE ELÉTRICA
- TERRAÇO BASE LARGA
- TERRAÇO EMBUTIDO

ESPAÇAMENTO: 1.50 x 1.50
TIRO MÉDIO ESTIMADO: 200.98 m
D.V: 4.61 %

CROQUI DE ACESSO

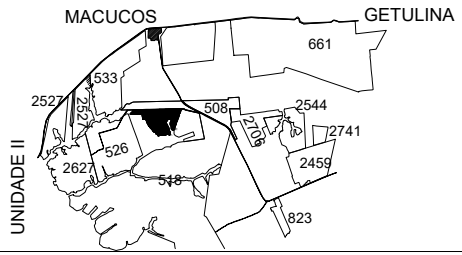

FAZENDA SÃO JORGE

PROPRIETÁRIO: REGIS H. DE CASTRO VENTURA
COMPRADOR: CLEALCO
MUNICÍPIO: GETULINA - SP

DISTÂNCIAS (km):
UNID. I - Asfalto: 71.00 Terra.: 0.50
UNID.I I - Asfalto: 18.50 Terra.: 3.50

COORDENADAS: E(X): 592271.50 N(Y): 7591702.83
LAT: -21°46'33.4994" LONG: -50°6'26.9937"

CLEALCO - AÇÚCAR E ALCOOL S/A - DEPARTAMENTO DE GEOTECNOLOGIA

UNIDADE:
II
PARTE:
A/A
FUNDO AGRÍCOLA:
308081