

Clealco
Açúcar, Etanol e Energia

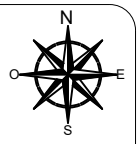

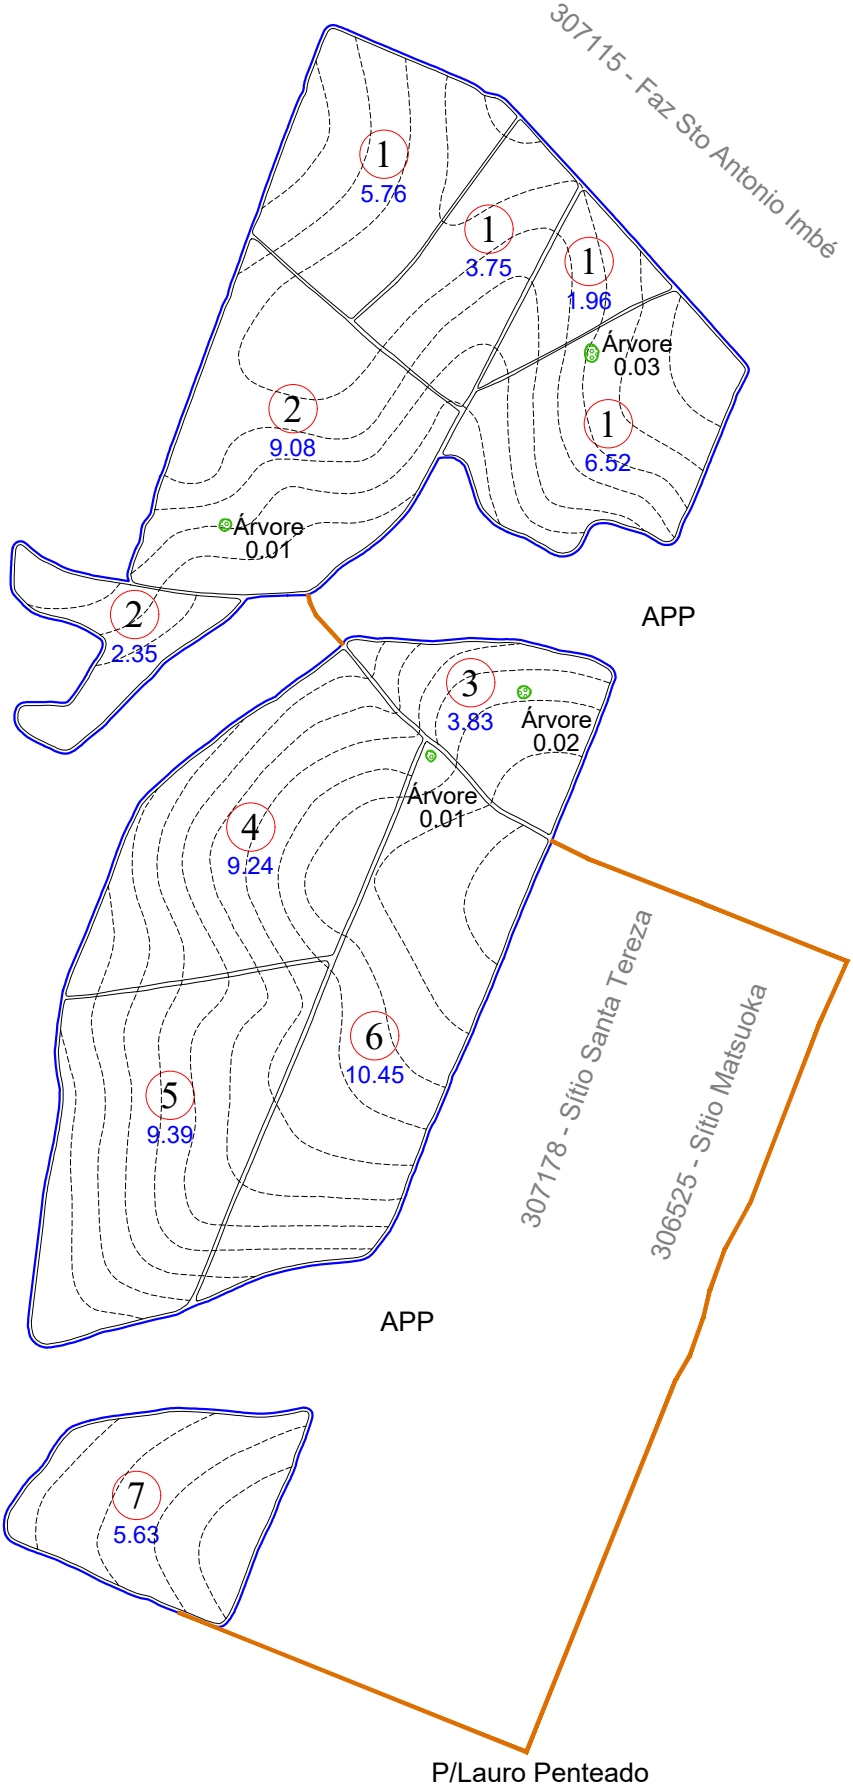

Nº TAL.	DATA PL.	ÁREA (ha)	VARIEDADE
1	04/2025	17.99	CTC 04
2		11.43	
3		3.83	
4		9.24	
5		9.39	
6		10.45	
7		5.63	
TOTAL PLANTIO		67.96	

ÁREAS	(ha)	(%)
PLANTIO	67.96	94.71
CARREADORES	3.73	5.19
OUTROS	0.00	0.00
SUB TOTAL AGRICULTÁVEL	71.69	99.90
AP.P.	0.00	0.00
ÁRVORES	0.07	0.10
OUTROS	0.00	0.00
SUB TOTAL NÃO AGRICULT.	0.07	0.10
ÁREA TOTAL	71.76	100.00

C. NÍVEL:	0.00 m/l	0.00 ha	0.00 %


LEGENDA

- FAZENDA
- TALHÃO
- REDE ELÉTRICA
- TERRAÇO BASE LARGA
- TERRAÇO EMBUTIDO
- (P.O.A) PATIO DE OPERAÇÃO

ESPAÇAMENTO: 1.50 x 1.50
TIRO MÉDIO ESTIMADO: 198.38 m
D.V: 6.80 %

ESCALA: 1: 9.000

CROQUI DE ACESSO

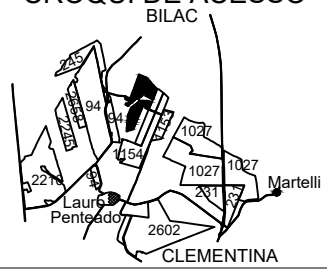

SÍTIO SÃO JOAQUIM V

PROPRIETÁRIO: JOSÉ CARLOS GARCIA
COMPRADOR: CLEALCO
MUNICÍPIO: CLEMENTINA - SP

DISTÂNCIAS (km):
UNID. I - Asfalto: 10.50 Terra.: 2.95
UNID.I I - Asfalto: 66.50 Terra.: 2.95

COORDENADAS: E(X): 556986.62 N(Y): 7623927.83
LAT: -21°29'10.7653" LONG: -50°26'59.5714"

CLEALCO - AÇÚCAR E ALCOOL S/A - DEPARTAMENTO DE GEOTECNOLOGIA

LEVANTAMENTO VIA:
- SATÉLITE
- GPS / VANT
- GOOGLE

UNIDADE: I
PARTE: A/A
FUNDO AGRÍCOLA: 308093

M:\01-Mapa de safra\Mapas Atualizados\Terceiro\308093 - Sitio São Joaquim V (Jose Carlos Garcia)\308093 - Sitio São Joaquim V (Jose Carlos Garcia).dwg

Bruno Gamboa 03/02/26