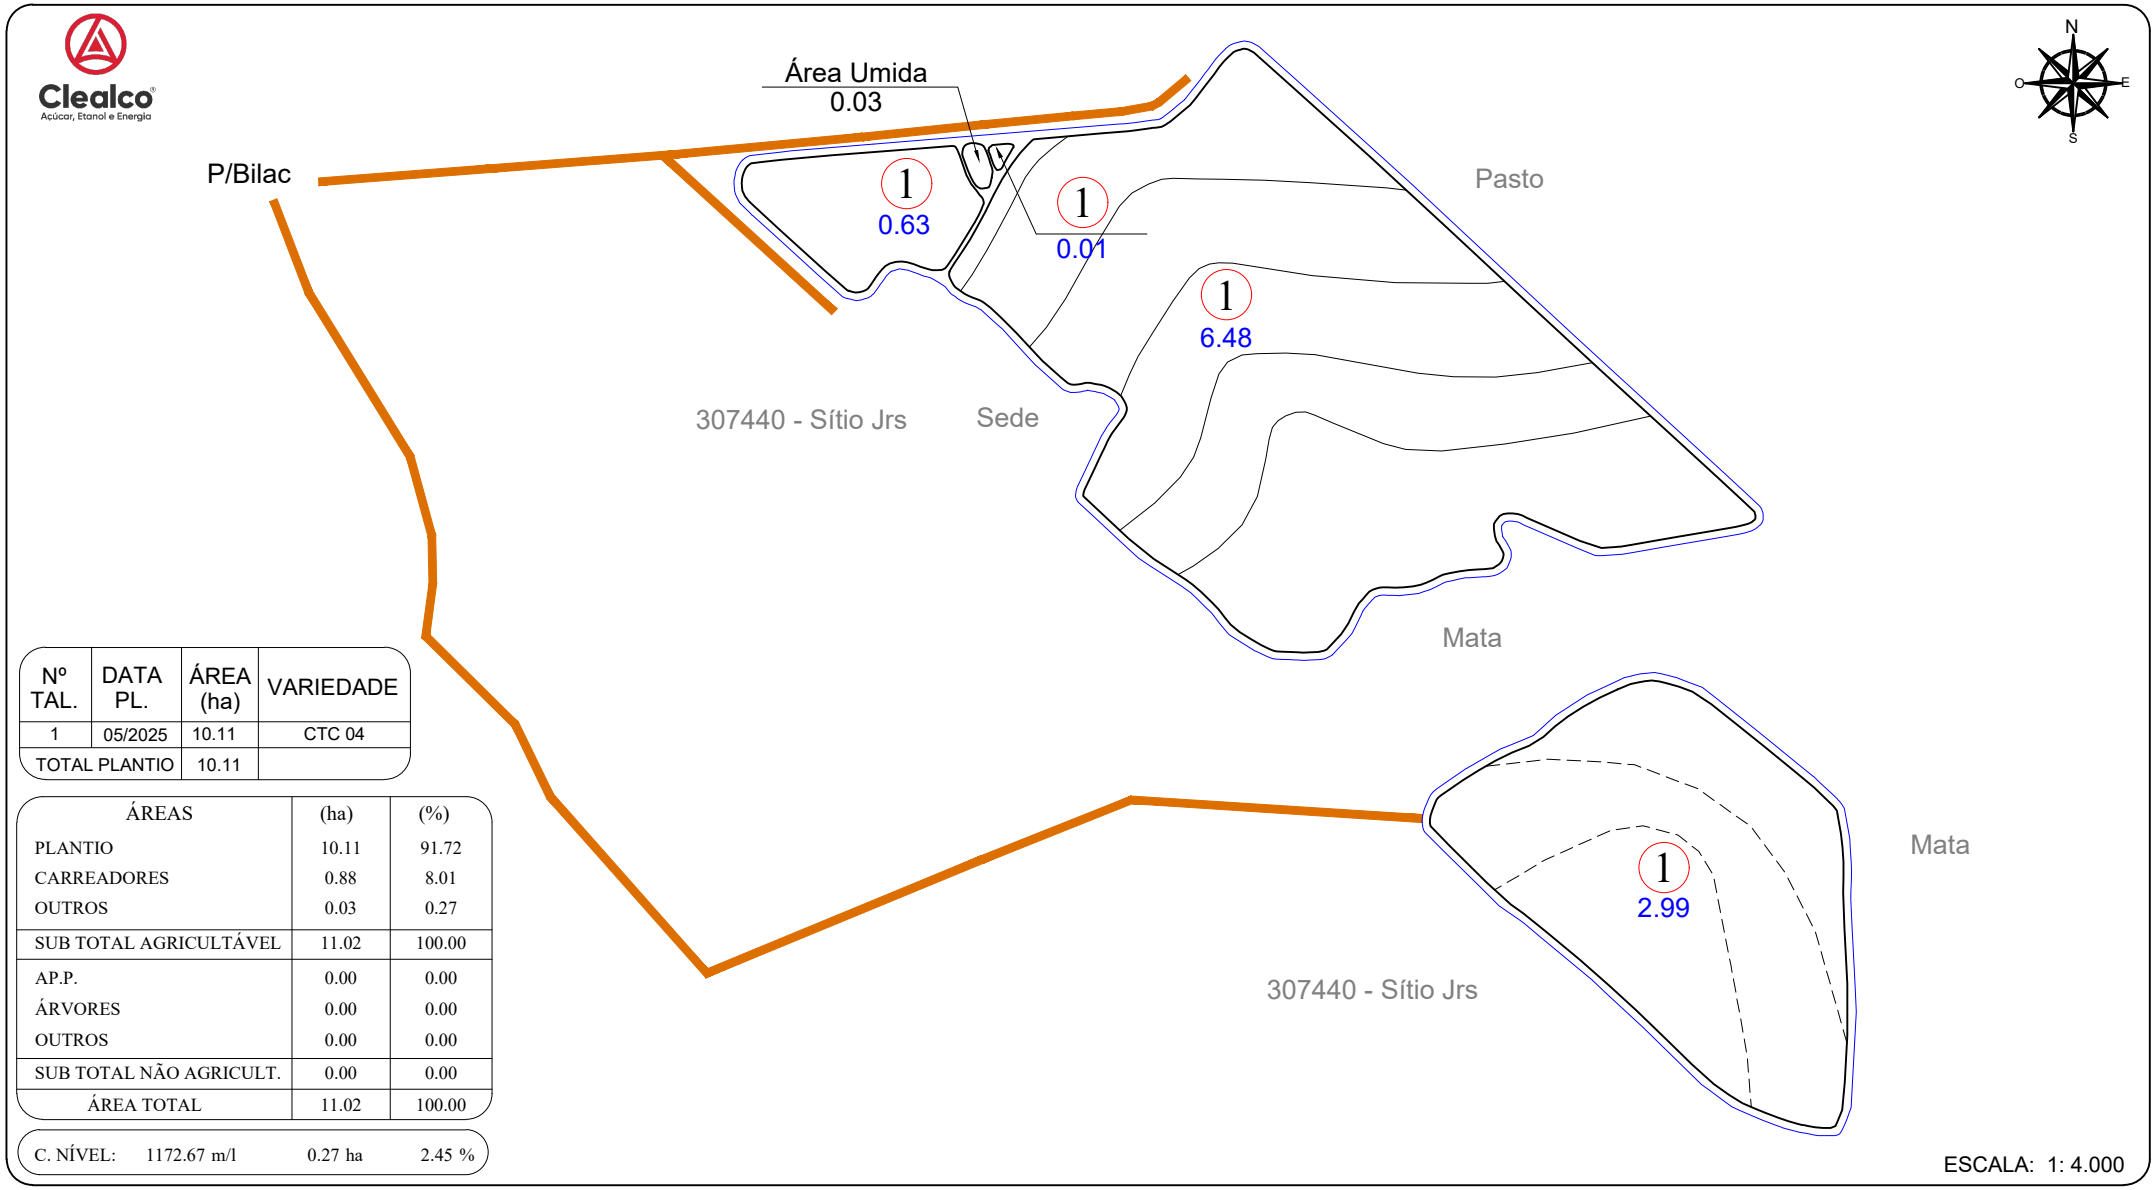


Nº TAL.	DATA PL.	ÁREA (ha)	VARIEDADE
1	05/2025	10.11	CTC 04
TOTAL PLANTIO		10.11	

ÁREAS	(ha)	(%)
PLANTIO	10.11	91.72
CARREADORES	0.88	8.01
OUTROS	0.03	0.27
SUB TOTAL AGRICULTÁVEL	11.02	100.00
AP.P.	0.00	0.00
ÁRVORES	0.00	0.00
OUTROS	0.00	0.00
SUB TOTAL NÃO AGRICULT.	0.00	0.00
ÁREA TOTAL	11.02	100.00

C. NÍVEL: 1172.67 m/l 0.27 ha 2.45 %


ESCALA: 1: 4.000

LEGENDA

- FAZENDA
- TALHÃO
- REDE ELÉTRICA
- TERRAÇO BASE LARGA
- TERRAÇO EMBUTIDO
- VAZIO
- CARREGADO

ESPAÇAMENTO: 1.50 x 1.50
TIRO MÉDIO ESTIMADO: 144.86 m
D.V: 6.54%

CROQUI DE ACESSO

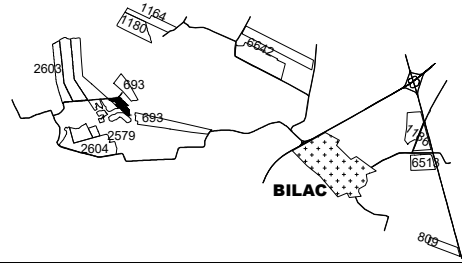

SÍTIO SÃO JOSÉ

PROPRIETÁRIO: ANTONIO ROBERTO GENARI
COMPRADOR: CLEALCO
MUNICÍPIO: BILAC - SP

DISTÂNCIAS (km):
UNID. I - Asfalto: 33.10 Terra.: 1.60
UNID.I I - Asfalto: 81.50 Terra.: 1.60

COORDENADAS: E(X): 549268.62 N(Y): 7634527.19
LAT: -21°23'26.8386" LONG: -50°31'28.9006"

CLEALCO - AÇÚCAR E ALCOOL S/A - DEPARTAMENTO DE GEOTECNOLOGIA

LEVANTAMENTO VIA:
SATÉLITE
GPS / VANT
GOOGLE

UNIDADE: I
PARTE: A/A
FUNDO AGRÍCOLA: 308100

M:\01-Mapa de safra\Mapas Atualizados\Terceiro\308100 - Sítio São José (Antonio Roberto Genari)\308100 - Sítio São José (Antonio Roberto Genari).dwg

Bruno Gamboa 10/03/26