
Clealco
Açúcar, Etanol e Energia

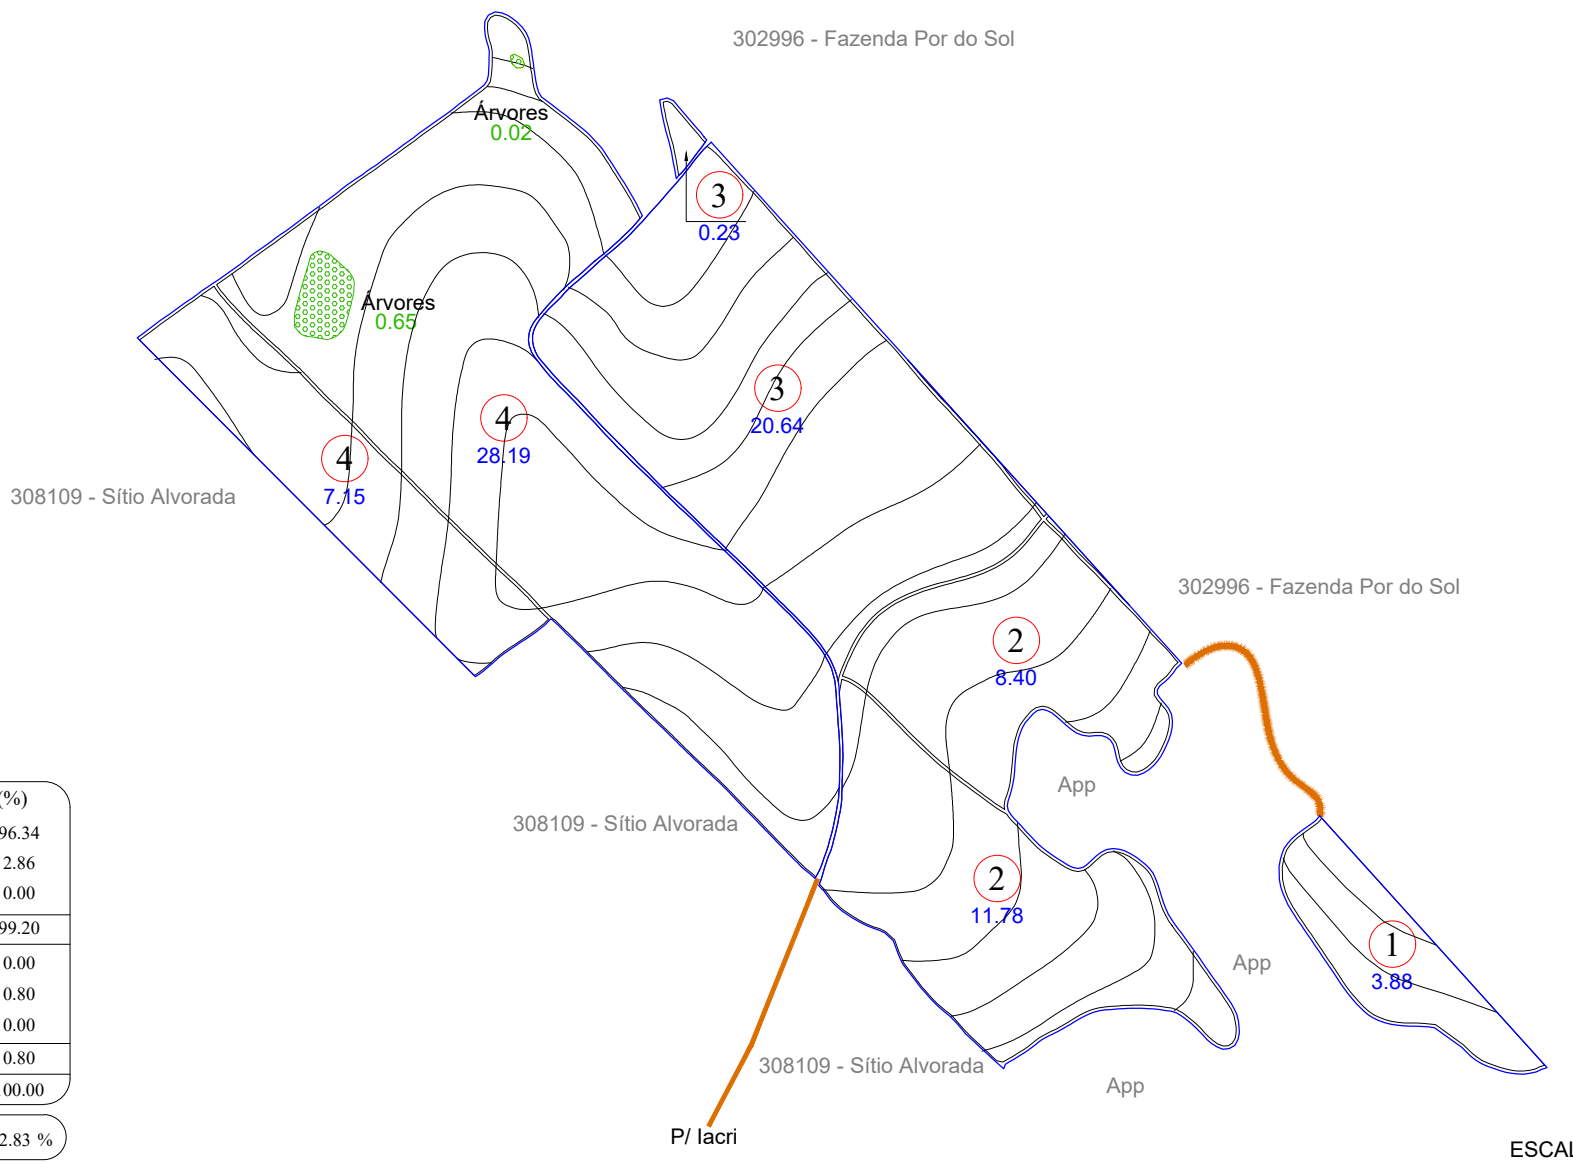

N
O
E
S

Nº TAL.	DATA PL.	ÁREA (ha)	VARIEDADE
1	2026	3.88	REFORMA
2		20.18	
3		20.87	
4		35.34	
TOTAL PLANTIO		80.27	

ÁREAS	(ha)	(%)
PLANTIO	80.27	96.34
CARREADORES	2.38	2.86
OUTROS	0.00	0.00
SUB TOTAL AGRICULTÁVEL	82.65	99.20
AP.P.	0.00	0.00
ÁRVORES	0.67	0.80
OUTROS	0.00	0.00
SUB TOTAL NÃO AGRICULT.	0.67	0.80
ÁREA TOTAL	83.32	100.00


C. NÍVEL: 10258.29 m/l 2.36 ha 2.83 %

ESCALA: 1: 10.000

LEGENDA
- FAZENDA
- TALHÃO
- REDE ELÉTRICA
- TERRAÇO BASE LARGA
- TERRAÇO EMBUTIDO
- VAZIO
- CARREGADO

ESPAÇAMENTO: 1.50 x 1.50
TIRO MÉDIO ESTIMADO: 000.00 m
D.V: 5.43 %

CROQUI DE ACESSO

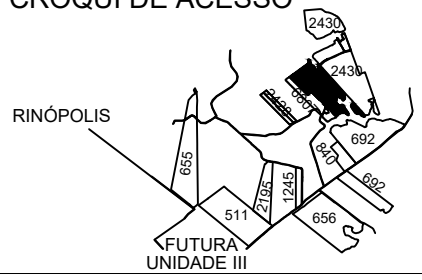

SÍTIO SALVADOR

PROPRIETÁRIO: ROBERLEI BUENO DE OLIVEIRA
COMPRADOR: CLEALCO
MUNICÍPIO: IACRI - SP

DISTÂNCIAS (km):
UNID. I - Asfalto: 35.70 Terra.: 7.70
UNID.I I - Asfalto: 70.00 Terra.: 8.50

COORDENADAS: E(X): 546020.50 N(Y): 7591402.65
LAT: -21°46'49.7773" LONG: -50°33'17.4242"
CLEALCO - AÇÚCAR E ALCOOL S/A - DEPARTAMENTO DE GEOTECNOLOGIA

LEVANTAMENTO VIA:
SATÉLITE
GPS / VANT
GOOGLE

UNIDADE: II
PARTE: A/A
FUNDO AGRÍCOLA: 308108

M:\01-Mapa de safra\Mapas Atualizados\Terceiro\308108 - Sitio Salvador (Roberlei Bueno De Oliveira)\308108 - Sitio Salvador (Roberlei Bueno De Oliveira).dwg

Bruno Gamboa 19/03/26