
Clealco
Açúcar, Etanol e Energia

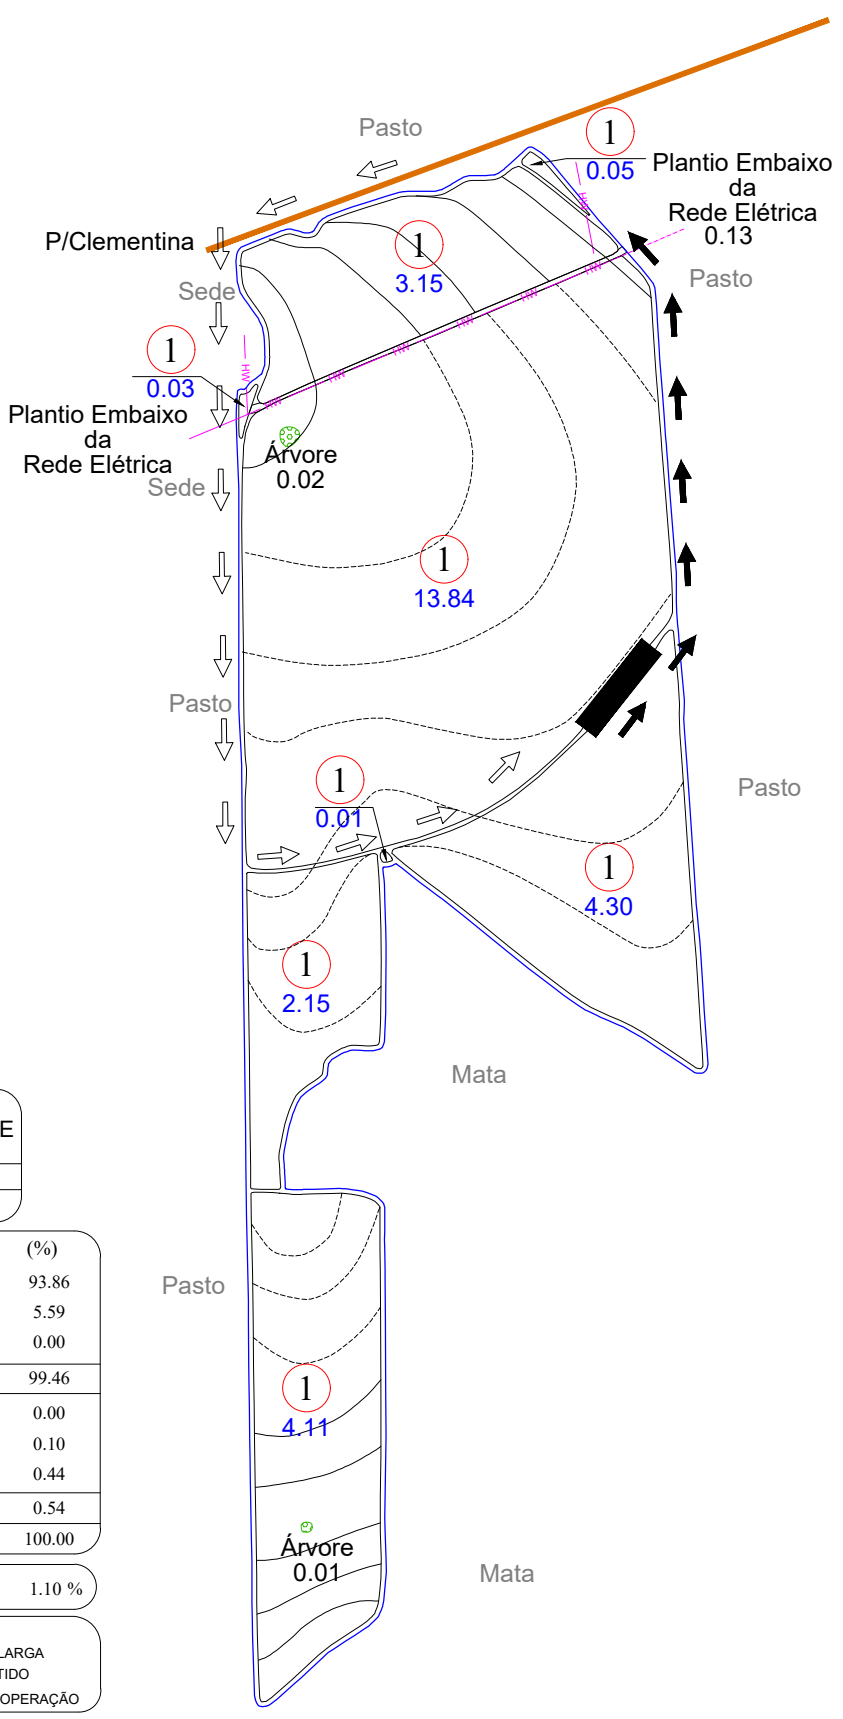

Nº TAL.	DATA PL.	ÁREA (ha)	VARIEDADE
1	04/2026	27.64	RB12 7825
TOTAL PLANTIO		27.64	

ÁREAS	(ha)	(%)
PLANTIO	27.64	93.86
CARREADORES	1.65	5.59
OUTROS	0.00	0.00
SUB TOTAL AGRICULTÁVEL	29.29	99.46
AP.P.	0.00	0.00
ÁRVORES	0.03	0.10
OUTROS	0.13	0.44
SUB TOTAL NÃO AGRICULT.	0.16	0.54
ÁREA TOTAL	29.45	100.00

C. NÍVEL: 1414.65 m/l 0.33 ha 1.10 %


LEGENDA

- FAZENDA
- TALHÃO
- REDE ELÉTRICA
- TERRAÇO BASE LARGA
- TERRAÇO EMBUTIDO
- (P.O.A) PATIO DE OPERAÇÃO

ESPAÇAMENTO: 1.50 x 1.50
TIRO MÉDIO ESTIMADO: 230.95 m
D.V: 4.63 %

ESCALA: 1: 6.500

CROQUI DE ACESSO

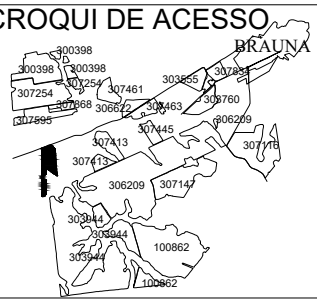

SÍTIO UNIÃO

PROPRIETÁRIO: RONALDO CÉSAR TRINDADE
COMPRADOR: CLEALCO
MUNICÍPIO: BRAÚNA - SP

DISTÂNCIAS (km):
UNID. I - Asfalto: 18.50 Terra.: 9.70
UNID.I I - Asfalto: 65.50 Terra.: 9.70

COORDENADAS: E(X): 564792.76 N(Y): 7618879.61
LAT: -21°31'54.0018" LONG: -50°22'27.5975"

CLEALCO - AÇÚCAR E ALCOOL S/A - DEPARTAMENTO DE GEOTECNOLOGIA

LEVANTAMENTO VIA:
- SATÉLITE
- GPS / VANT
- GOOGLE

UNIDADE: I
PARTE: A/A
FUNDO AGRÍCOLA: 308112

M:\01-Mapa de safra\Mapas Atualizados\Terceiro\308112 - Sitio União (Ronaldo Cesar Trindade)\308112 - Sitio União (Ronaldo Cesar Trindade).dwg

Bruno Gamboa 19/08/26