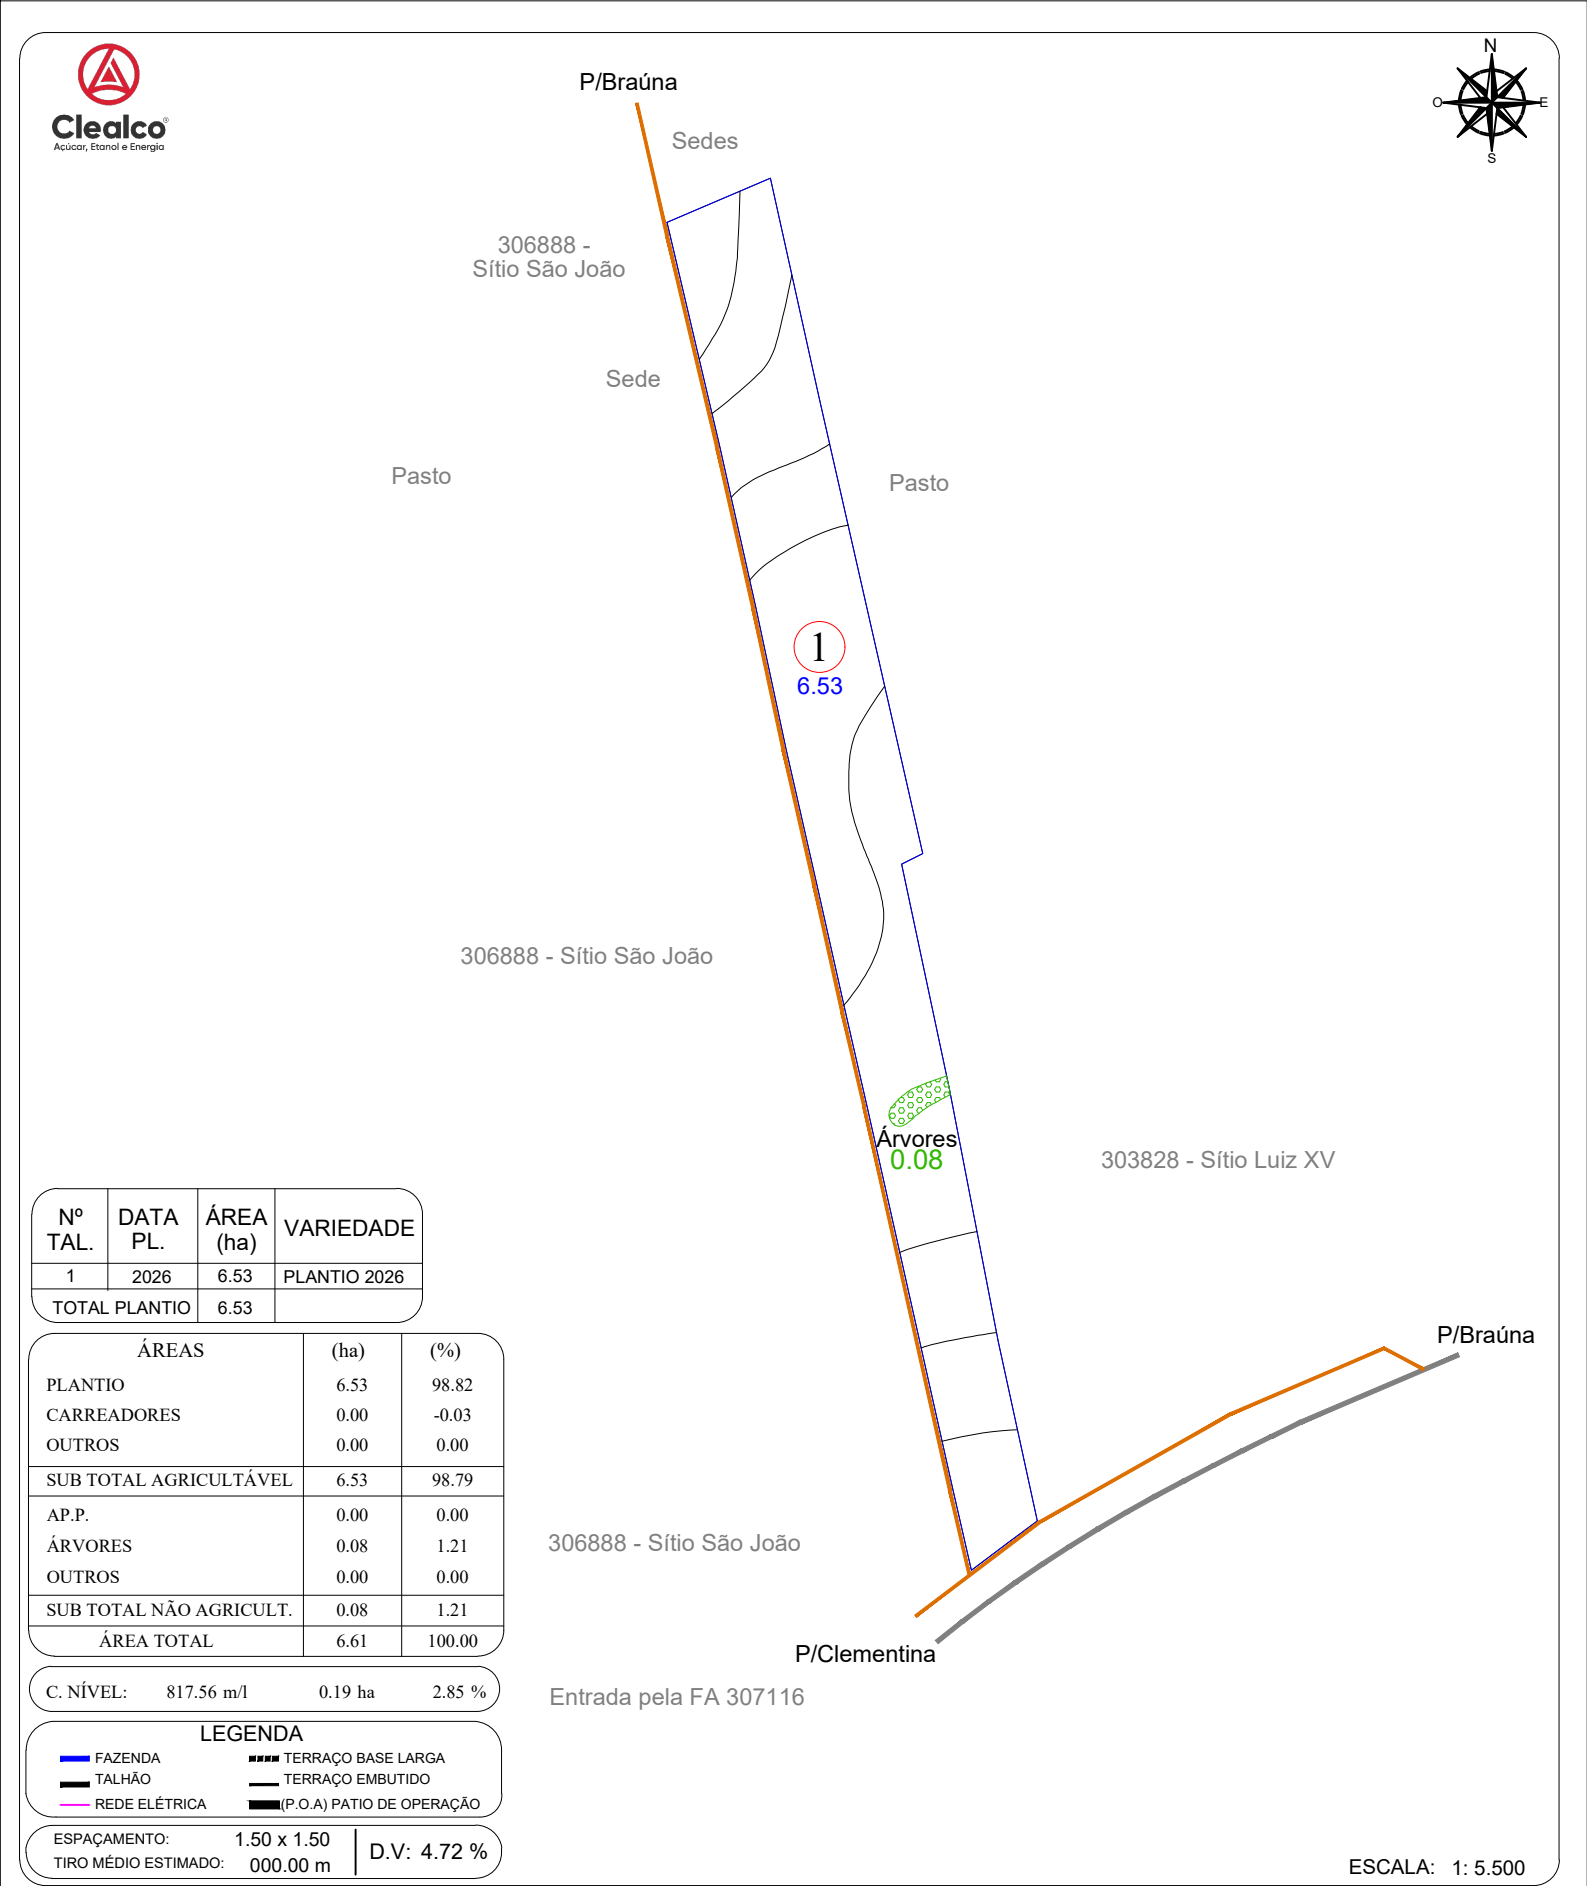


Nº TAL.	DATA PL.	ÁREA (ha)	VARIEDADE
1	2026	6.53	PLANTIO 2026
TOTAL PLANTIO		6.53	

ÁREAS	(ha)	(%)
PLANTIO	6.53	98.82
CARREADORES	0.00	-0.03
OUTROS	0.00	0.00
SUB TOTAL AGRICULTÁVEL	6.53	98.79
AP.P.	0.00	0.00
ÁRVORES	0.08	1.21
OUTROS	0.00	0.00
SUB TOTAL NÃO AGRICULT.	0.08	1.21
ÁREA TOTAL	6.61	100.00

C. NÍVEL: 817.56 m/l 0.19 ha 2.85 %


LEGENDA

- FAZENDA
- TALHÃO
- REDE ELÉTRICA
- TERRAÇO BASE LARGA
- TERRAÇO EMBUTIDO
- (P.O.A) PATIO DE OPERAÇÃO

ESPAÇAMENTO: 1.50 x 1.50
TIRO MÉDIO ESTIMADO: 000.00 m
D.V: 4.72 %

ESCALA: 1: 5.500

CROQUI DE ACESSO

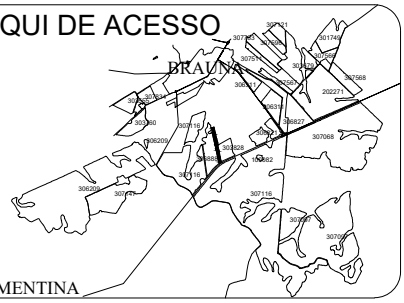

SÍTIO SÃO JOSÉ

PROPRIETÁRIO: GIVANILDO LUIZ FERREIRA
COMPRADOR: CLEALCO
MUNICÍPIO: BRAÚNA - SP

DISTÂNCIAS (km):
UNID. I - Asfalto: 16.00 Terra.: 0.50
UNID.I I - Asfalto: 40.00 Terra.: 0.50

COORDENADAS: E(X): 570829.03 N(Y): 7620053.38
LAT: -21°31'15.0025" LONG: -50°18'57.9470"

CLEALCO - AÇÚCAR E ALCOOL S/A - DEPARTAMENTO DE GEOTECNOLOGIA

LEVANTAMENTO VIA:
SATÉLITE
GPS / VANT
GOOGLE

UNIDADE: I
PARTE: A/A
FUNDO AGRÍCOLA: 308117

M:\01-Mapa de safra\Mapas Atualizados\Terceiro\308117 - Sitio São José (Givanildo Luiz ferreira)\308117 - Sitio São José (Givanildo Luiz ferreira).dwg

Peterson Santos 25/03/2026