
Clealco
Açúcar, Etanol e Energia

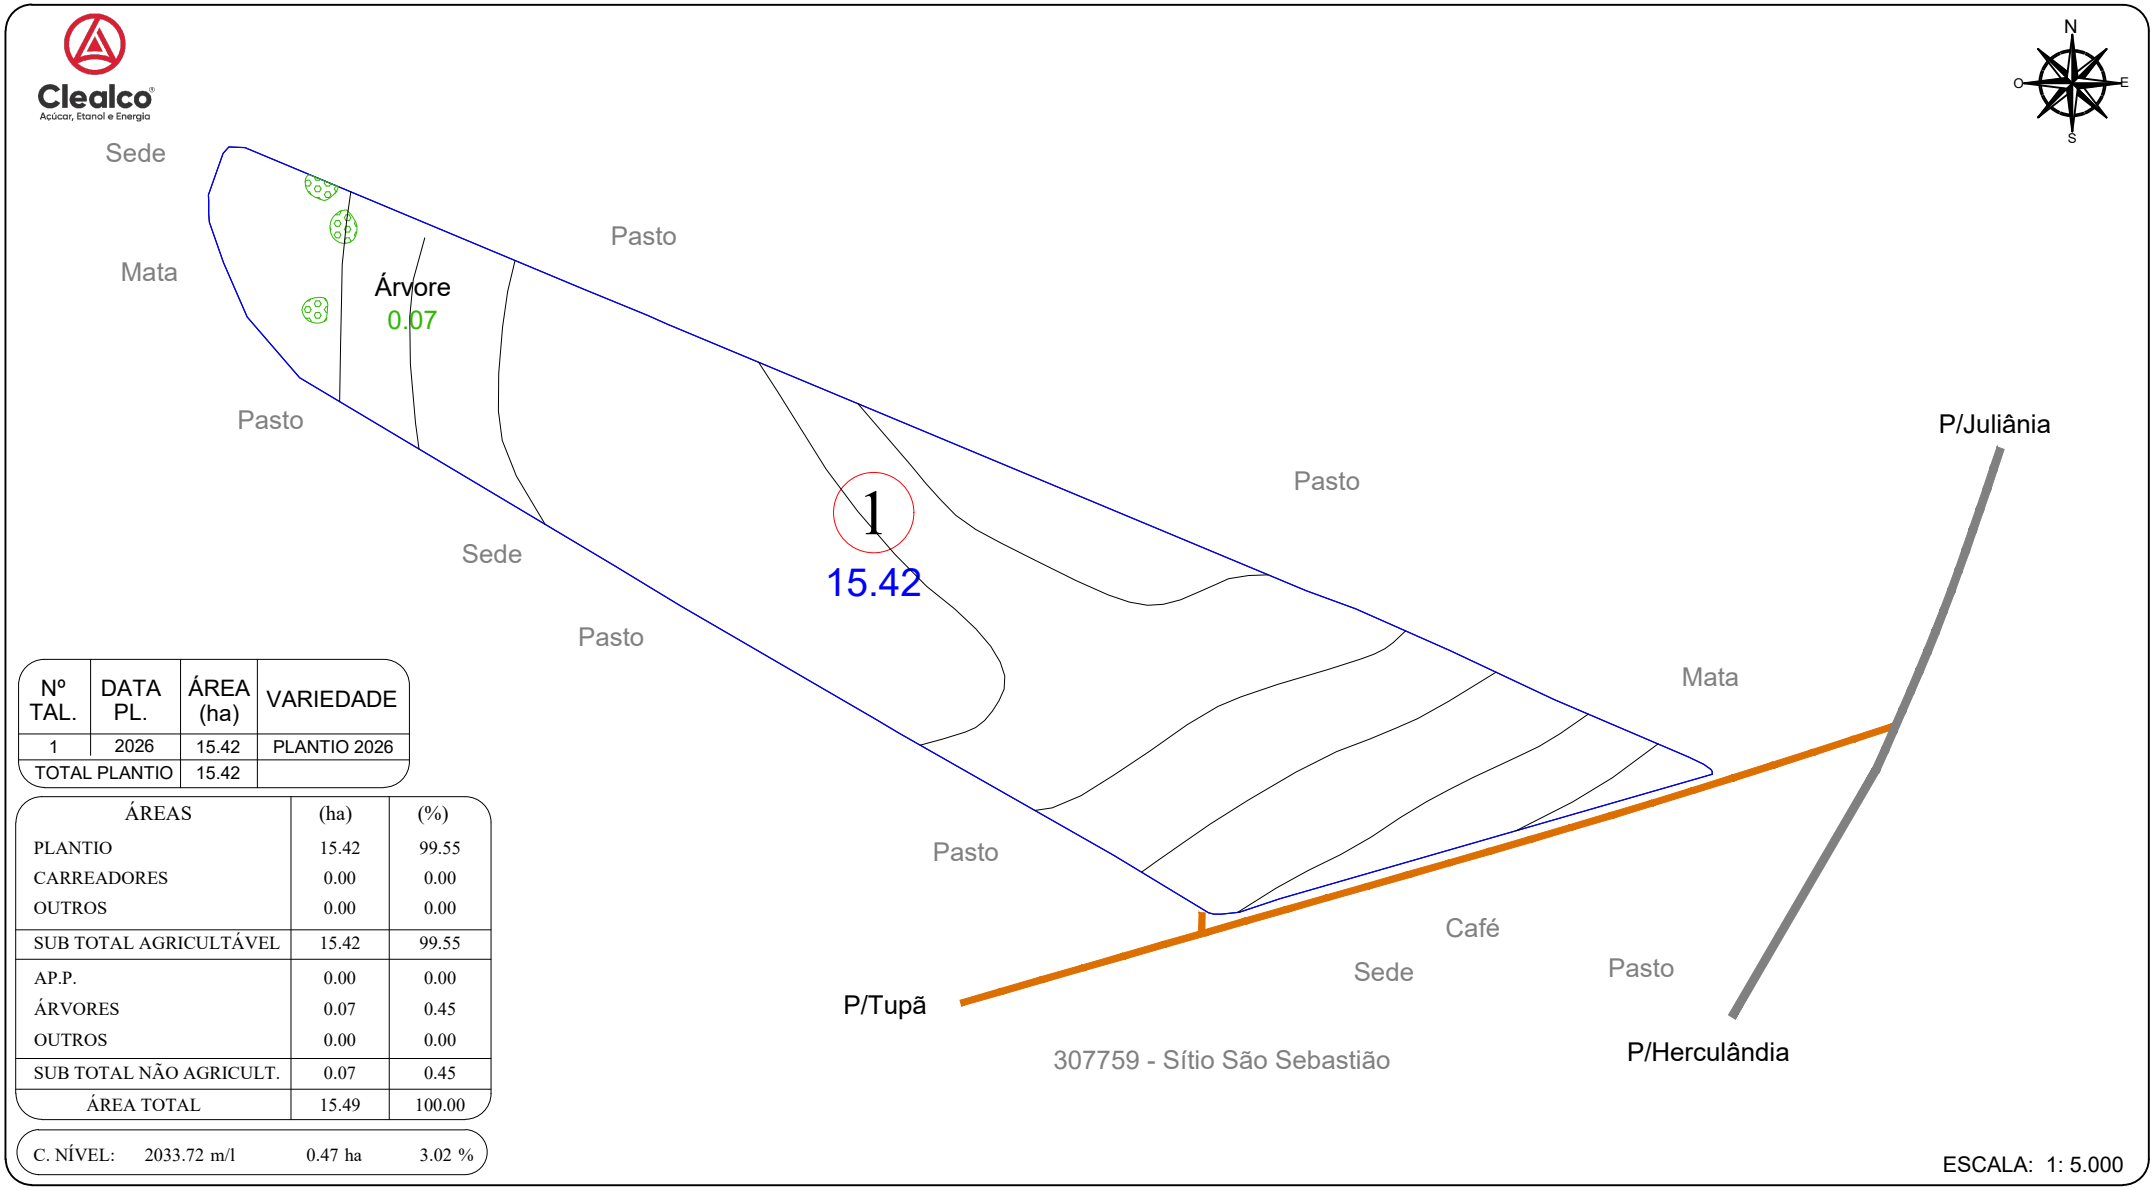

Nº TAL.	DATA PL.	ÁREA (ha)	VARIEDADE
1	2026	15.42	PLANTIO 2026
TOTAL PLANTIO		15.42	

ÁREAS	(ha)	(%)
PLANTIO	15.42	99.55
CARREADORES	0.00	0.00
OUTROS	0.00	0.00
SUB TOTAL AGRICULTÁVEL	15.42	99.55
AP.P.	0.00	0.00
ÁRVORES	0.07	0.45
OUTROS	0.00	0.00
SUB TOTAL NÃO AGRICULT.	0.07	0.45
ÁREA TOTAL	15.49	100.00


C. NÍVEL: 2033.72 m/l 0.47 ha 3.02 %

ESCALA: 1: 5.000

LEGENDA
- FAZENDA
- TALHÃO
- REDE ELÉTRICA
- TERRAÇO BASE LARGA
- TERRAÇO EMBUTIDO

ESPAÇAMENTO: 1.50 x 1.50
TIRO MÉDIO ESTIMADO: 000.00 m
D.V: 4.13 %

CROQUI DE ACESSO

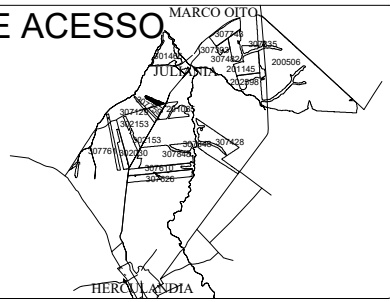

SÍTIO SÃO PEDRO

PROPRIETÁRIO: REGINALDO VIANA RODRIGUES
COMPRADOR: CLEALCO
MUNICÍPIO: HERCULÂNDIA - SP

DISTÂNCIAS (km):
UNID. I - Asfalto: 41.00 Terra.: 23.50
UNID.I I - Asfalto: 25.00 Terra.: 1.00

COORDENADAS: E(X): 563872.83 N(Y): 7576456.21
LAT: -21°54'53.8841" LONG: -50°22'53.6841"
CLEALCO - AÇÚCAR E ALCOOL S/A - DEPARTAMENTO DE GEOTECNOLOGIA

LEVANTAMENTO VIA:
SATÉLITE
GPS / VANT
GOOGLE

UNIDADE: II
PARTE: A/A
FUNDO AGRÍCOLA: 308127

M:\01-Mapa de safra\Mapas Atualizados\Terceiro\308127 - Sítio São Pedro (Reginaldo Viana Rodrigues)\308127 - Sítio São Pedro (Reginaldo Viana Rodrigues).dwg

Bruno Gamboa 10/10/25