
Clealco
Açúcar, Etanol e Energia

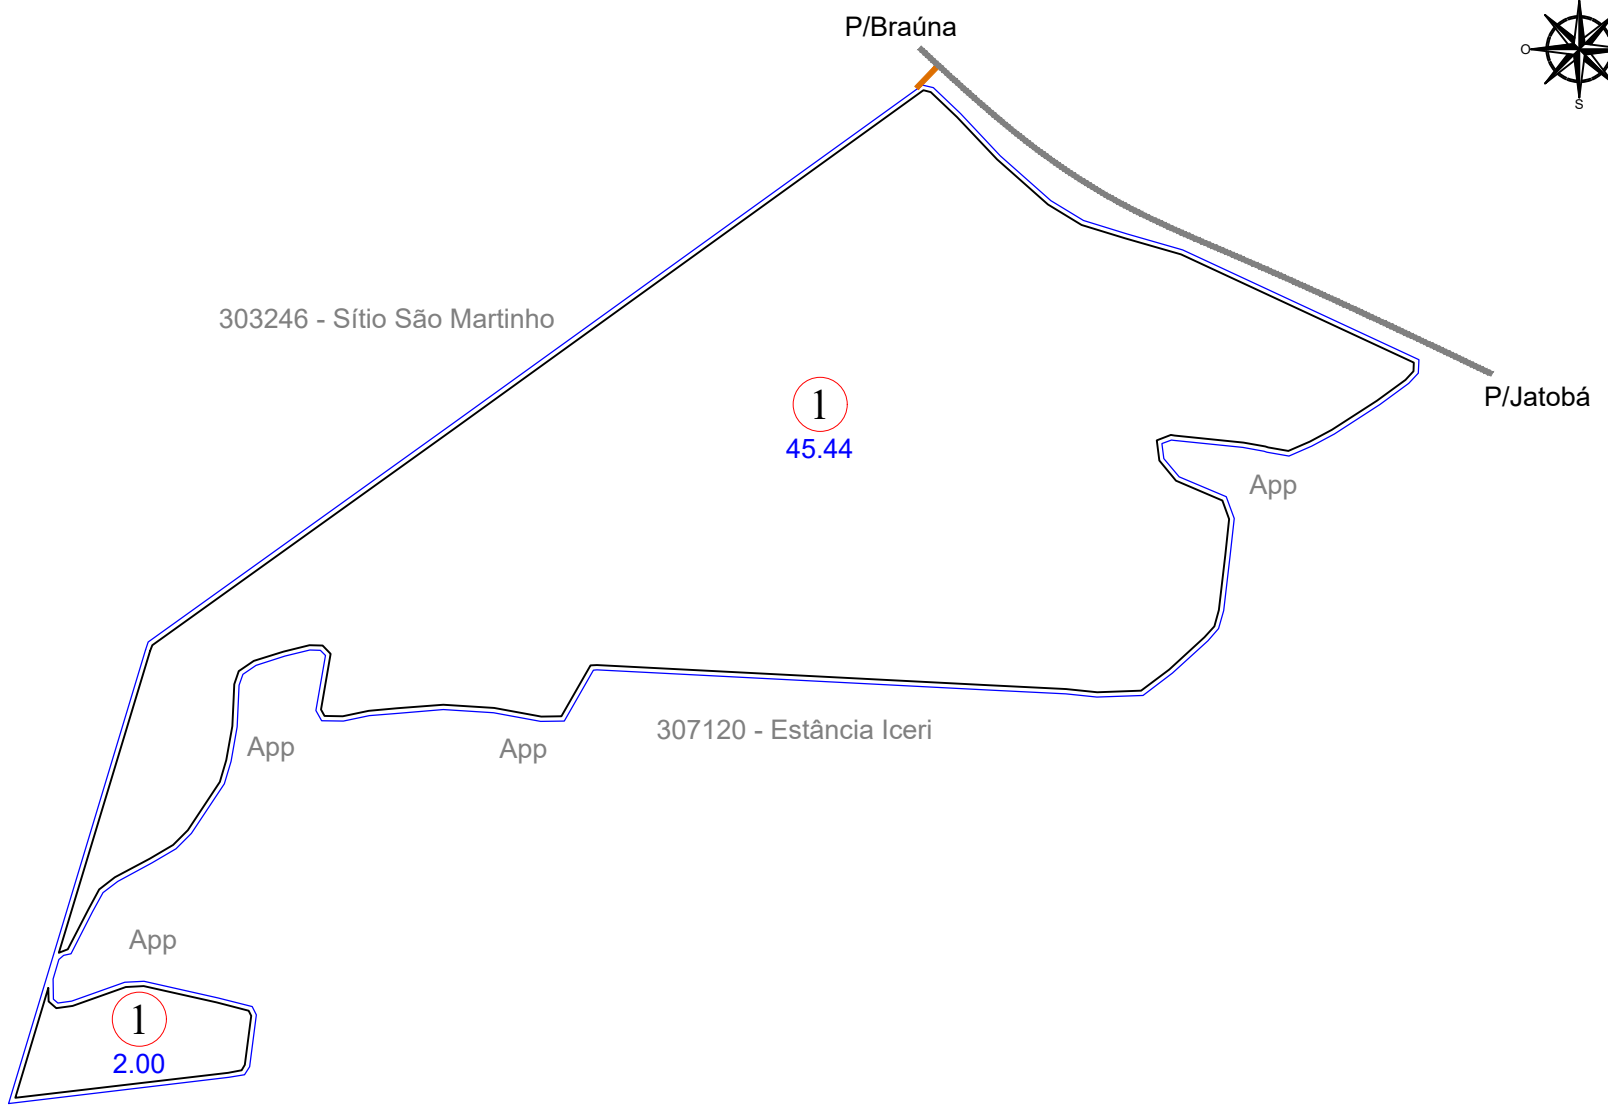

Nº TAL.	DATA PL.	ÁREA (ha)	VARIEDADE
1	04/2025	47.44	RB07 5322
TOTAL PLANTIO		47.44	

ÁREAS	(ha)	(%)
PLANTIO	47.44	95.31
CARREADORES	2.34	4.69
OUTROS	0.00	0.00
SUB TOTAL AGRICULTÁVEL	49.78	100.00
AP.P.	0.00	0.00
ÁRVORES	0.00	0.00
OUTROS	0.00	0.00
SUB TOTAL NÃO AGRICULT.	0.00	0.00
ÁREA TOTAL	49.78	100.00

C. NÍVEL: 0.00 m/l 0.00 ha 0.00 %


ESCALA: 1: 8.000

LEGENDA

- FAZENDA
- TALHÃO
- REDE ELÉTRICA
- TERRAÇO BASE LARGA
- TERRAÇO EMBUTIDO

ESPAÇAMENTO: 1.50 x 1.50
TIRO MÉDIO ESTIMADO: 000.00 m
D.V: 0.00 %

CROQUI DE ACESSO

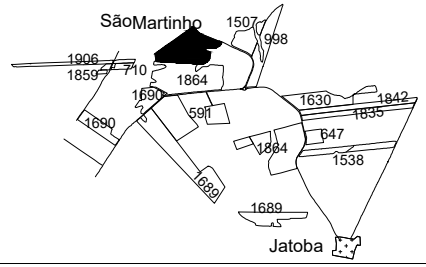

SÍTIO DOIS IRMÃOS

PROPRIETÁRIO: WILLIAN AVILA
COMPRADOR: CLEALCO
MUNICÍPIO: ALTO ALEGRE - SP

DISTÂNCIAS (km):
UNID. I - Asfalto: 32.50 Terra.: 0.00
UNID.I I - Asfalto: 40.00 Terra.: 0.00

COORDENADAS: E(X): 575541.24 N(Y): 7611769.80
LAT: -21°35'43.7203" LONG: -50°16'12.8104"

CLEALCO - AÇÚCAR E ALCOOL S/A - DEPARTAMENTO DE GEOTECNOLOGIA

LEVANTAMENTO VIA:
SATÉLITE
GPS / VANT
GOOGLE

UNIDADE: I
PARTE: A/A
FUNDO AGRÍCOLA: 308145

M:\01-Mapa de safra\Mapas Atualizados\Terceiro\308145 - Sítio Dois Irmãos (Willian Avila Pereira e Outro)\308145 - Sítio Dois Irmãos (Willian Avila Pereira e Outro).dwg

Bruno Gamboa 03/03/26