
Clealco
Açúcar, Etanol e Energia

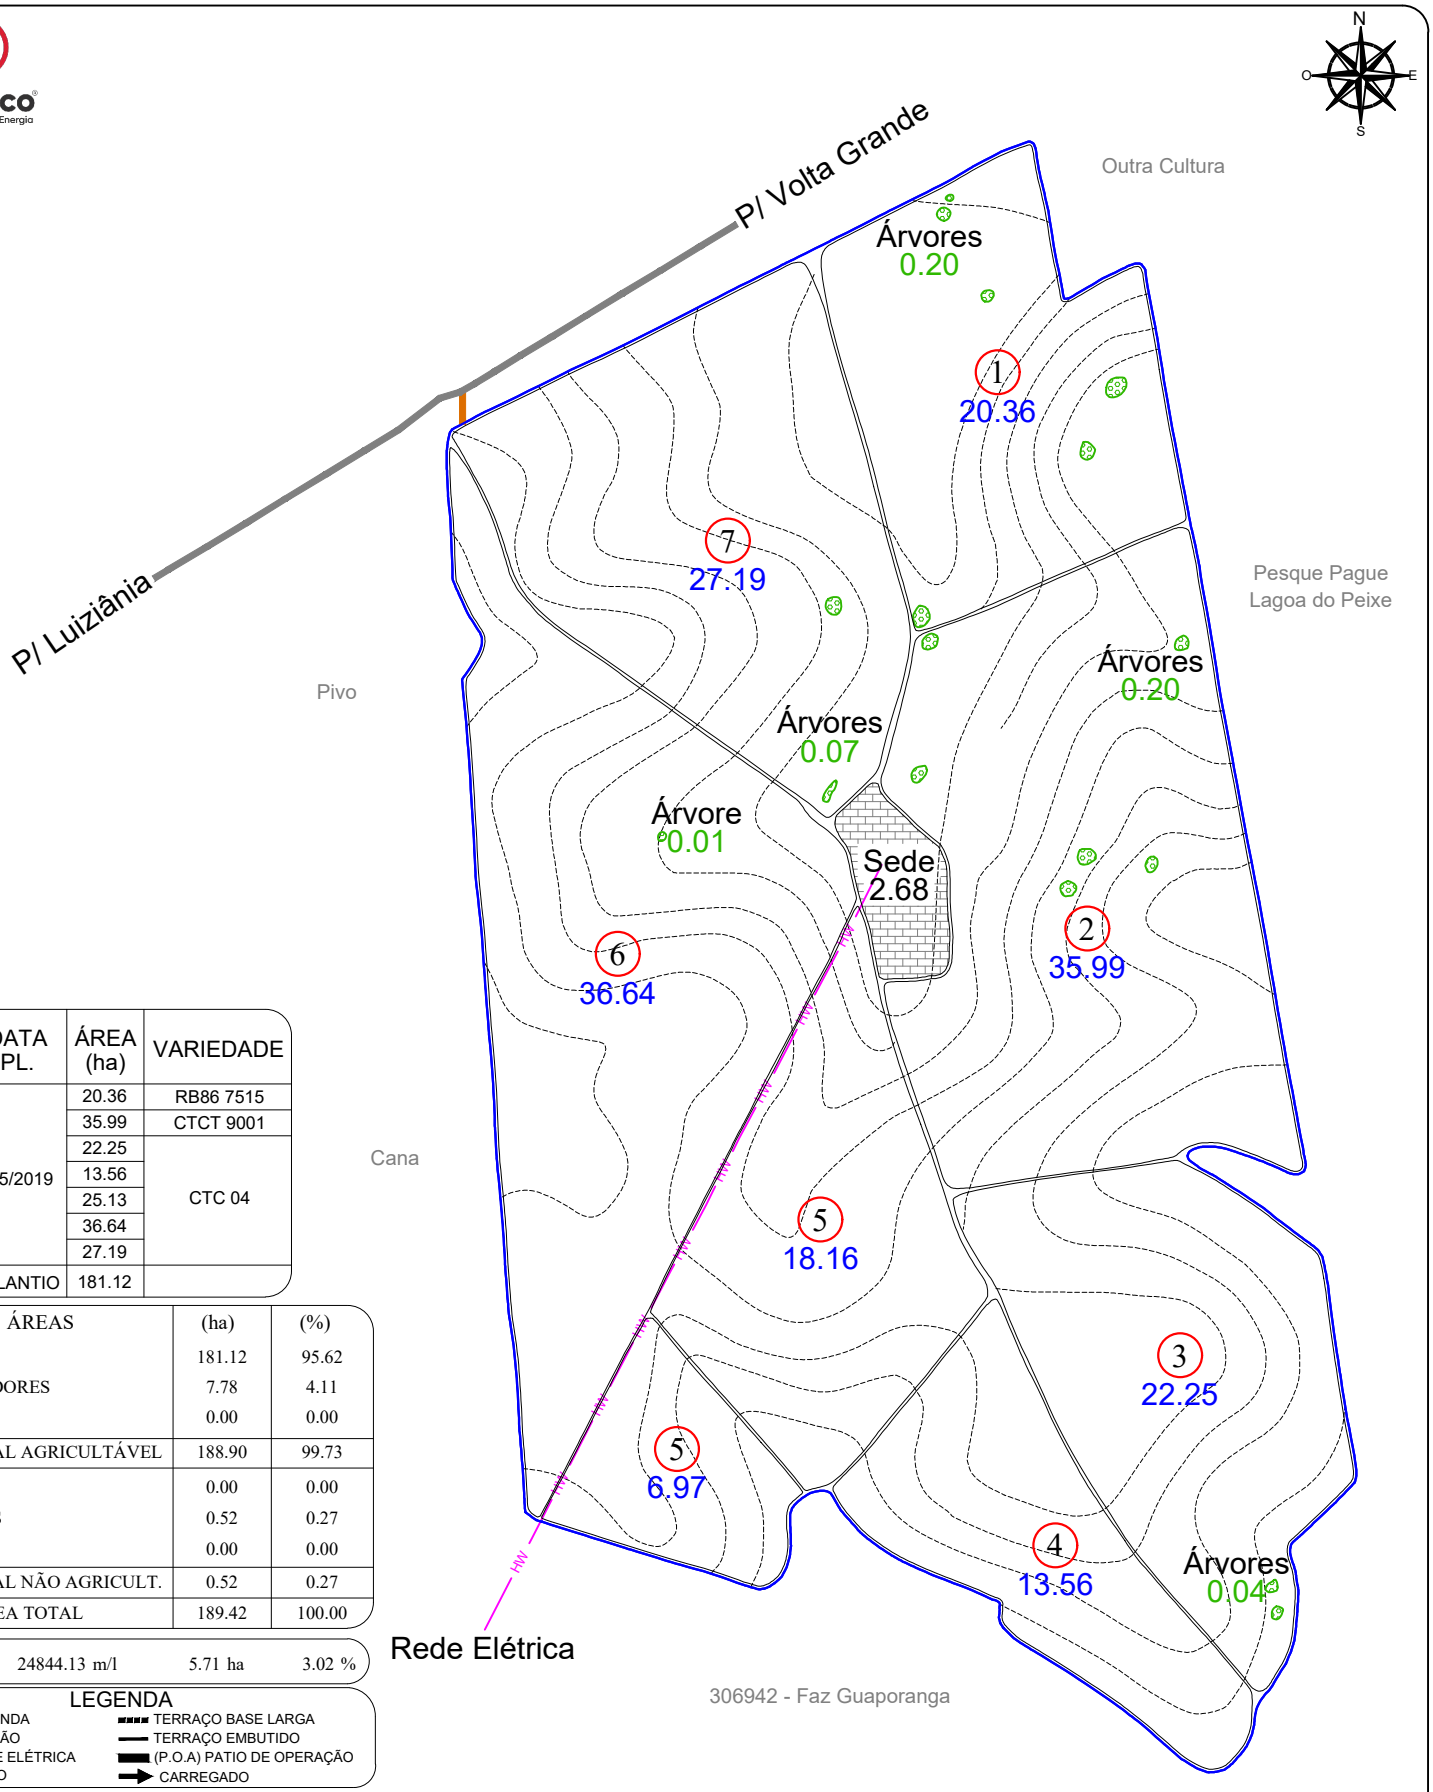

Nº TAL.	DATA PL.	ÁREA (ha)	VARIEDADE
1	05/2019	20.36	RB86 7515
2		35.99	CTCT 9001
3		22.25	CTC 04
4		13.56	
5		25.13	
6		36.64	
7		27.19	
TOTAL PLANTIO		181.12	

ÁREAS	(ha)	(%)
PLANTIO	181.12	95.62
CARREADORES	7.78	4.11
OUTROS	0.00	0.00
SUB TOTAL AGRICULTÁVEL	188.90	99.73
AP.P.	0.00	0.00
ÁRVORES	0.52	0.27
OUTROS	0.00	0.00
SUB TOTAL NÃO AGRICULT.	0.52	0.27
ÁREA TOTAL	189.42	100.00

C. NÍVEL: 24844.13 m/l 5.71 ha 3.02 %


LEGENDA

- FAZENDA
- TALHÃO
- REDE ELÉTRICA
- VAZIO
- TERRAÇO BASE LARGA
- TERRAÇO EMBUTIDO
- (P.O.A) PATIO DE OPERAÇÃO
- CARREGADO

ESPAÇAMENTO: 1.50 x 1.50
TIRO MÉDIO ESTIMADO: 000.00 m
D.V: 4.74 %

ESCALA: 1: 10.500

CROQUI DE ACESSO

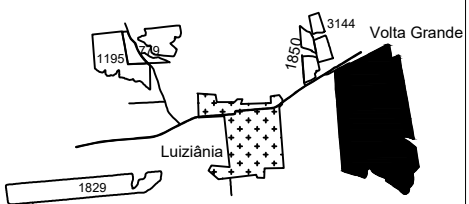

FAZENDA REALEZA

PROPRIETÁRIO: WILLIAN ÁVILA PEREIRA
COMPRADOR: CLEALCO
MUNICÍPIO: LUIZIÂNIA - SP

DISTÂNCIAS (km):
UNID. I - Asfalto: 34.00 Terra.: 0.80
UNID.I I - Asfalto: 25.70 Terra.: 1.40

COORDENADAS: E(X): 571392.77 N(Y): 7603015.08
LAT: -21°40'29.0699" LONG: -50°18'35.7265"

CLEALCO - AÇÚCAR E ALCOOL S/A - DEPARTAMENTO DE GEOTECNOLOGIA

LEVANTAMENTO VIA:
- SATÉLITE
- GPS / VANT
- GOOGLE

UNIDADE: I
PARTE: A/A
FUNDO AGRÍCOLA: 308147

M:\01-Mapa de safra\Mapas Atualizados\Terceiro\308147 - Fazenda Realeza (Willian Avila Pereira)\308147 - Fazenda Realeza (Willian Avila Pereira).dwg

Peterson Santos 05/05/2026