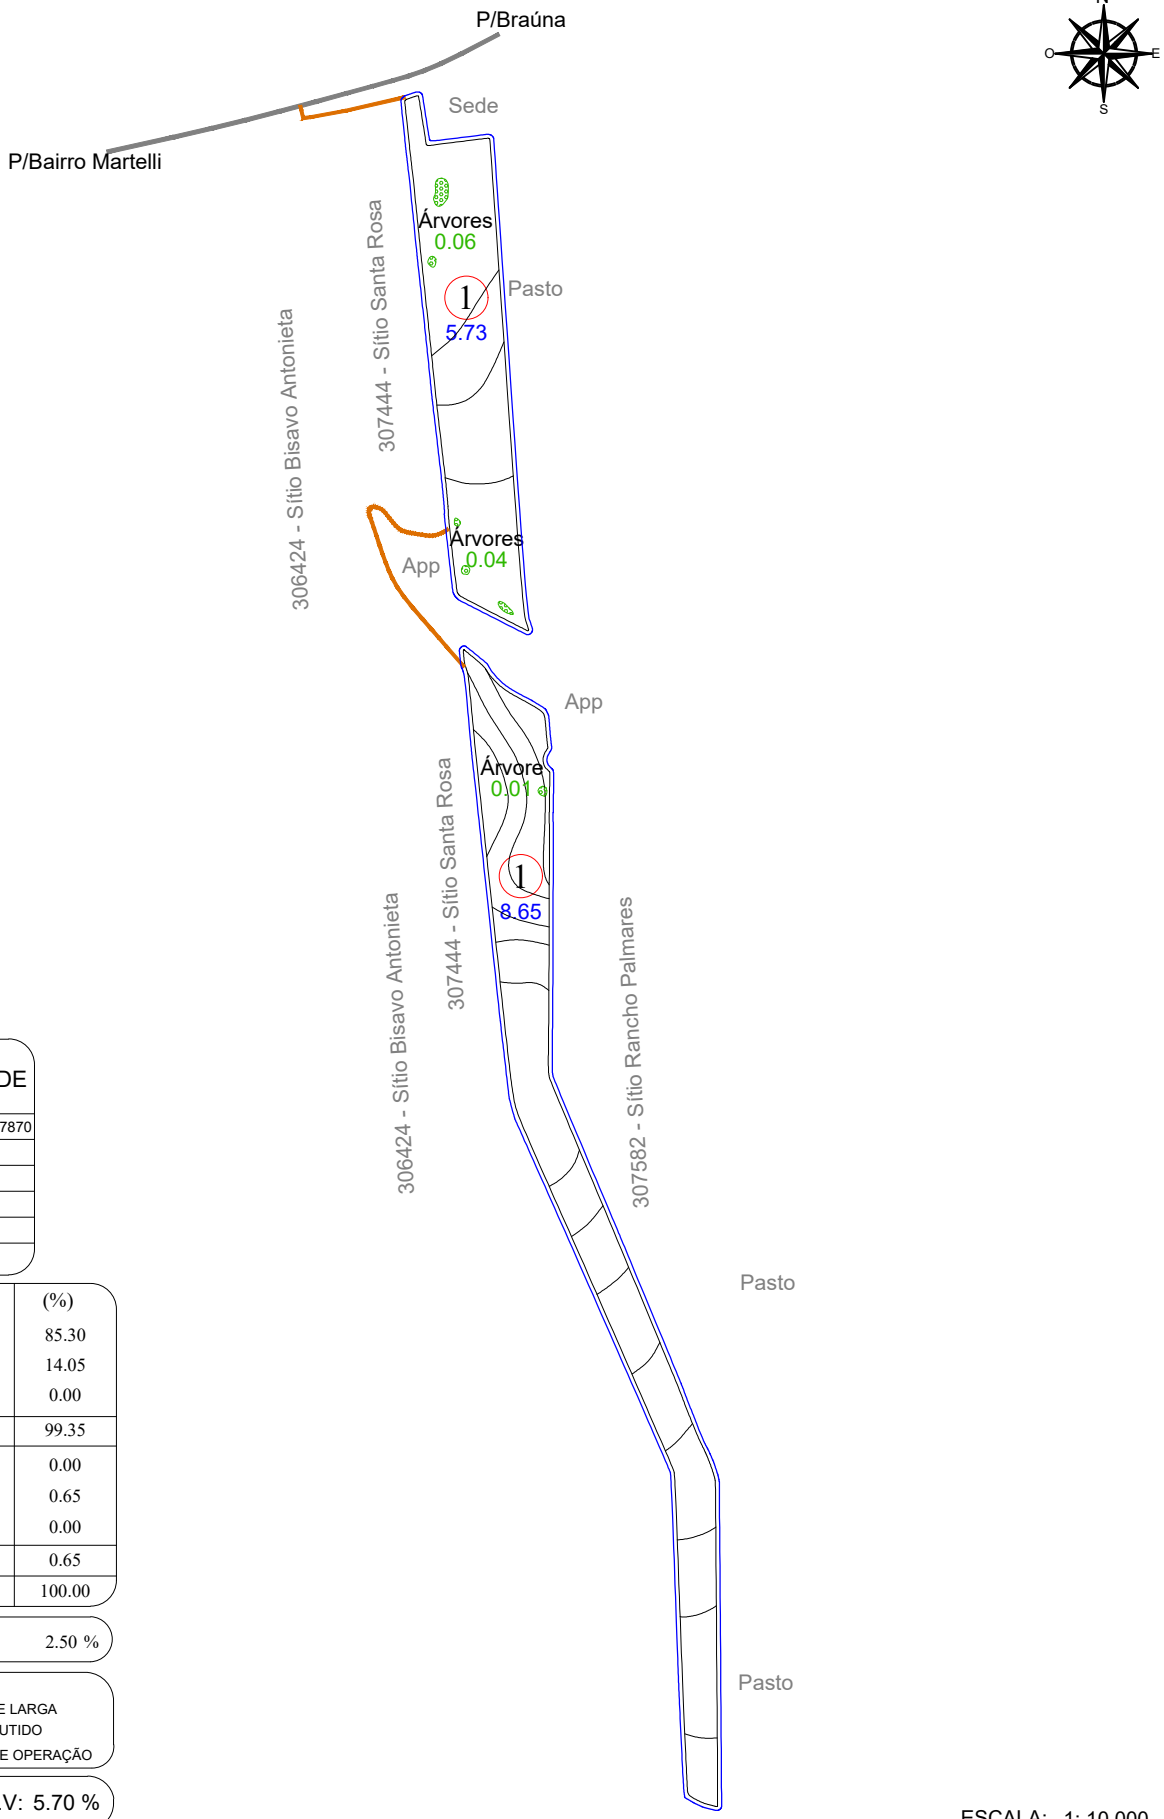


Nº TAL.	DATA PL.	ÁREA (ha)	VARIEDADE
1	05/2025	14.38	RB 075322 / CV 7870
TOTAL PLANTIO		14.38	

ÁREAS	(ha)	(%)
PLANTIO	14.38	85.30
CARREADORES	2.37	14.05
OUTROS	0.00	0.00
SUB TOTAL AGRICULTÁVEL	16.75	99.35
AP.P.	0.00	0.00
ÁRVORES	0.11	0.65
OUTROS	0.00	0.00
SUB TOTAL NÃO AGRICULT.	0.11	0.65
ÁREA TOTAL	16.86	100.00

C. NÍVEL: 1835.08 m/l 0.42 ha 2.50 %


LEGENDA

- FAZENDA
- TALHÃO
- REDE ELÉTRICA
- TERRAÇO BASE LARGA
- TERRAÇO EMBUTIDO
- (P.O.A) PATIO DE OPERAÇÃO

ESPAÇAMENTO: 1.50 x 1.50
TIRO MÉDIO ESTIMADO: 74.81 m
D.V: 5.70 %

ESCALA: 1: 10.000

CROQUI DE ACESSO

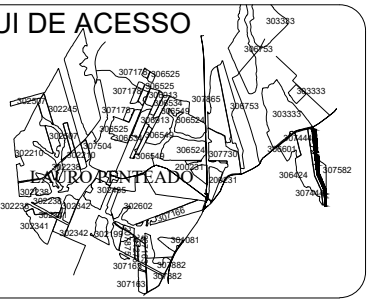

SÍTIO SÃO JOÃO I

PROPRIETÁRIO: PAULO BENTO BOGO
COMPRADOR: CLEALCO
MUNICÍPIO: CLEMENTINA - SP

DISTÂNCIAS (km):
UNID. I - Asfalto: 19.10 Terra.: 1.50
UNID.I I - Asfalto: 69.50 Terra.: 1.50

COORDENADAS: E(X): 562317.84 N(Y): 7620786.55
LAT: -21°30'52.2960" LONG: -50°23'53.8855"

CLEALCO - AÇÚCAR E ALCOOL S/A - DEPARTAMENTO DE GEOTECNOLOGIA

LEVANTAMENTO VIA:
SATÉLITE
GPS / VANT
GOOGLE

UNIDADE: I
PARTE: A/A
FUNDO AGRÍCOLA: 308153

M:\01-Mapa de safra\Mapas Atualizados\Terceiro\308153 - Sítio São João I (Paulo Bento Bogo)\308153 - Sítio São João I (Paulo Bento Bogo).dwg

Peterson Santos 12/05/2026