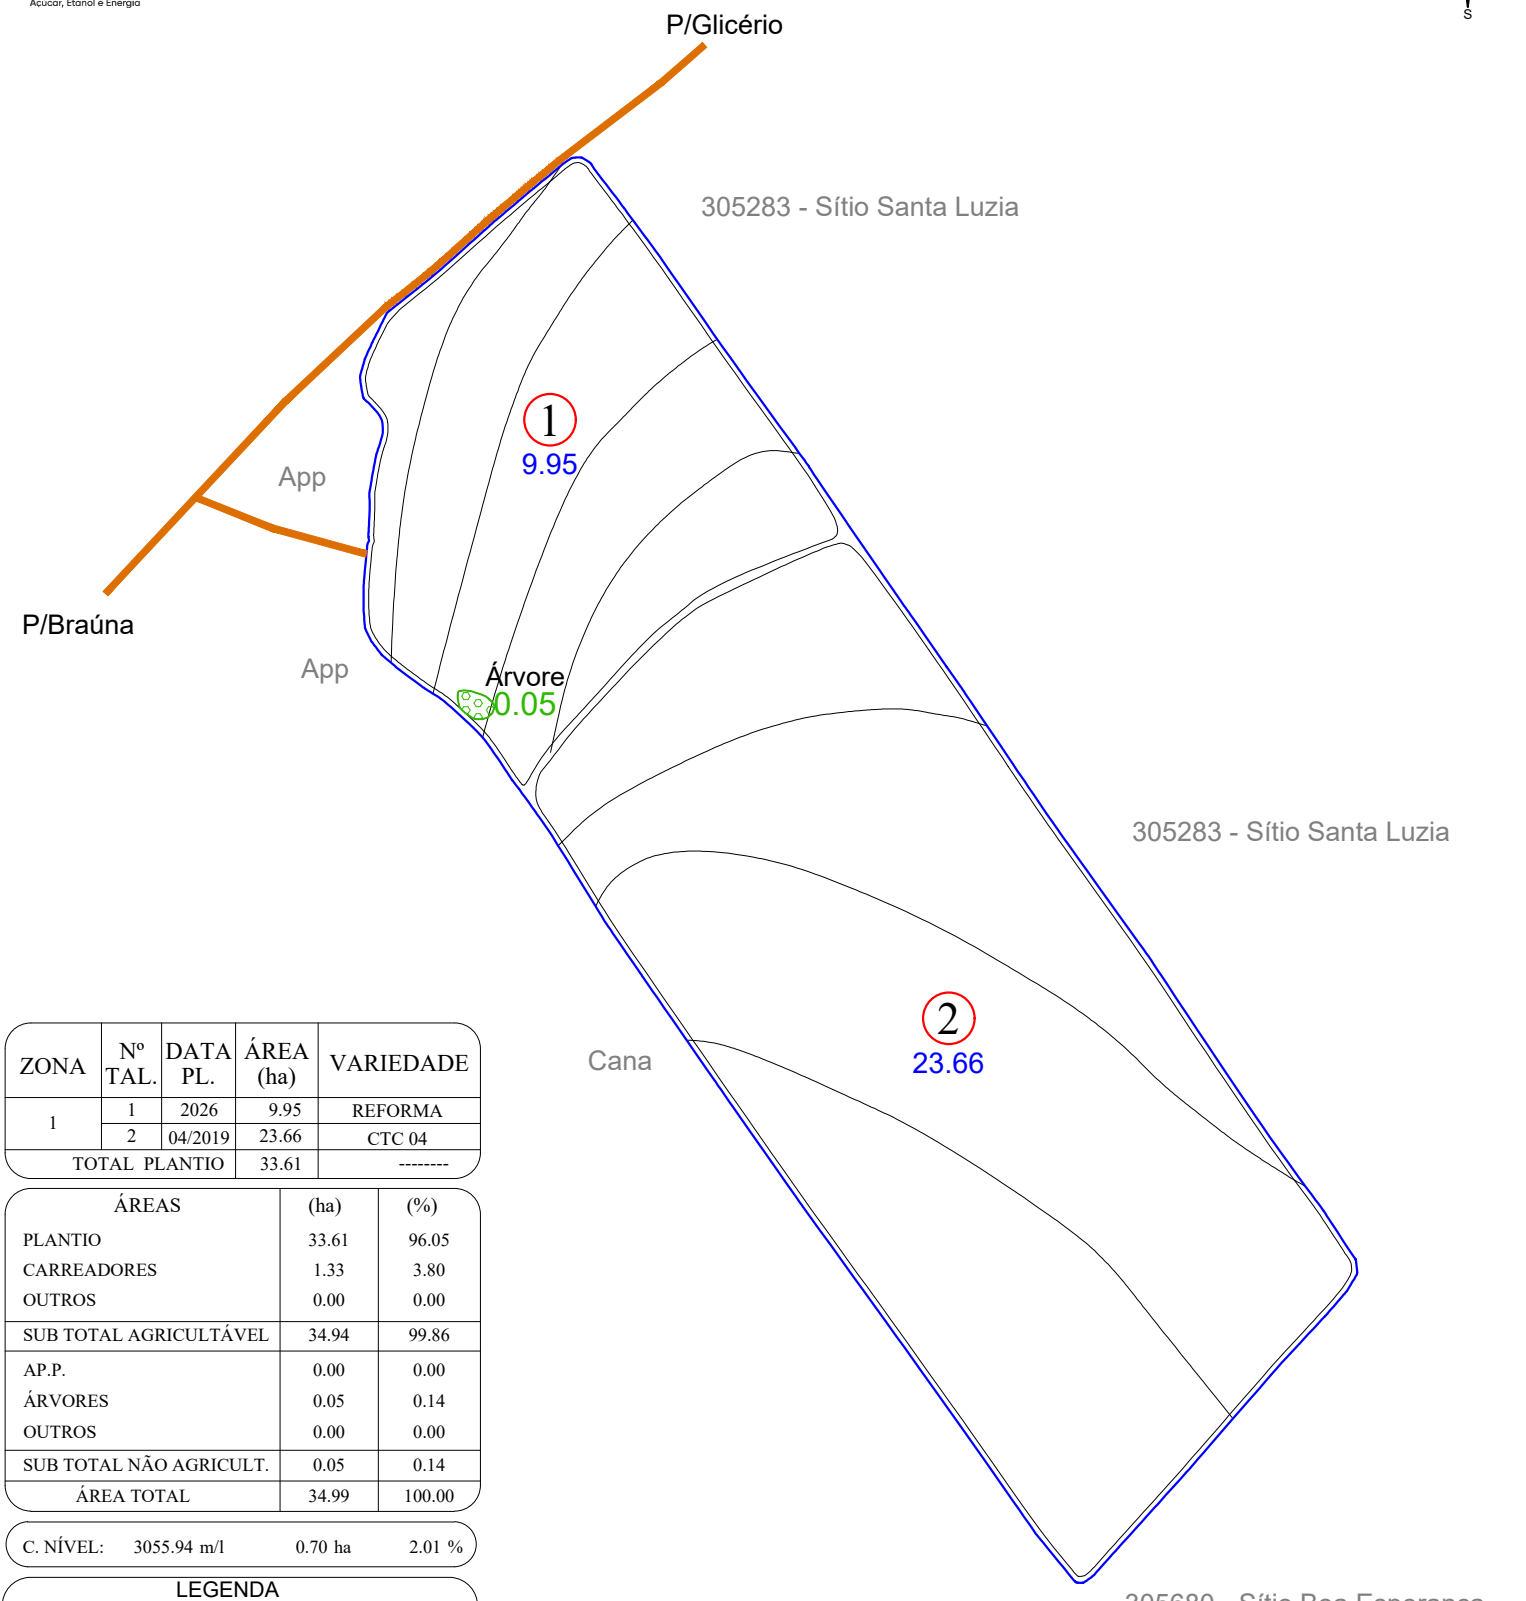



| ZONA | Nº TAL. | DATA PL. | ÁREA (ha) | VARIEDADE |
|---|---|---|---|---|
| 1 | 1 | 2026 | 9.95 | REFORMA |
| | 2 | 04/2019 | 23.66 | CTC 04 |
| TOTAL PLANTIO | | | 33.61 | -------- |

| ÁREAS | (ha) | (%) |
|---|---|---|
| PLANTIO | 33.61 | 96.05 |
| CARREADORES | 1.33 | 3.80 |
| OUTROS | 0.00 | 0.00 |
| SUB TOTAL AGRICULTÁVEL | 34.94 | 99.86 |
| AP.P. | 0.00 | 0.00 |
| ÁRVORES | 0.05 | 0.14 |
| OUTROS | 0.00 | 0.00 |
| SUB TOTAL NÃO AGRICULT. | 0.05 | 0.14 |
| ÁREA TOTAL | 34.99 | 100.00 |

C. NÍVEL: 3055.94 m/l 0.70 ha 2.01 %


LEGENDA

- FAZENDA
- TALHÃO
- REDE ELÉTRICA
- TERRAÇO BASE LARGA
- TERRAÇO EMBUTIDO
- (P.O.A) PATIO DE OPERAÇÃO

ESPAÇAMENTO: 1.50 x 1.50
TIRO MÉDIO ESTIMADO: 304.38 m
D.V: 3.44%

ESCALA: 1: 6.000

## CROQUI DE ACESSO

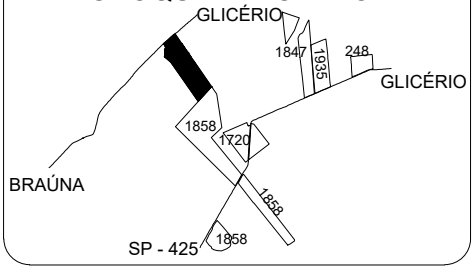


# SÍTIO SÃO JOSÉ

PROPRIETÁRIO: MILENE GARBELINI
COMPRADOR: CLEALCO
MUNICÍPIO: GLICÉRIO - SP

DISTÂNCIAS (km):
UNID. I - Asfalto: 18.50 Terra.: 10.00
UNID.I I - Asfalto: 45.00 Terra.: 10.00

COORDENADAS: E(X): 576175.26 N(Y): 7628283.41
LAT: -21°26'46.5407" LONG: -50°15'53.4650"

CLEALCO - AÇÚCAR E ALCOOL S/A - DEPARTAMENTO DE GEOTECNOLOGIA

LEVANTAMENTO VIA:
- SATÉLITE
- GPS / VANT
- GOOGLE

UNIDADE: I
PARTE: A/A
FUNDO AGRÍCOLA: 308167

M:\01-Mapa de safra\Mapas Atualizados\Terceiro\308167 - Sítio São José (Milene Garbelini)\308167 - Sítio São José (Milene Garbelini).dwg

Bruno Gamboa 25/02/26