
Clealco
Açúcar, Etanol e Energia

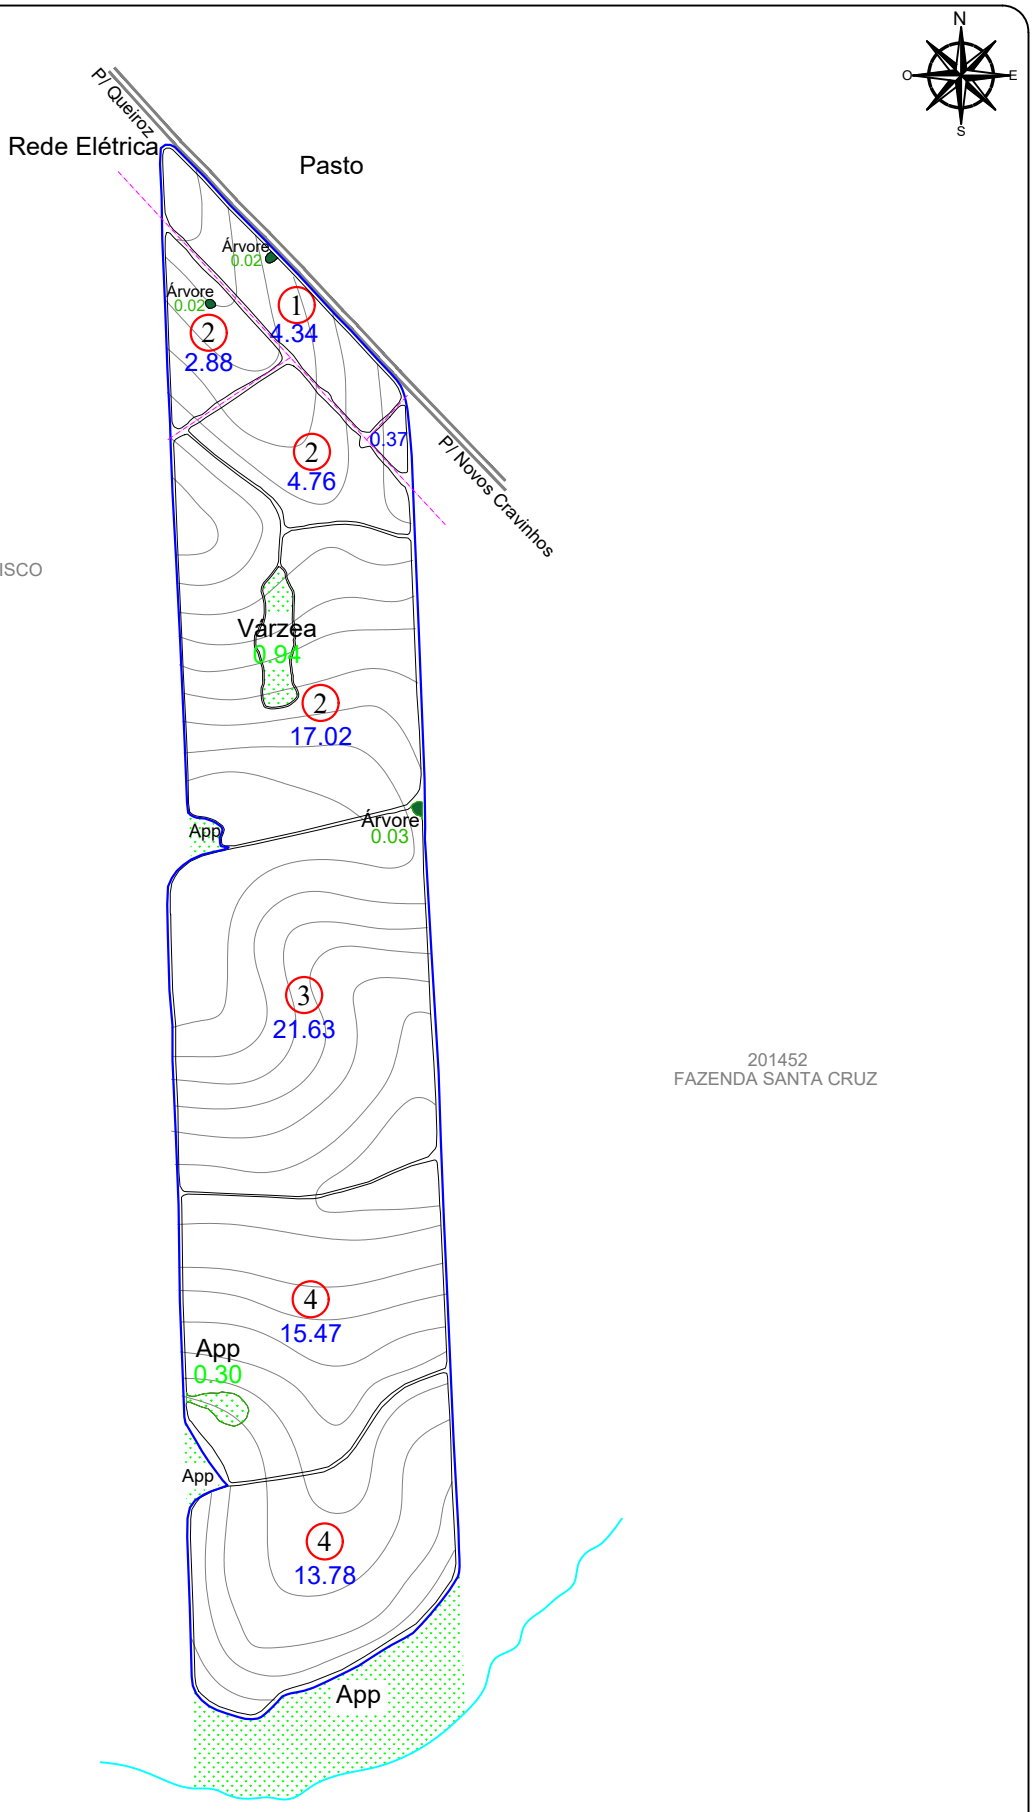

Nº TAL.	DATA PL.	ÁREA (ha)	VARIEDADE
1	06/2023	4.71	RB 975242
2		24.66	
3		21.63	
4		29.25	
TOTAL PLANTIO		80.25	

ÁREAS	(ha)	(%)
PLANTIO	80.25	93.33
CARREADORES	4.43	5.15
OUTROS	0.00	0.00
SUB TOTAL AGRICULTÁVEL	84.68	98.48
AP.P.	1.24	1.44
ÁRVORES	0.07	0.08
OUTROS	0.00	0.00
SUB TOTAL NÃO AGRICULT.	1.31	1.52
ÁREA TOTAL	85.99	100.00

C. NÍVEL: 14727.06 m/l 3.39 ha 3.94 %


LEGENDA

- FAZENDA
- TALHÃO
- REDE ELÉTRICA
- TERRAÇO BASE LARGA
- TERRAÇO EMBUTIDO
- (P.O.A) PATIO DE OPERAÇÃO

ESPAÇAMENTO: 1.50 x 1.50
TIRO MÉDIO ESTIMADO: 000.00 m
D.V: 0.00 %

ESCALA: 1: 12.000

CROQUI DE ACESSO

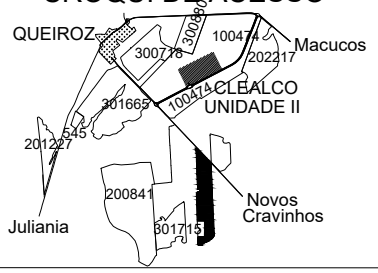

FAZENDA SÃO JORGE

PROPRIETÁRIO: JULIO CESAR R. DE BARROS
COMPRADOR: CLEALCO
MUNICÍPIO: QUEIROZ - SP

DISTÂNCIAS (km):
UNID. I - Asfalto: 62.50 Terra.: 1.00
UNID.I I - Asfalto: 4.00 Terra.: 0.00

COORDENADAS: E(X): 580925.28 N(Y): 7585239.10
LAT: -21°50'5.7156" LONG: -50°13'0.9104"

CLEALCO - AÇÚCAR E ALCOOL S/A - DEPARTAMENTO DE GEOTECNOLOGIA

LEVANTAMENTO VIA:
- SATÉLITE
- GPS / VANT
- GOOGLE

UNIDADE: II
PARTE: A/B
FUNDO AGRÍCOLA: 308175

M:\01-Mapa de safra\Mapas Atualizados\Terceiro\308175 - Fazenda Sao Jorge (Julio Cesar Rios de Barros)\308175 A - Fazenda Sao Jorge (Julio Cesar Rios de Barros).dwg

Benati 18/05/2026