
Clealco
Açúcar, Etanol e Energia

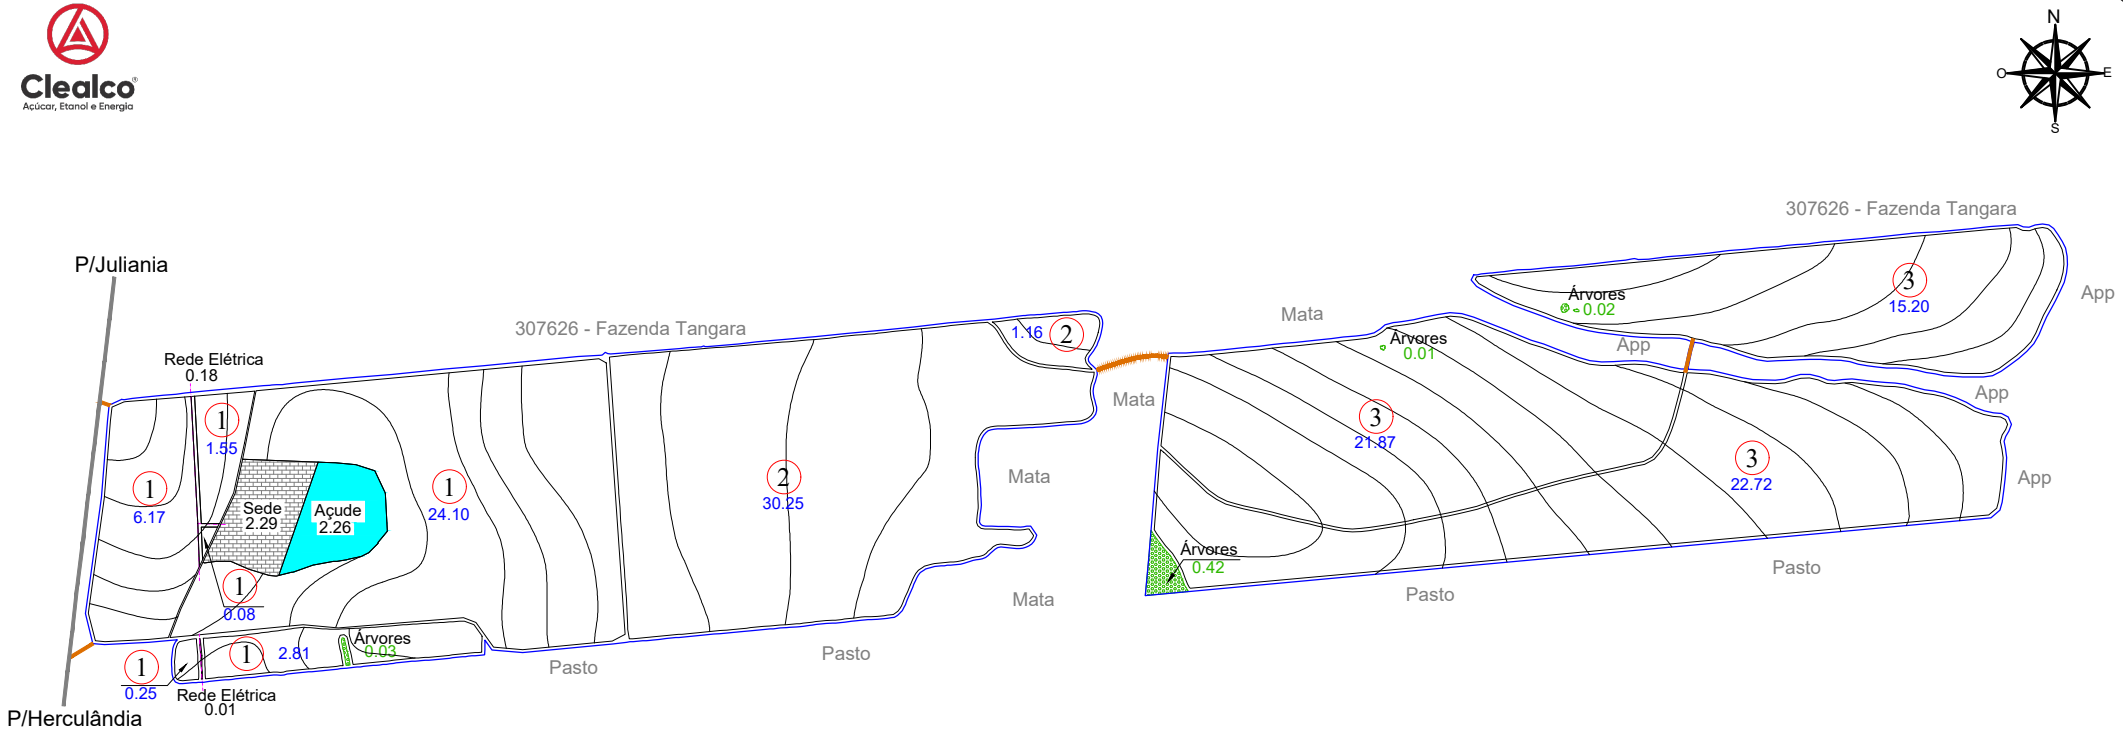

ÁREAS	(ha)	(%)
PLANTIO	126.16	91.29
CARREADORES	6.82	4.93
OUTROS	0.00	0.00
SUB TOTAL AGRICULTÁVEL	132.98	96.22
AP.P.	0.00	0.00
ÁRVORES	0.48	0.35
OUTROS	4.74	3.43
SUB TOTAL NÃO AGRICULT.	5.22	3.78
ÁREA TOTAL	138.20	100.00
C. NÍVEL: 13567.17 m/l	3.12 ha	2.26 %


Nº TAL.	DATA PL.	ÁREA (ha)	VARIEDADE
1	2026	34.96	PLANTIO 2026
2		31.41	
3		59.79	
TOTAL PLANTIO		126.16	

ESCALA: 1: 13.000

LEGENDA
- FAZENDA
- TALHÃO
- REDE ELÉTRICA
- TERRAÇO BASE LARGA
- TERRAÇO EMBUTIDO
- VAZIO
- CARREGADO

ESPAÇAMENTO: 1.50 x 1.50
TIRO MÉDIO ESTIMADO: 244.75 m
D.V: 5.33 %

CROQUI DE ACESSO

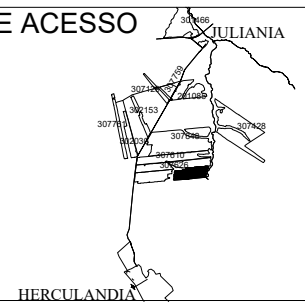

FAZENDA SÃO PEDRO

PROPRIETÁRIO: DAIANE CARLA GILBERTO
COMPRADOR: CLEALCO
MUNICÍPIO: HERCULÂNDIA - SP

DISTÂNCIAS (km):
UNID. I - Asfalto: 81.70 Terra.: 3.50
UNID.I I - Asfalto: 28.50 Terra.: 3.50

COORDENADAS: E(X): 564955.94 N(Y): 7572155.10
LAT: -21°57'13.6247" LONG: -50°22'15.3188"
CLEALCO - AÇÚCAR E ALCOOL S/A - DEPARTAMENTO DE GEOTECNOLOGIA

LEVANTAMENTO VIA:
SATÉLITE
GPS / VANT
GOOGLE

UNIDADE: II
PARTE: A/A
FUNDO AGRÍCOLA: 308180

M:\01-Mapa de safra\Mapas Atualizados\Terceiro\308180 - Fazenda São Pedro (Daiane Carla Gilberto)\308180 - Fazenda São Pedro (Daiane Carla Gilberto).dwg

Peterson Santos 23/10/26