
Clealco
Açúcar, Etanol e Energia

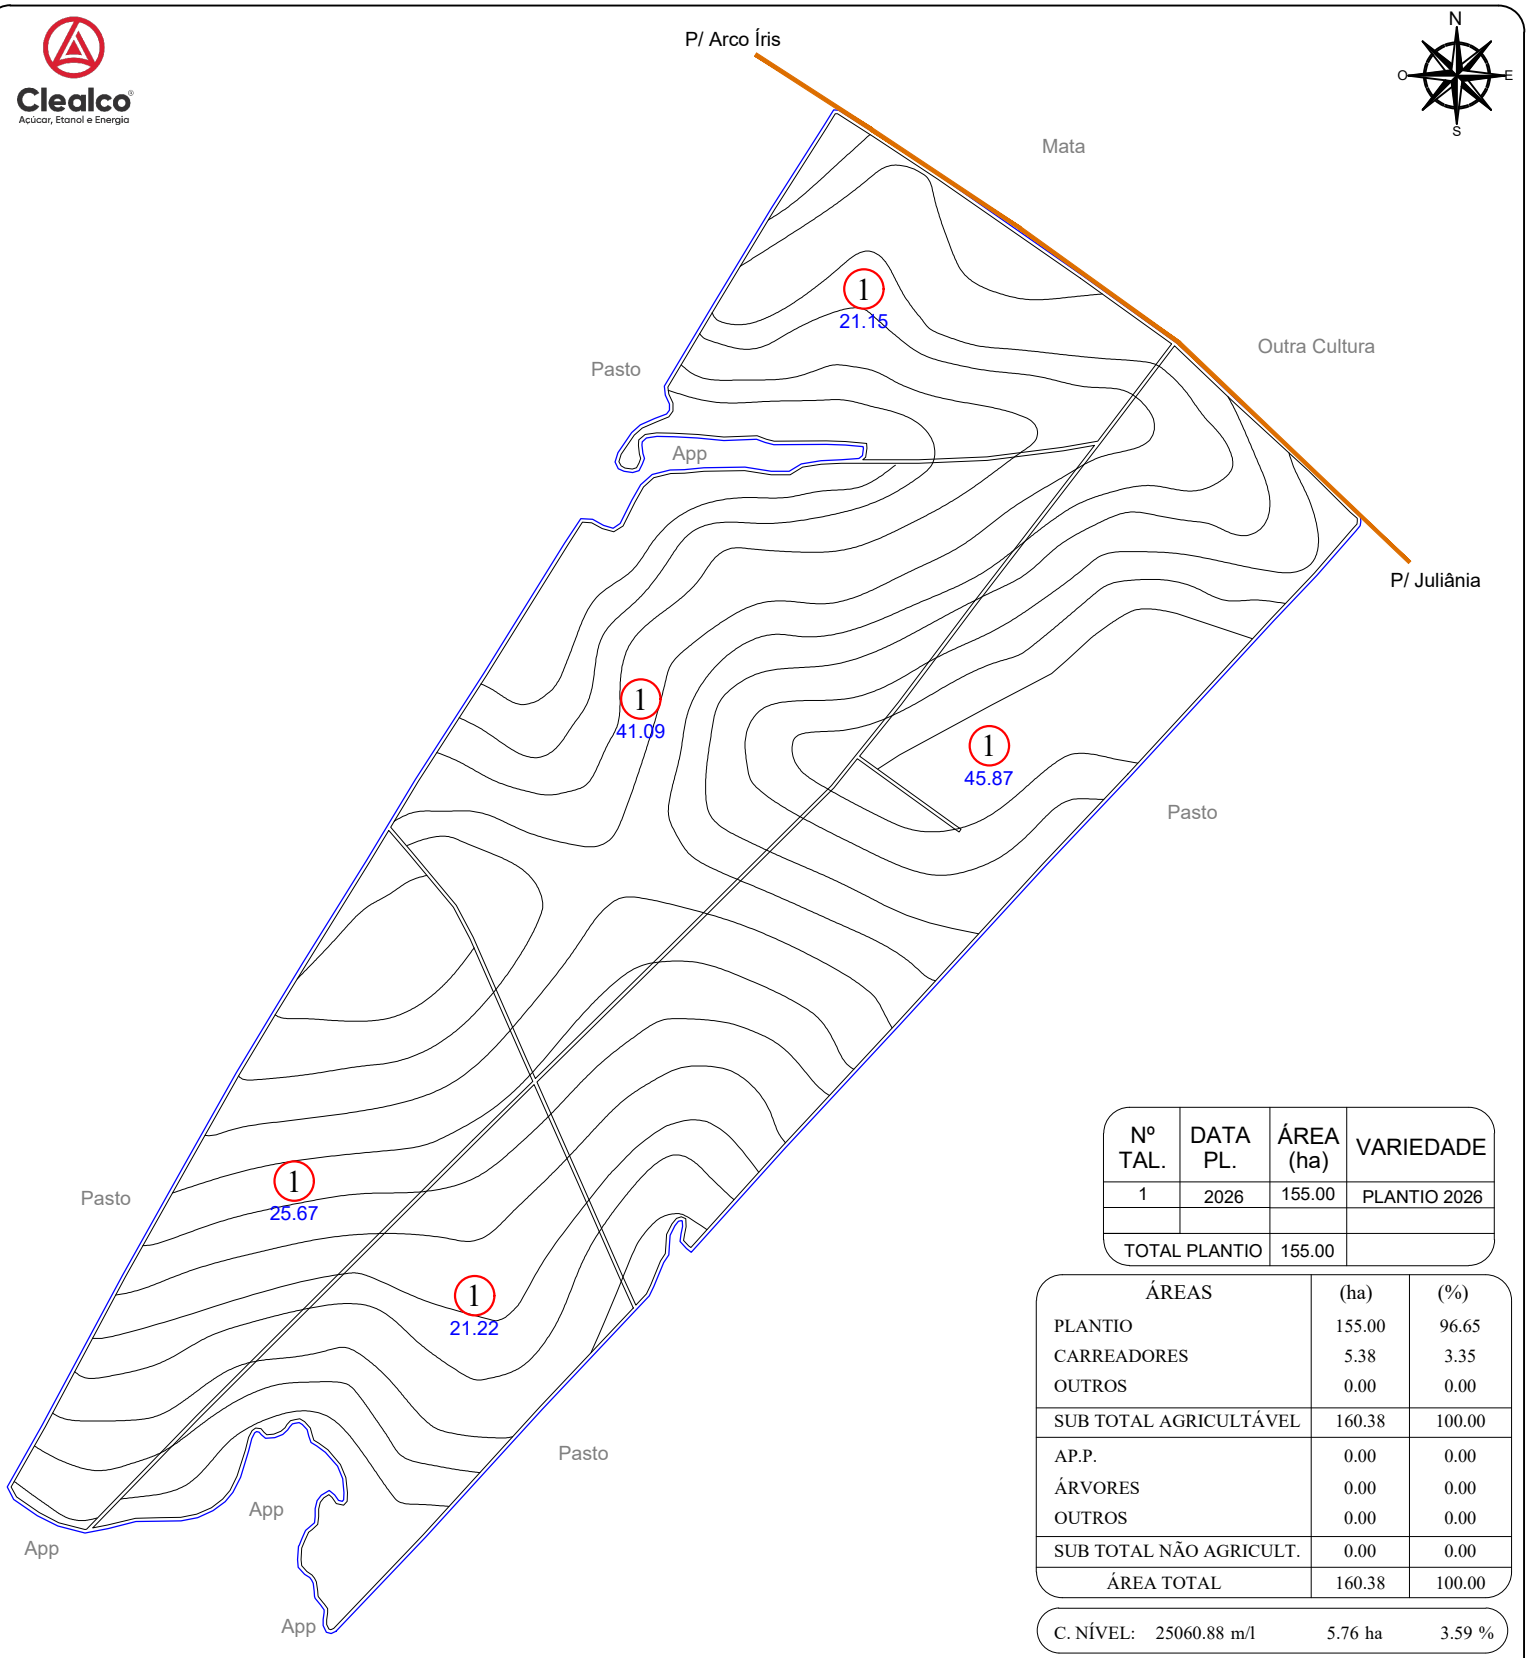

Nº TAL.	DATA PL.	ÁREA (ha)	VARIEDADE
1	2026	155.00	PLANTIO 2026
TOTAL PLANTIO		155.00	

ÁREAS	(ha)	(%)
PLANTIO	155.00	96.65
CARREADORES	5.38	3.35
OUTROS	0.00	0.00
SUB TOTAL AGRICULTÁVEL	160.38	100.00
AP.P.	0.00	0.00
ÁRVORES	0.00	0.00
OUTROS	0.00	0.00
SUB TOTAL NÃO AGRICULT.	0.00	0.00
ÁREA TOTAL	160.38	100.00

C. NÍVEL: 25060.88 m/l 5.76 ha 3.59 %


LEGENDA

- FAZENDA
- TALHÃO
- REDE ELÉTRICA
- VAZIO
- TERRAÇO BASE LARGA
- TERRAÇO EMBUTIDO
- (P.O.A) PATIO DE OPERAÇÃO
- CARREGADO

ESPAÇAMENTO: 1.50 x 1.50
TIRO MÉDIO ESTIMADO: 327.24 m
D.V: 4.95 %

ESCALA: 1: 11.000

CROQUI DE ACESSO

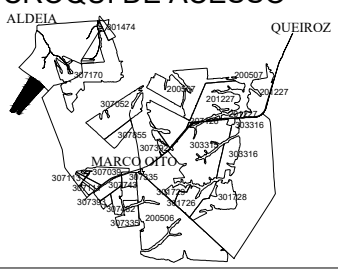

FAZENDA SÃO JOÃO

PROPRIETÁRIO: ANTONIO IRVANDO DE ANDRADE
COMPRADOR: CLEALCO
MUNICÍPIO: TUPÃ - SP

DISTÂNCIAS (km):
UNID. I - Asfalto: 38.70 Terra.: 12.50
UNID.I I - Asfalto: 20.60 Terra.: 9.30

COORDENADAS: E(X): 562998.97 N(Y): 7585352.98
LAT: -21°50'4.6472" LONG: -50°23'25.3710"

CLEALCO - AÇÚCAR E ALCOOL S/A - DEPARTAMENTO DE GEOTECNOLOGIA

LEVANTAMENTO VIA:
SATÉLITE
GPS / VANT
GOOGLE

UNIDADE: II
PARTE: A/A
FUNDO AGRÍCOLA: 308184

M:\01-Mapa de safra\Mapas Atualizados\Clealco\308184 - Fazenda São João Do Iacri (Antonio Irvando de Andrade)\308184 - Fazenda São João Do Iacri (Antonio Irvando de Andrade).dwg

Peterson Santos 23/10/26