
Clealco
Açúcar, Etanol e Energia

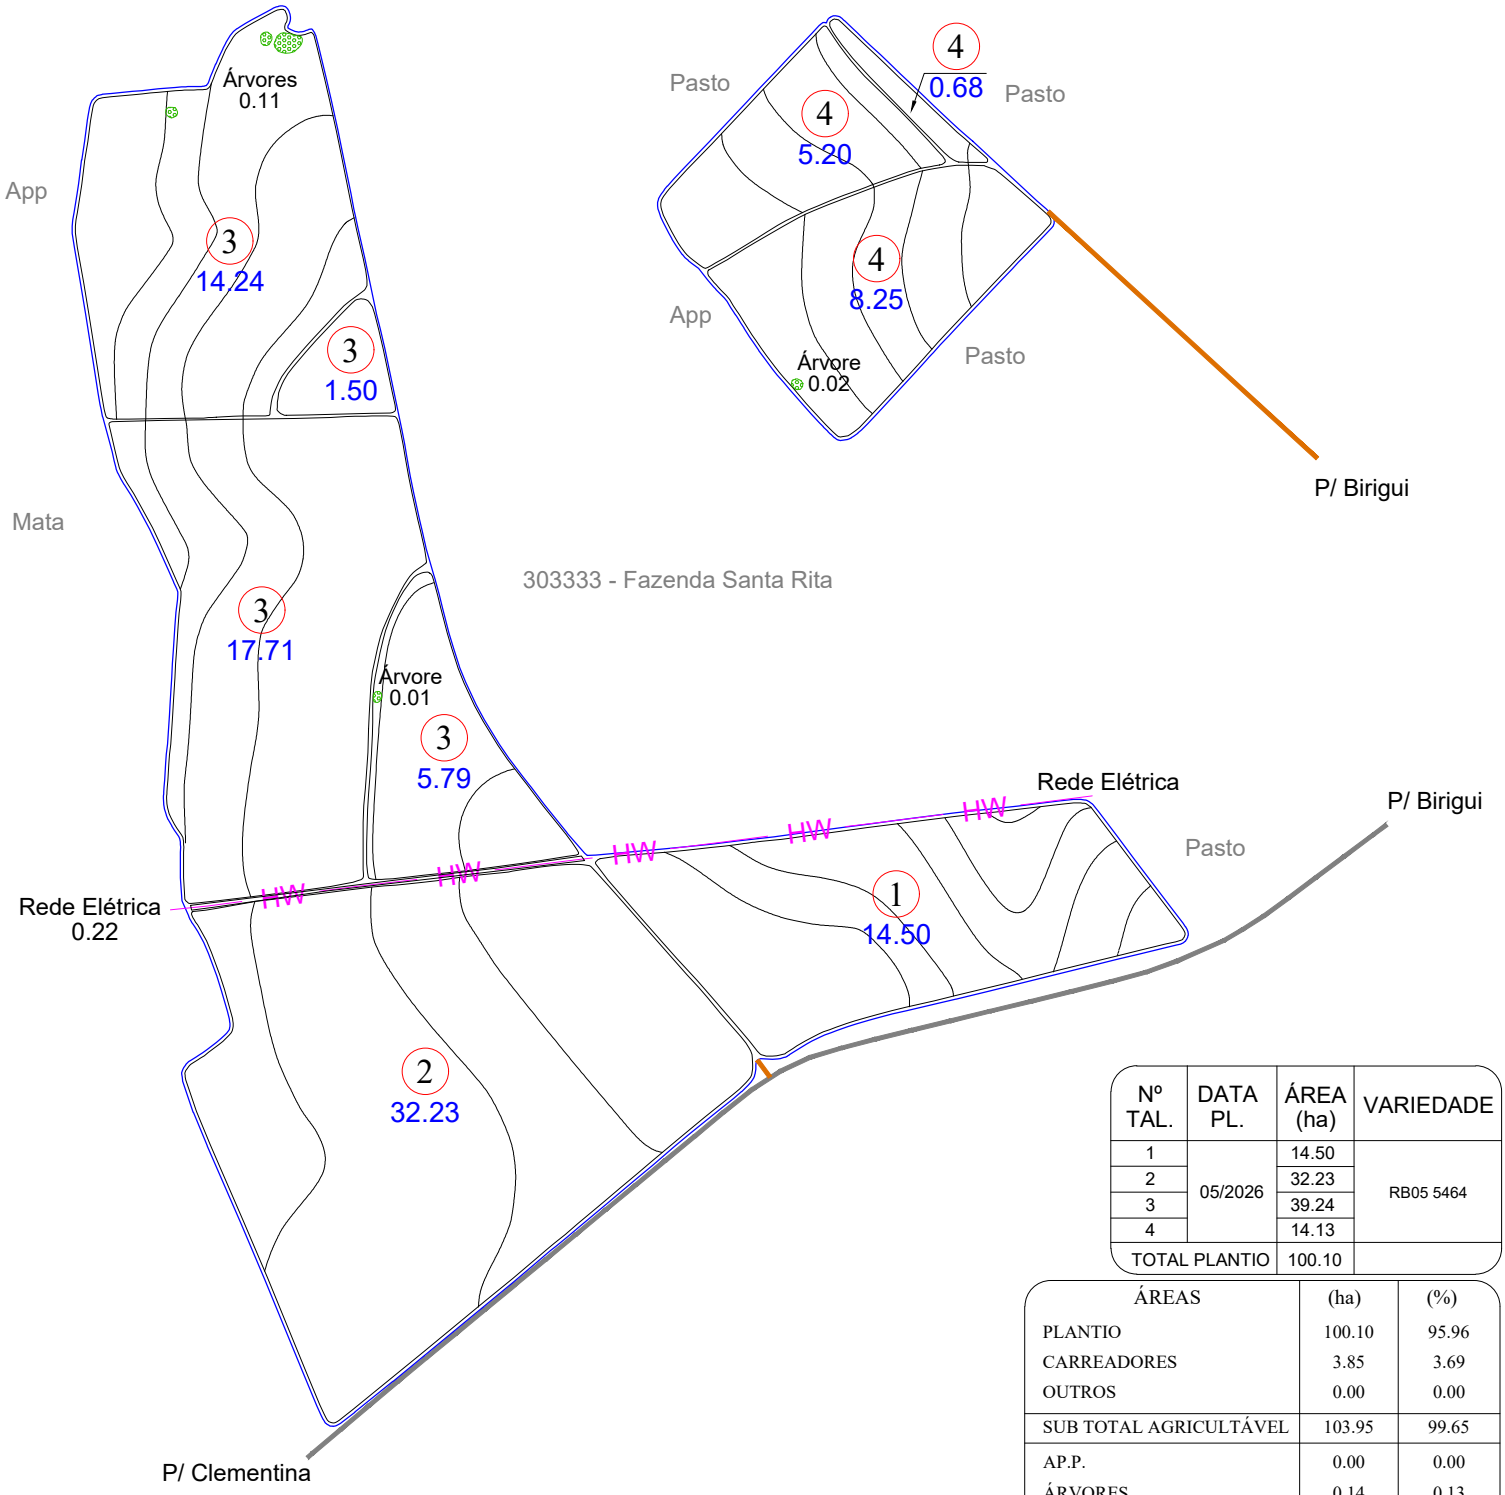

Nº TAL.	DATA PL.	ÁREA (ha)	VARIEDADE
1	05/2026	14.50	RB05 5464
2		32.23	
3		39.24	
4		14.13	
TOTAL PLANTIO		100.10	

ÁREAS	(ha)	(%)
PLANTIO	100.10	95.96
CARREADORES	3.85	3.69
OUTROS	0.00	0.00
SUB TOTAL AGRICULTÁVEL	103.95	99.65
AP.P.	0.00	0.00
ÁRVORES	0.14	0.13
OUTROS	0.22	0.21
SUB TOTAL NÃO AGRICULT.	0.36	0.35
ÁREA TOTAL	104.31	100.00

LEGENDA

- FAZENDA
- TALHÃO
- REDE ELÉTRICA
- TERRAÇO BASE LARGA
- TERRAÇO EMBUTIDO
- (P.O.A) PATIO DE OPERAÇÃO


ESCALA: 1: 10.000

ESPAÇAMENTO: 1.50 x 1.50
TIRO MÉDIO ESTIMADO: 000.00 m

D.V: 0.00 %

C. NÍVEL: 8571.51 m/l 1.97 ha 1.89 %

CROQUI DE ACESSO

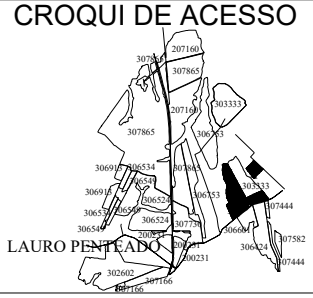

FAZENDA SANTA RITA

PROPRIETÁRIO: JORGE LUIZ ZAGO
COMPRADOR: CLEALCO
MUNICÍPIO: COROADOS - SP

DISTÂNCIAS (km):
UNID. I - Asfalto: 11.20 Terra.: 1.20
UNID.I I - Asfalto: 67.00 Terra.: 1.20

COORDENADAS: E(X): 561659.63 N(Y): 7623215.74
LAT: -21°29'33.3693" LONG: -50°24'17.0848"

CLEALCO - AÇÚCAR E ALCOOL S/A - DEPARTAMENTO DE GEOTECNOLOGIA

LEVANTAMENTO VIA:
- SATÉLITE
- GPS / VANT
- GOOGLE

UNIDADE: I

PARTE: A/A

FUNDO AGRÍCOLA: 308186

M:\01-Mapa de safra\Mapas Atualizados\Terceiro\308186 - Fazenda Santa Rita (Jorge Luiz Zago)\308186 - Fazenda Santa Rita (Jorge Luiz Zago).dwg

Bruno Gamboa 22/09/26