
Clealco
Açúcar, Etanol e Energia

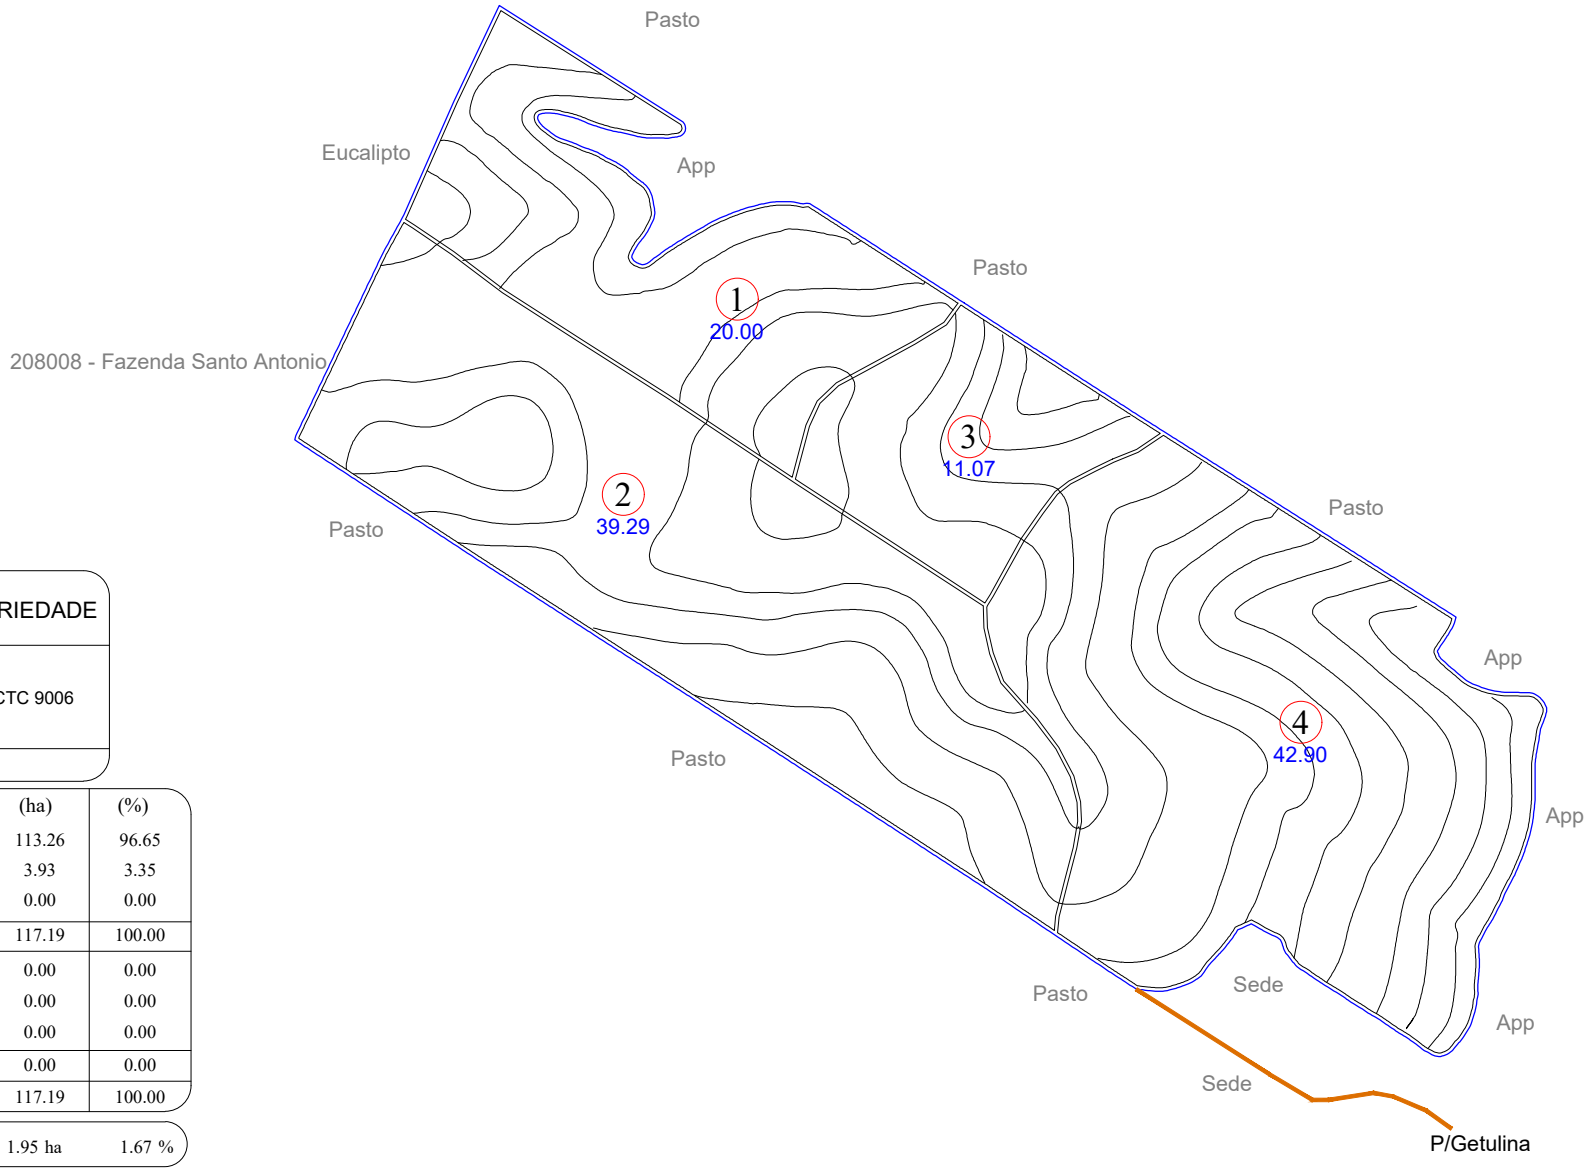

N
O
E
S

Nº TAL.	DATA PL.	ÁREA (ha)	VARIEDADE
1	06/2025	20.00	CTC 9006
2		39.29	
3		11.07	
4		42.90	
TOTAL PLANTIO		113.26	

ÁREAS	(ha)	(%)
PLANTIO	113.26	96.65
CARREADORES	3.93	3.35
OUTROS	0.00	0.00
SUB TOTAL AGRICULTÁVEL	117.19	100.00
AP.P.	0.00	0.00
ÁRVORES	0.00	0.00
OUTROS	0.00	0.00
SUB TOTAL NÃO AGRICULT.	0.00	0.00
ÁREA TOTAL	117.19	100.00


C. NÍVEL:	8488.05 m/l	1.95 ha	1.67 %

ESCALA: 1: 11.000

LEGENDA
- FAZENDA
- TALHÃO
- REDE ELÉTRICA
- TERRAÇO BASE LARGA
- TERRAÇO EMBUTIDO
- VAZIO
- CARREGADO

ESPAÇAMENTO: 1.50 x 1.50
TIRO MÉDIO ESTIMADO: 301.20 m
D.V: 4.97 %

CROQUI DE ACESSO

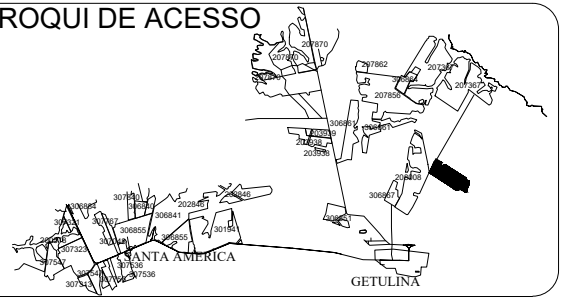

FAZENDA RIACHUELO

PROPRIETÁRIO: ROGERIO AGUIAR DOS REIS
COMPRADOR: CLEALCO
MUNICÍPIO: GETULINA - SP

DISTÂNCIAS (km):
UNID. I - Asfalto: 91.10 Terra.: 6.50
UNID.I I - Asfalto: 40.00 Terra.: 6.50

COORDENADAS: E(X): 612316.94 N(Y): 7592787.26
LAT: -21°45'54.0580" LONG: -49°54'49.3396"
CLEALCO - AÇÚCAR E ALCOOL S/A - DEPARTAMENTO DE GEOTECNOLOGIA

LEVANTAMENTO VIA:
- SATÉLITE
- GPS / VANT
- GOOGLE

UNIDADE: II
PARTE: A/A
FUNDO AGRÍCOLA: 308188

M:\01-Mapa de safra\Mapas Atualizados\Terceiro\308188 - Fazenda Riachuelo (Rogerio Aguiar Dos Reis)\308188 - Fazenda Riachuelo (Rogerio Aguiar Dos Reis).dwg

Bruno Gamboa 18/03/26