
Clealco
Açúcar, Etanol e Energia

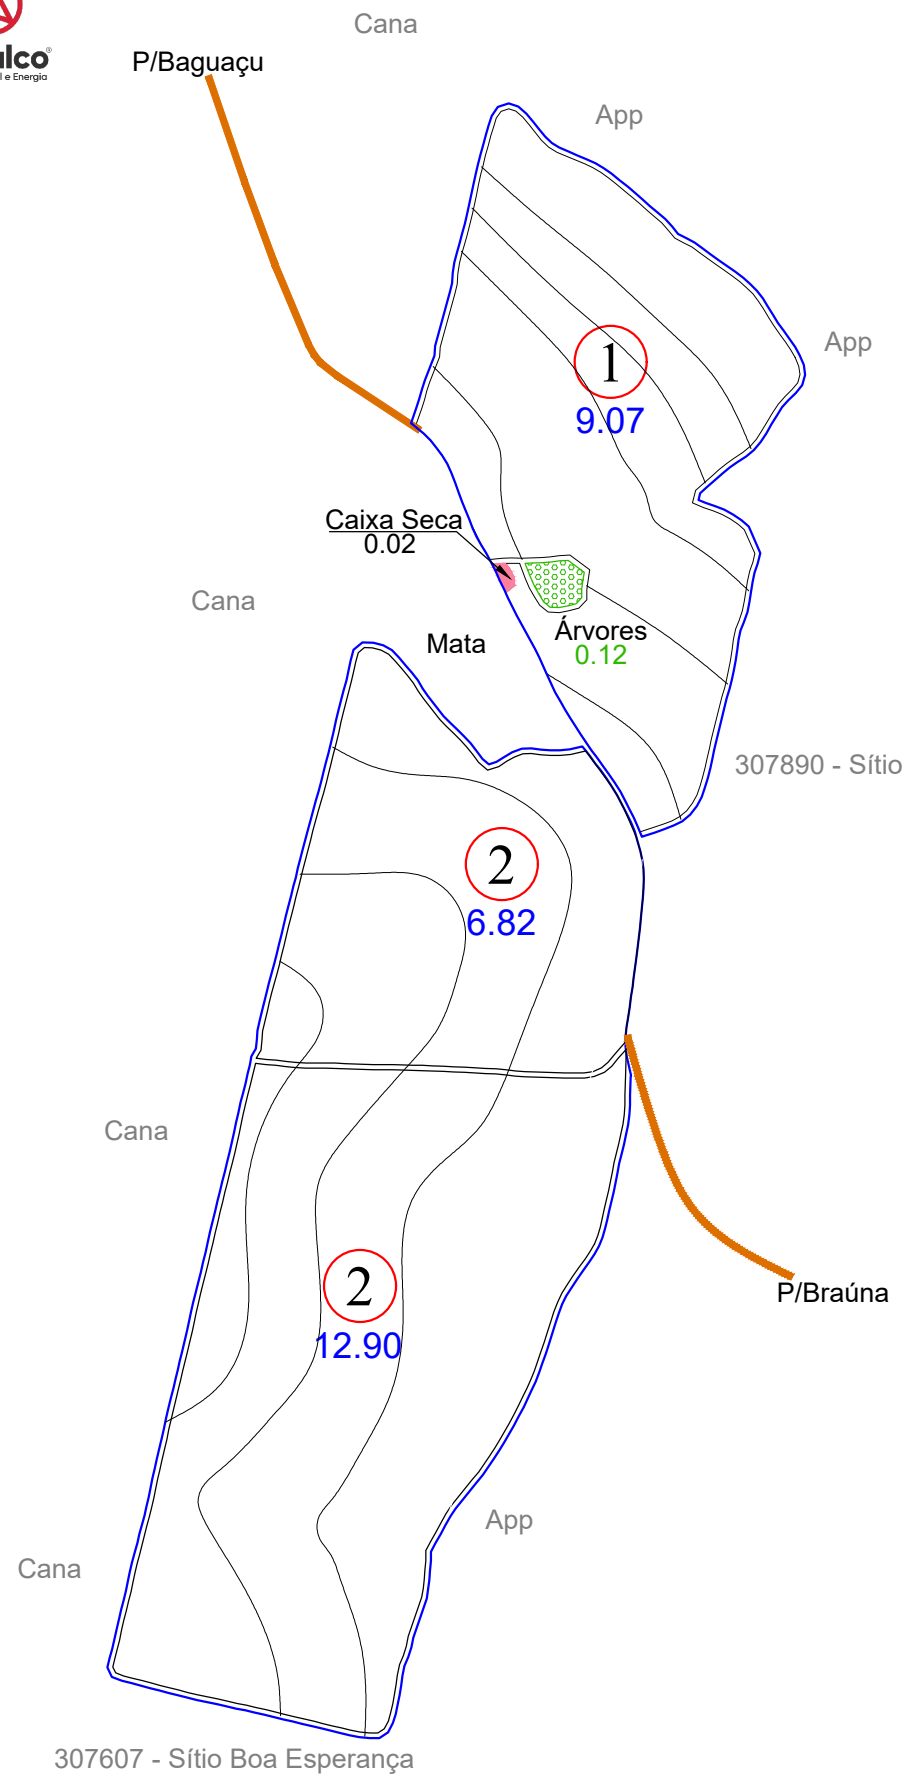

N
O E
S

Nº TAL.	DATA PL.	ÁREA (ha)	VARIEDADE
1	05/2025	9.07	RB97 5201
2		19.72	
TOTAL PLANTIO		28.79	

ÁREAS	(ha)	(%)
PLANTIO	28.79	95.12
CARREADORES	1.34	4.42
OUTROS	0.02	0.07
SUB TOTAL AGRICULTÁVEL	30.15	99.60
AP.P.	0.00	0.00
ÁRVORES	0.12	0.40
OUTROS	0.00	0.00
SUB TOTAL NÃO AGRICULT.	0.12	0.40
ÁREA TOTAL	30.27	100.00

C. NÍVEL: 4160.15 m/l 0.96 ha 3.16 %


LEGENDA

- FAZENDA
- TALHÃO
- REDE ELÉTRICA
- TERRAÇO BASE LARGA
- TERRAÇO EMBUTIDO
- (P.O.A) PATIO DE OPERAÇÃO

ESPAÇAMENTO: 1.50 x 1.50
TIRO MÉDIO ESTIMADO: 234.53 m
D.V: 5.71 %

ESCALA: 1: 6.000

CROQUI DE ACESSO

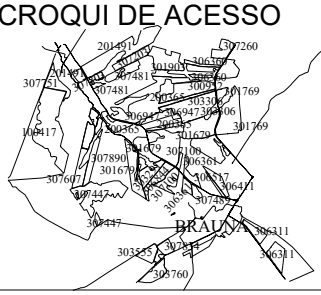

SÍTIO SÃO JOSÉ

PROPRIETÁRIO: ANDRÉ LUIZ FERREIRA
COMPRADOR: CLEALCO
MUNICÍPIO: COROADOS - SP

DISTÂNCIAS (km):
UNID. I - Asfalto: 19.10 Terra.: 3.20
UNID.I I - Asfalto: 77.00 Terra.: 3.20

COORDENADAS: E(X): 566724.38 N(Y): 7625397.73
LAT: -21°28'21.7487" LONG: -50°21'21.3850"

CLEALCO - AÇÚCAR E ALCOOL S/A - DEPARTAMENTO DE GEOTECNOLOGIA

LEVANTAMENTO VIA:
SATÉLITE
GPS / VANT
GOOGLE

UNIDADE: I
PARTE: A/A
FUNDO AGRÍCOLA: 308195

M:\01-Mapa de safra\Mapas Atualizados\Terceiro\308195 - Sitio Sao Jose (Andre Luiz Ferreira)\308195 - Sitio Sao Jose (Andre Luiz Ferreira).dwg

Bruno Gamboa 05/11/25