
Clealco
Açúcar, Etanol e Energia

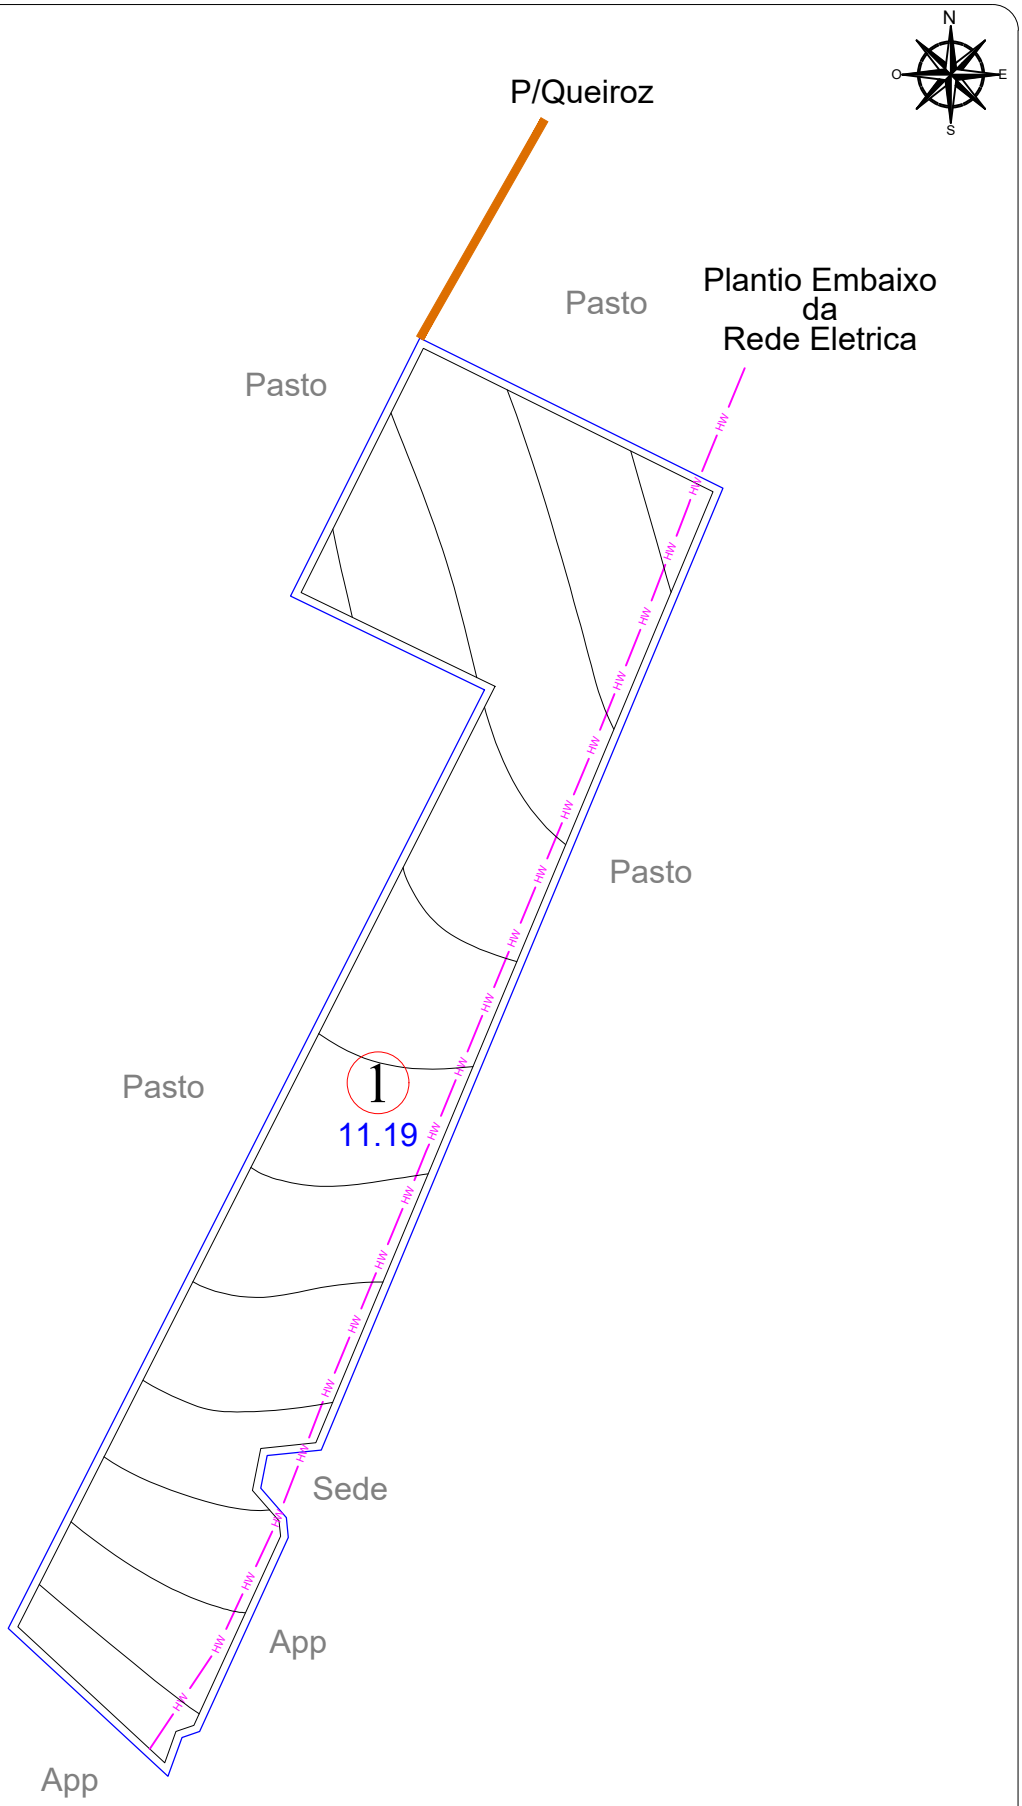

Nº TAL.	DATA PL.	ÁREA (ha)	VARIEDADE
1	05/2025	11.19	RB86 7515
TOTAL PLANTIO		11.19	

ÁREAS	(ha)	(%)
PLANTIO	11.19	90.70
CARREADORES	1.15	9.30
OUTROS	0.00	0.00
SUB TOTAL AGRICULTÁVEL	12.34	100.00
AP.P.	0.00	0.00
ÁRVORES	0.00	0.00
OUTROS	0.00	0.00
SUB TOTAL NÃO AGRICULT.	0.00	0.00
ÁREA TOTAL	12.34	100.00

C. NÍVEL:	1620.39 m/l	0.37 ha	3.02 %


LEGENDA

- FAZENDA
- TALHÃO
- REDE ELÉTRICA
- VAZIO
- TERRAÇO BASE LARGA
- TERRAÇO EMBUTIDO
- (P.O.A) PATIO DE OPERAÇÃO
- CARREGADO

ESPAÇAMENTO:	1.50 x 1.50	D.V: 6.04 %
TIRO MÉDIO ESTIMADO:	112.46 m	

ESCALA: 1: 5.000

CROQUI DE ACESSO

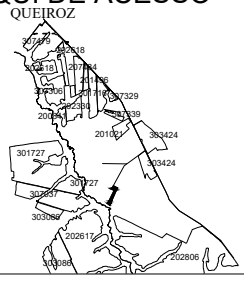

SÍTIO EL SHADDAI

PROPRIETÁRIO: MANOEL ANANIAS GARCIA
COMPRADOR: CLEALCO
MUNICÍPIO: QUEIROZ - SP

DISTÂNCIAS (km):
UNID. I - Asfalto: 62.90 Terra.: 3.00
UNID.I I - Asfalto: 8.00 Terra.: 3.00

COORDENADAS: E(X): 581876.66 N(Y): 7580411.10
LAT: -21°52'42.5729" LONG: -50°12'26.9047"

CLEALCO - AÇÚCAR E ALCOOL S/A - DEPARTAMENTO DE GEOTECNOLOGIA

LEVANTAMENTO VIA:
- SATÉLITE
- GPS / VANT
- GOOGLE

UNIDADE: II
PARTE: A/A
FUNDO AGRÍCOLA: 308197

M:\01-Mapa de safra\Mapas Atualizados\Terceiro\308197 - Sitio El Shadaai (Manoel Ananias Garcia)\308197 - Sitio El Shadaai (Manoel Ananias Garcia).dwg

Bruno Gamboa 28/04/26