
Clealco
Açúcar, Etanol e Energia

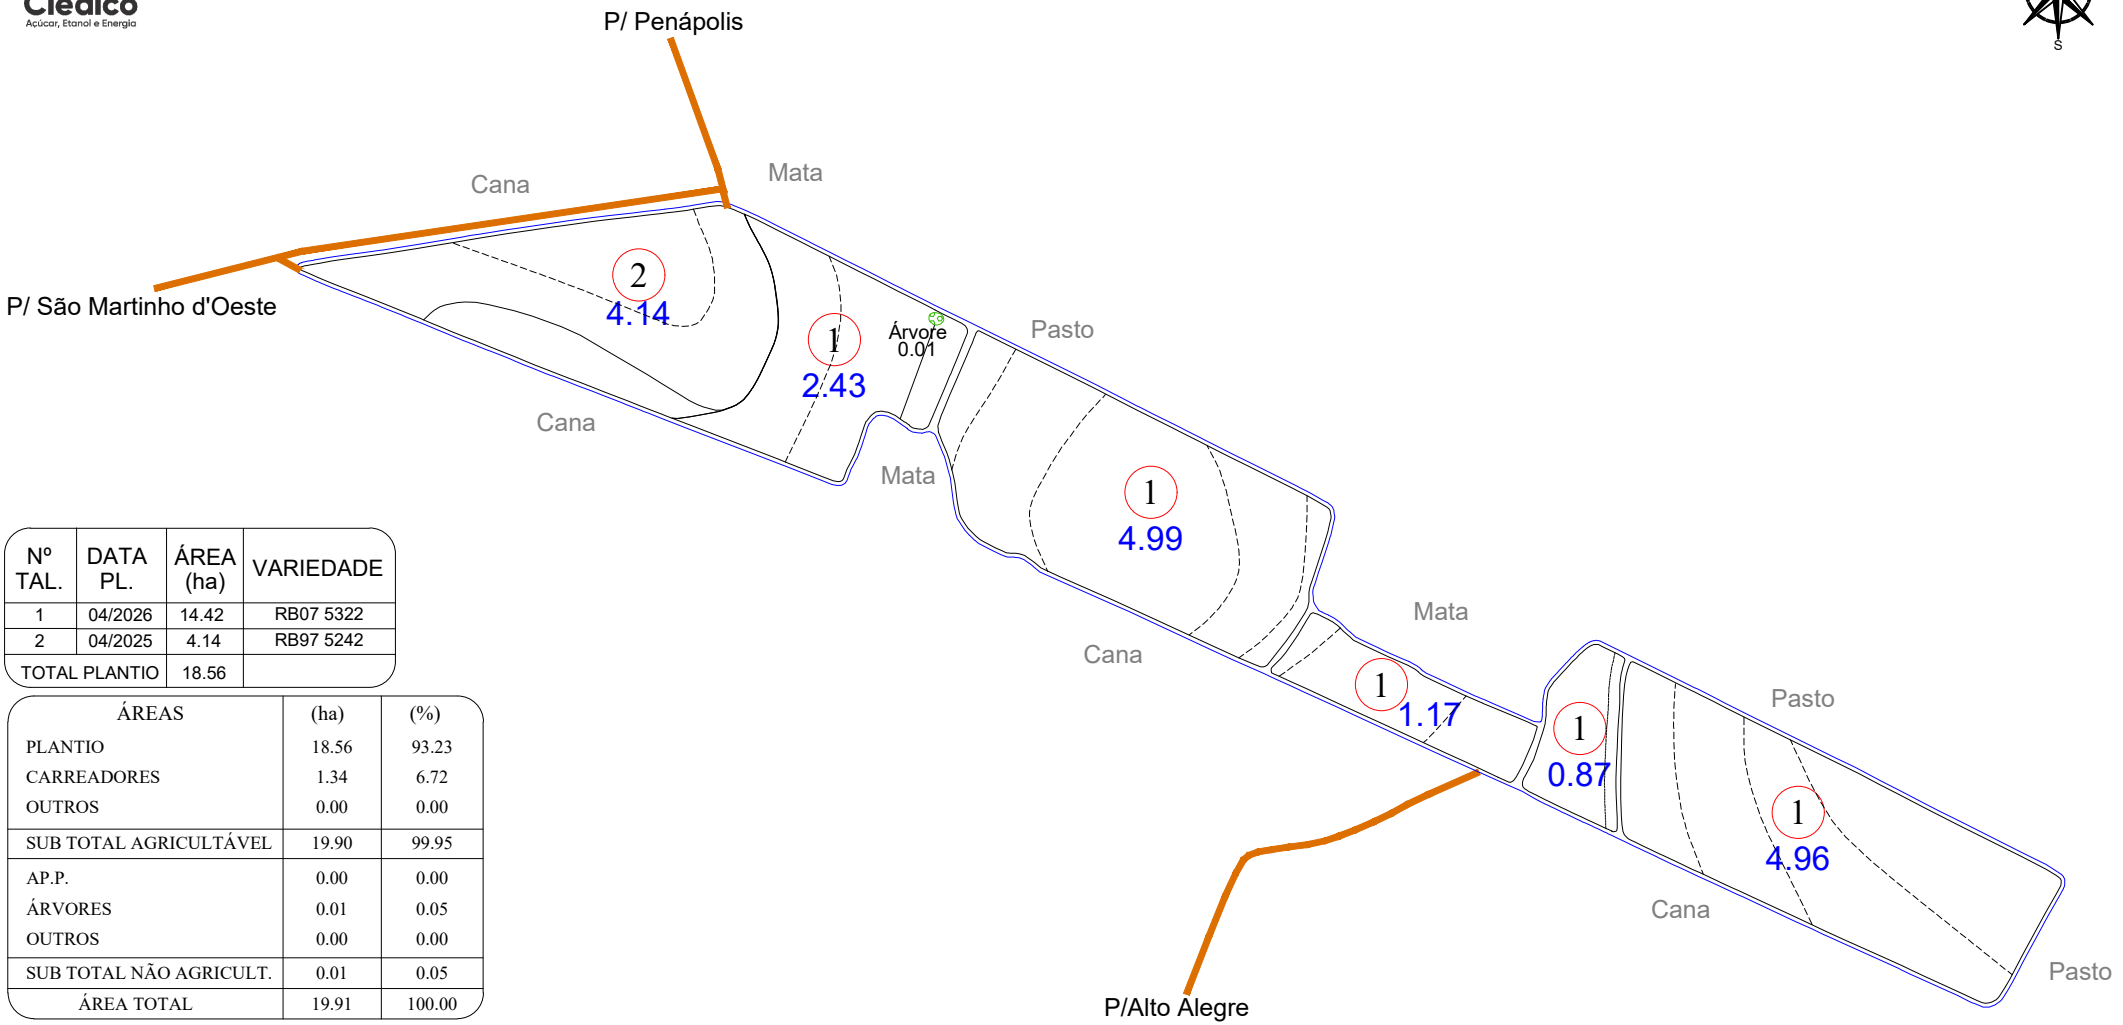

Nº TAL.	DATA PL.	ÁREA (ha)	VARIEDADE
1	04/2026	14.42	RB07 5322
2	04/2025	4.14	RB97 5242
TOTAL PLANTIO		18.56	

ÁREAS	(ha)	(%)
PLANTIO	18.56	93.23
CARREADORES	1.34	6.72
OUTROS	0.00	0.00
SUB TOTAL AGRICULTÁVEL	19.90	99.95
AP.P.	0.00	0.00
ÁRVORES	0.01	0.05
OUTROS	0.00	0.00
SUB TOTAL NÃO AGRICULT.	0.01	0.05
ÁREA TOTAL	19.91	100.00

C. NÍVEL:	614.48 m/l	0.14 ha	0.71 %


ESCALA: 1: 6.500

LEGENDA

- FAZENDA
- TALHÃO
- REDE ELÉTRICA
- TERRAÇO BASE LARGA
- TERRAÇO EMBUTIDO

ESPAÇAMENTO:	1.50 x 1.50	D.V: 4.46 %
TIRO MÉDIO ESTIMADO:	136.33 m	

CROQUI DE ACESSO

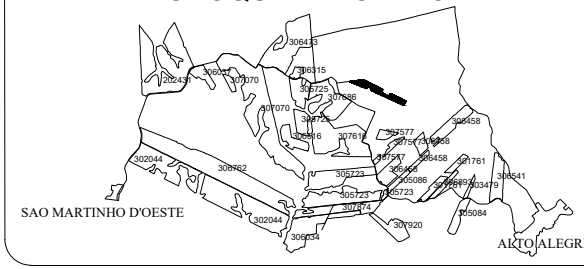

ESTÂNCIA DYMONT

PROPRIETÁRIO: PAULO CESAR LOPES
COMPRADOR: CLEALCO
MUNICÍPIO: ALTO ALEGRE - SP

DISTÂNCIAS (km):
UNID. I - Asfalto: 31.00 Terra.: 10.50
UNID.I I - Asfalto: 40.00 Terra.: 10.00

COORDENADAS: E(X): 582001.95 N(Y): 7616601.19
LAT: -21°33'5.5620" LONG: -50°12'28.9883"

CLEALCO - AÇÚCAR E ALCOOL S/A - DEPARTAMENTO DE GEOTECNOLOGIA

LEVANTAMENTO VIA:
SATÉLITE
GPS / VANT
GOOGLE

UNIDADE: I

PARTE: A/A

FUNDO AGRÍCOLA: 308214

M:\01-Mapa de safra\Mapas Atualizados\Terceiro\308214 - Estância Dymont (Paulo Cesar Lopes)\308214 - Estância Dymont (Paulo Cesar Lopes).dwg

Bruno Gamboa 21/09/26