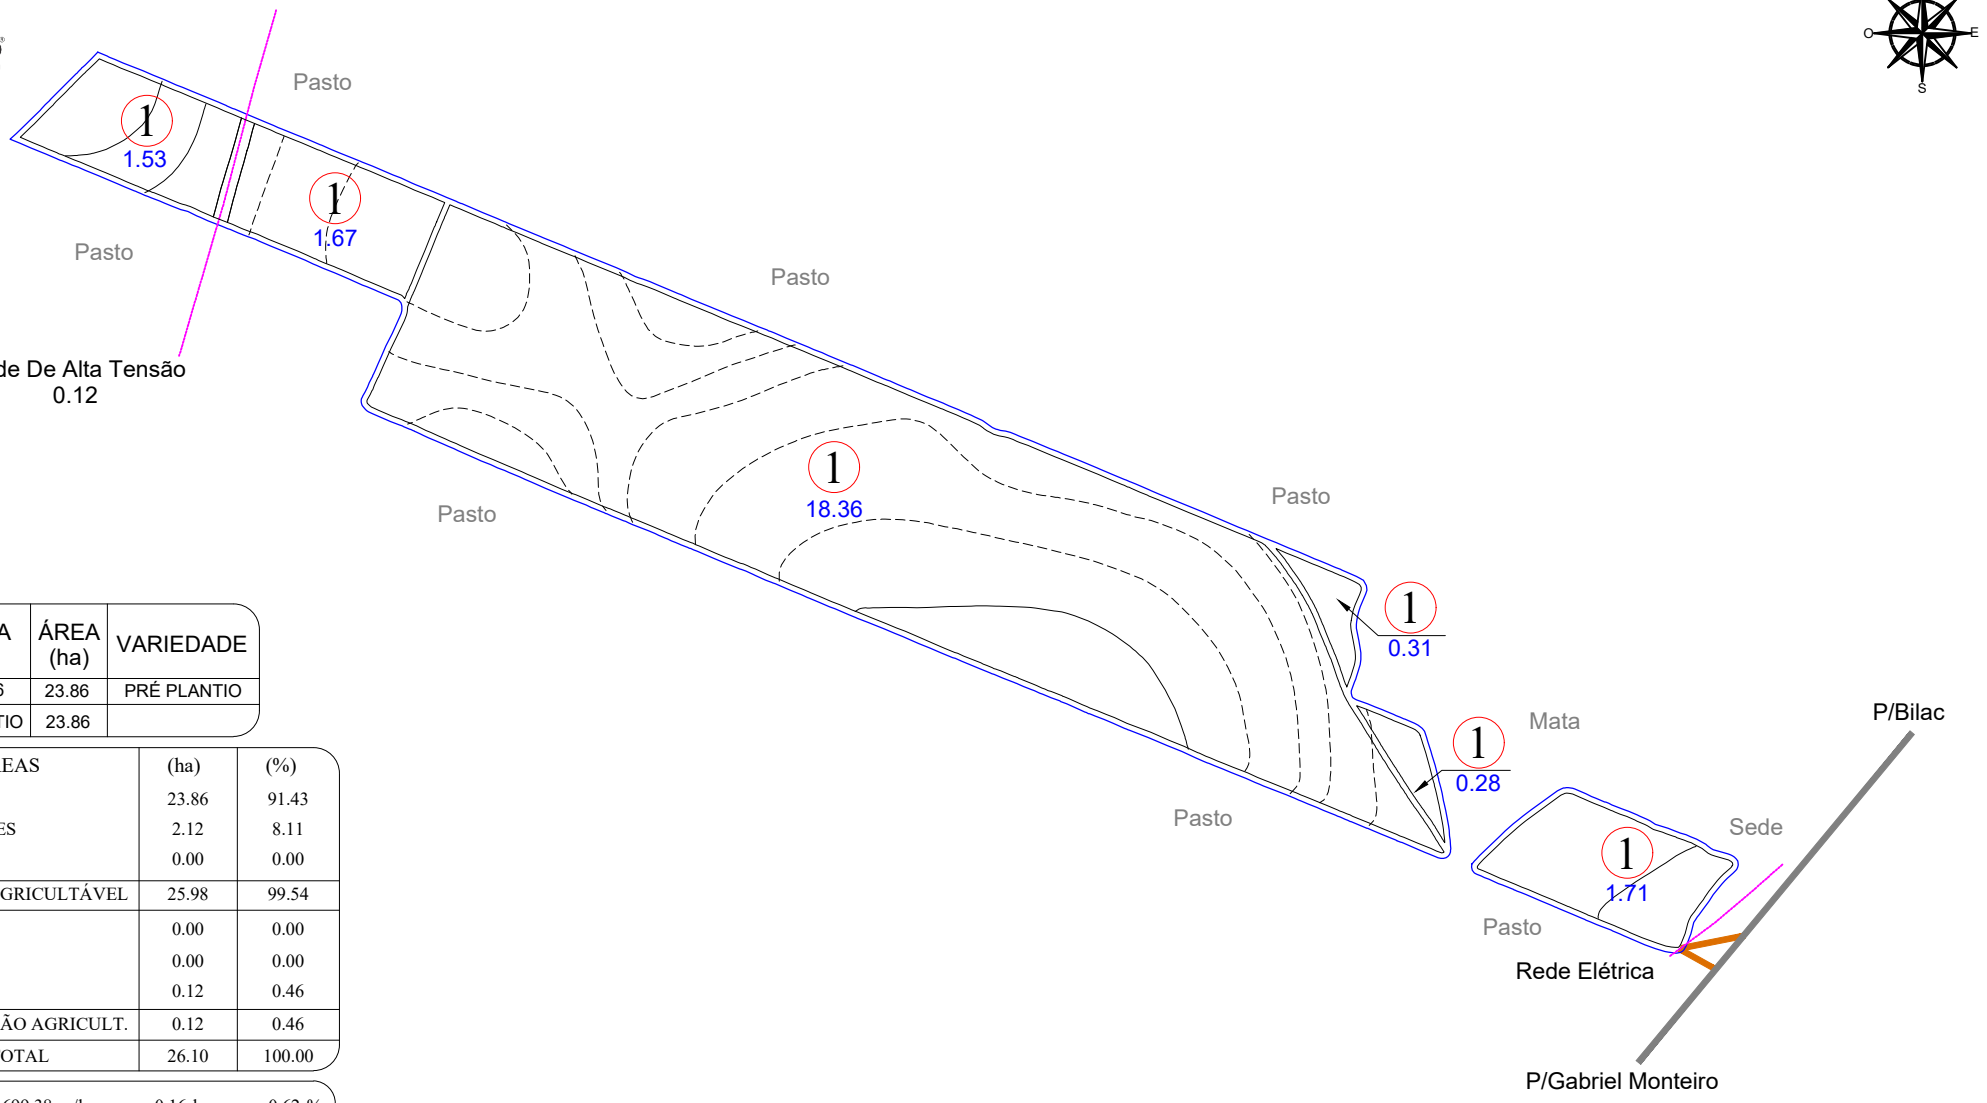


ESCALA: 1: 7.000

Nº TAL.	DATA PL.	ÁREA (ha)	VARIEDADE
1	2026	23.86	PRÉ PLANTIO
TOTAL PLANTIO		23.86	

ÁREAS	(ha)	(%)
PLANTIO	23.86	91.43
CARREADORES	2.12	8.11
OUTROS	0.00	0.00
SUB TOTAL AGRICULTÁVEL	25.98	99.54
AP.P.	0.00	0.00
ÁRVORES	0.00	0.00
OUTROS	0.12	0.46
SUB TOTAL NÃO AGRICULT.	0.12	0.46
ÁREA TOTAL	26.10	100.00


C. NÍVEL: 699.38 m/l 0.16 ha 0.62 %

LEGENDA

- FAZENDA
- TALHÃO
- REDE ELÉTRICA
- TERRAÇO BASE LARGA
- TERRAÇO EMBUTIDO
- VAZIO
- CARREGADO

ESPAÇAMENTO: 1.50 x 1.50
TIRO MÉDIO ESTIMADO: 296.30 m
D.V: 3.67 %

CROQUI DE ACESSO

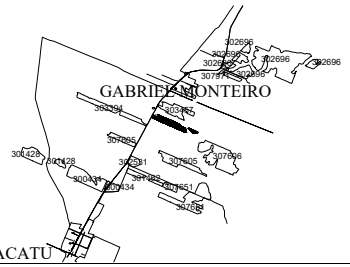

SÍTIO BOA SORTE

PROPRIETÁRIO: ROBERLEI BUENO DE OLIVEIRA
COMPRADOR: CLEALCO
MUNICÍPIO: PIACATU - SP

DISTÂNCIAS (km):
UNID. I - Asfalto: 38.60 Terra.: 4.58
UNID.I I - Asfalto: 64.60 Terra.: 4.58

COORDENADAS: E(X): 546356.88 N(Y): 7620283.98
LAT: -21°31'10.3855" LONG: -50°33'8.6095"
CLEALCO - AÇÚCAR E ALCOOL S/A - DEPARTAMENTO DE GEOTECNOLOGIA

LEVANTAMENTO VIA:
SATÉLITE
GPS / VANT
GOOGLE

UNIDADE: I
PARTE: A/A
FUNDO AGRÍCOLA: 308217

M:\01-Mapa de safra\Mapas Atualizados\Terceiro\308217 - Sítio Boa Sorte (Roberlei Bueno De Oliveira)\308217 - Sítio Boa Sorte (Roberlei Bueno De Oliveira).dwg

Bruno Gamboa 06/05/26