
Clealco
Açúcar, Etanol e Energia

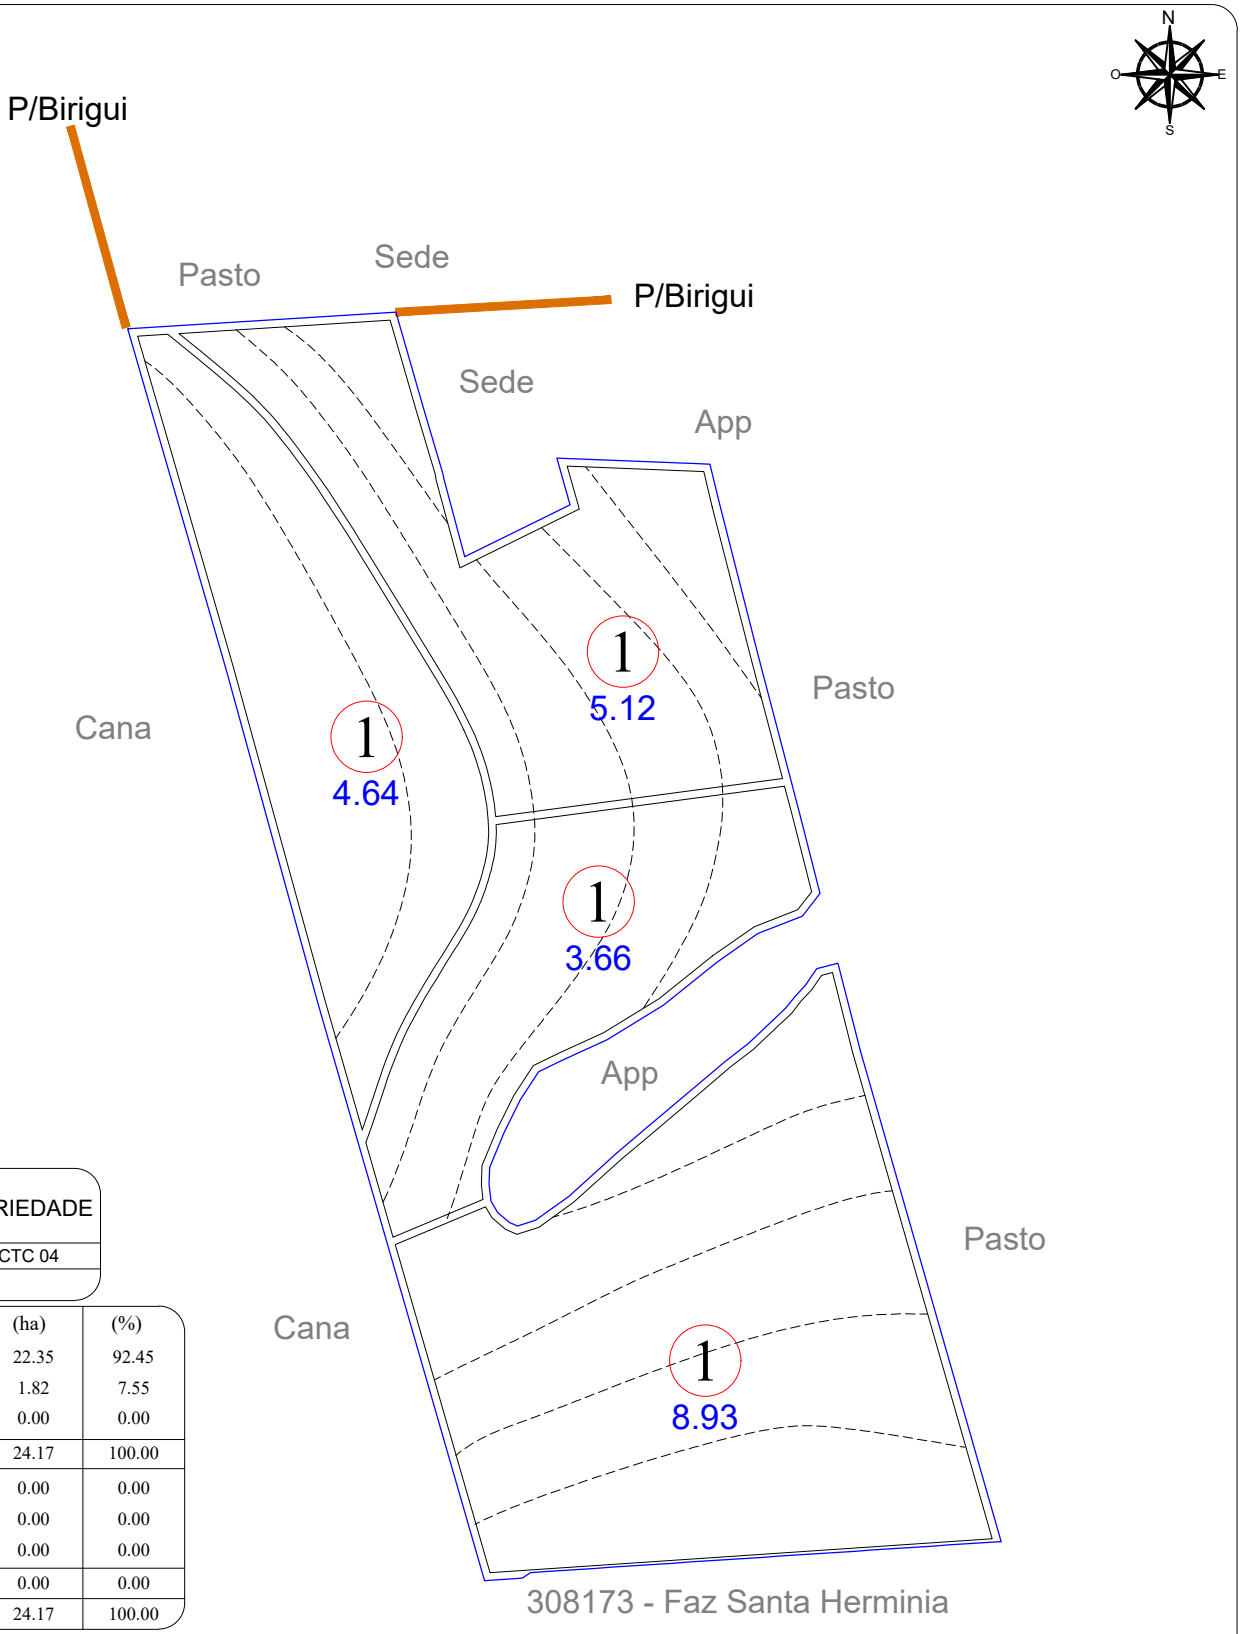

Nº TAL.	DATA PL.	ÁREA (ha)	VARIEDADE
1	2026	22.35	CTC 04
TOTAL PLANTIO		22.35	

ÁREAS	(ha)	(%)
PLANTIO	22.35	92.45
CARREADORES	1.82	7.55
OUTROS	0.00	0.00
SUB TOTAL AGRICULTÁVEL	24.17	100.00
AP.P.	0.00	0.00
ÁRVORES	0.00	0.00
OUTROS	0.00	0.00
SUB TOTAL NÃO AGRICULT.	0.00	0.00
ÁREA TOTAL	24.17	100.00

C. NÍVEL: 0.00 m/l 0.00 ha 0.00 %


LEGENDA

- FAZENDA
- TALHÃO
- REDE ELÉTRICA
- VAZIO
- TERRAÇO BASE LARGA
- TERRAÇO EMBUTIDO
- (P.O.A) PATIO DE OPERAÇÃO
- CARREGADO

ESPAÇAMENTO: 1.50 x 1.50
TIRO MÉDIO ESTIMADO: 263.84 m
D.V: 5.92 %

ESCALA: 1: 5.000

CROQUI DE ACESSO

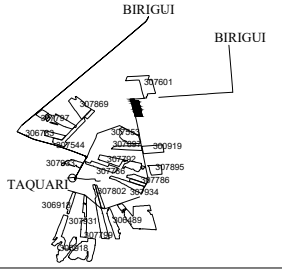

SÍTIO NOSSA SENHORA APARECIDA

PROPRIETÁRIO: WANDO IASSIA GIMENEZ
COMPRADOR: CLEALCO
MUNICÍPIO: BIRIGUI - SP

DISTÂNCIAS (km):
UNID. I - Asfalto: 28.50 Terra.: 4.00
UNID.I I - Asfalto: 84.00 Terra.: 4.00

COORDENADAS: E(X): 564023.56 N(Y): 7638170.57
LAT: -21°21'26.6684" LONG: -50°22'56.9785"

CLEALCO - AÇÚCAR E ALCOOL S/A - DEPARTAMENTO DE GEOTECNOLOGIA

LEVANTAMENTO VIA:
SATÉLITE
GPS / VANT
GOOGLE

UNIDADE: I
PARTE: A/A
FUNDO AGRÍCOLA: 308228

M:\01-Mapa de safra\Mapas Atualizados\Terceiro\308228 - Sítio Nossa Senhora Aparecida (Wando Iassia Gimenez)\308228 - Sítio Nossa Senhora Aparecida (Wando Iassia Gimenez).dwg

Bruno Gamboa 15/04/26