
Clealco
Açúcar, Etanol e Energia

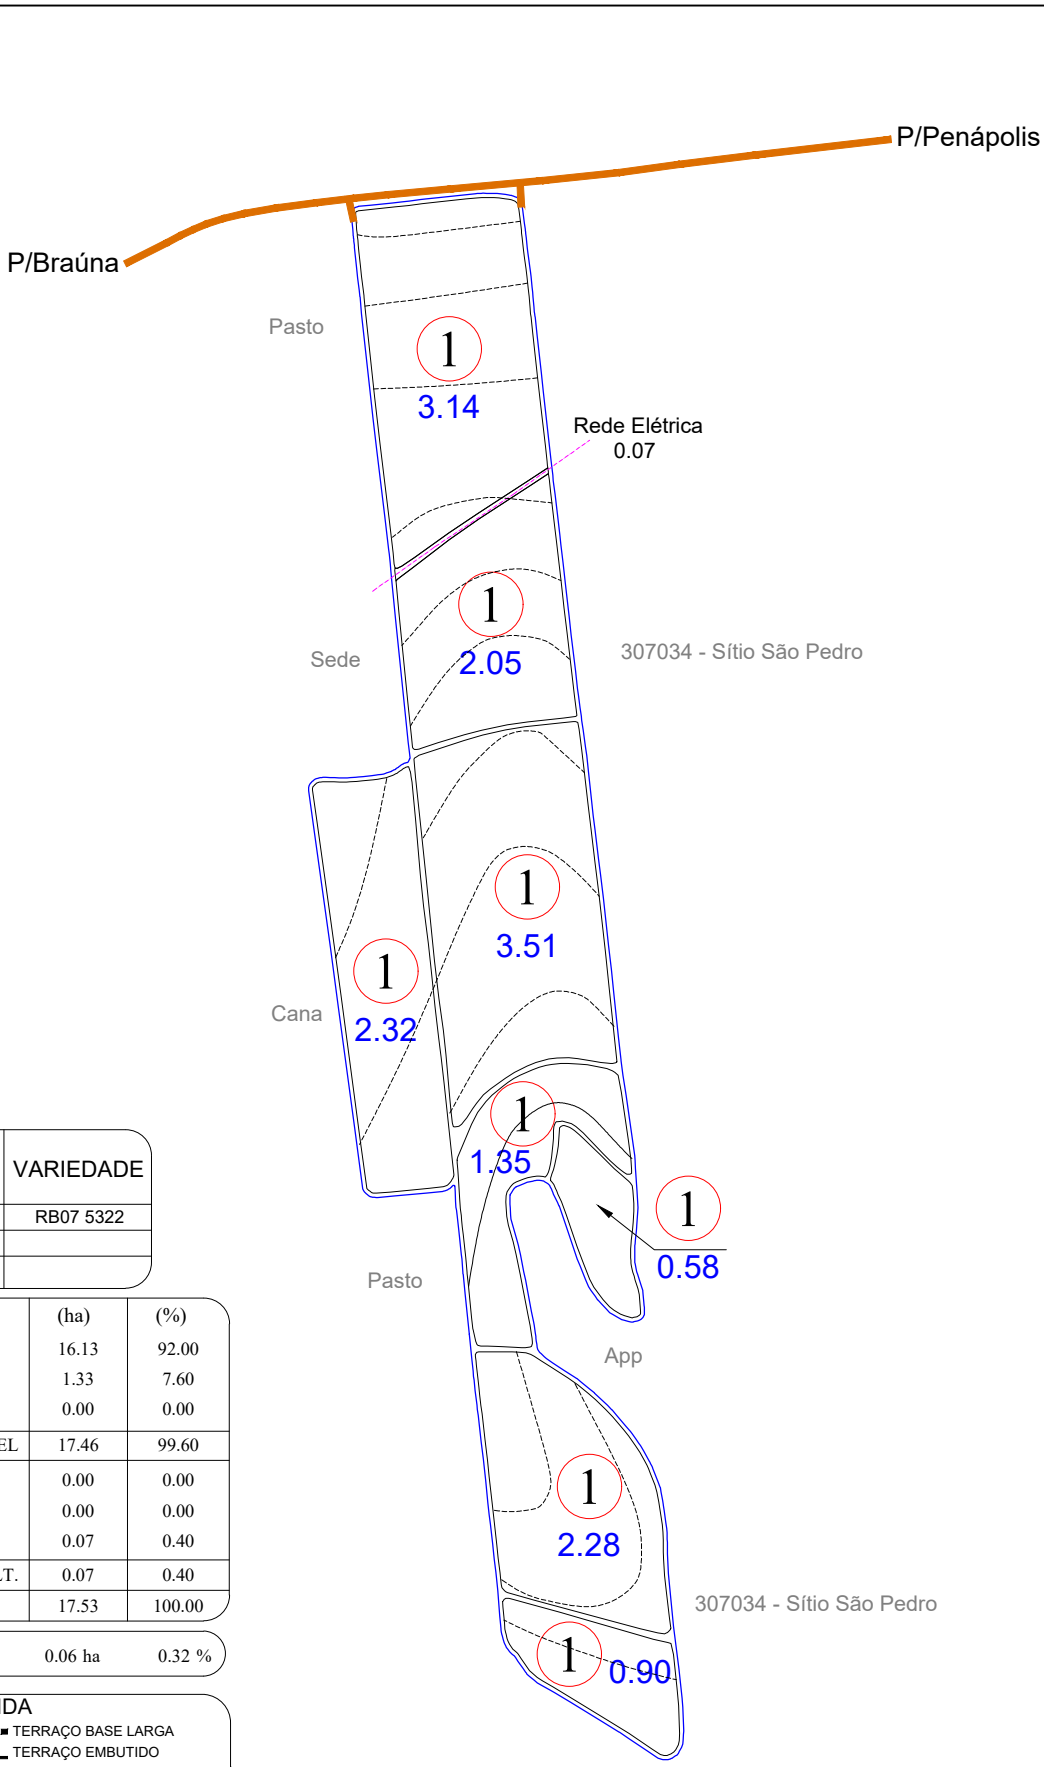

Nº TAL.	DATA PL.	ÁREA (ha)	VARIEDADE
1	04/2026	16.13	RB07 5322
TOTAL PLANTIO		16.13	

ÁREAS	(ha)	(%)
PLANTIO	16.13	92.00
CARREADORES	1.33	7.60
OUTROS	0.00	0.00
SUB TOTAL AGRICULTÁVEL	17.46	99.60
AP.P.	0.00	0.00
ÁRVORES	0.00	0.00
OUTROS	0.07	0.40
SUB TOTAL NÃO AGRICULT.	0.07	0.40
ÁREA TOTAL	17.53	100.00

C. NÍVEL:	242.62 m/l	0.06 ha	0.32 %


LEGENDA

- FAZENDA
- TALHÃO
- REDE ELÉTRICA
- TERRAÇO BASE LARGA
- TERRAÇO EMBUTIDO
- (P.O.A) PATIO DE OPERAÇÃO

ESPAÇAMENTO: 1.50 x 1.50
TIRO MÉDIO ESTIMADO: 111.54 m
D.V: 4.73 %

ESCALA: 1: 6.000

CROQUI DE ACESSO

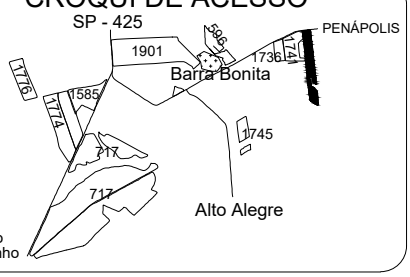

SITIO SÃO FRANCISCO

PROPRIETÁRIO: PAULO RICARDO FERREIRA LOPES
COMPRADOR: CLEALCO
MUNICÍPIO: PENÁPOLIS - SP

DISTÂNCIAS (km):
UNID. I - Asfalto: 31.00 Terra.: 7.70
UNID.I I - Asfalto: 72.50 Terra.: 8.00

COORDENADAS: E(X): 581448.45 N(Y): 7619332.01
LAT: -21°31'36.8382" LONG: -50°12'48.7093"

CLEALCO - AÇÚCAR E ALCOOL S/A - DEPARTAMENTO DE GEOTECNOLOGIA

LEVANTAMENTO VIA:
- SATÉLITE
- GPS / VANT
- GOOGLE

UNIDADE: I
PARTE: A/A
FUNDO AGRÍCOLA: 308231

M:\01-Mapa de safra\Mapas Atualizados\Terceiro\308231 - Sítio São Francisco (Paulo Ricardo Ferreira Lopes)\308231 - Sítio São Francisco (Paulo Ricardo Ferreira Lopes).dwg

Bruno Gamboa 16/09/26