
Clealco
Açúcar, Etanol e Energia

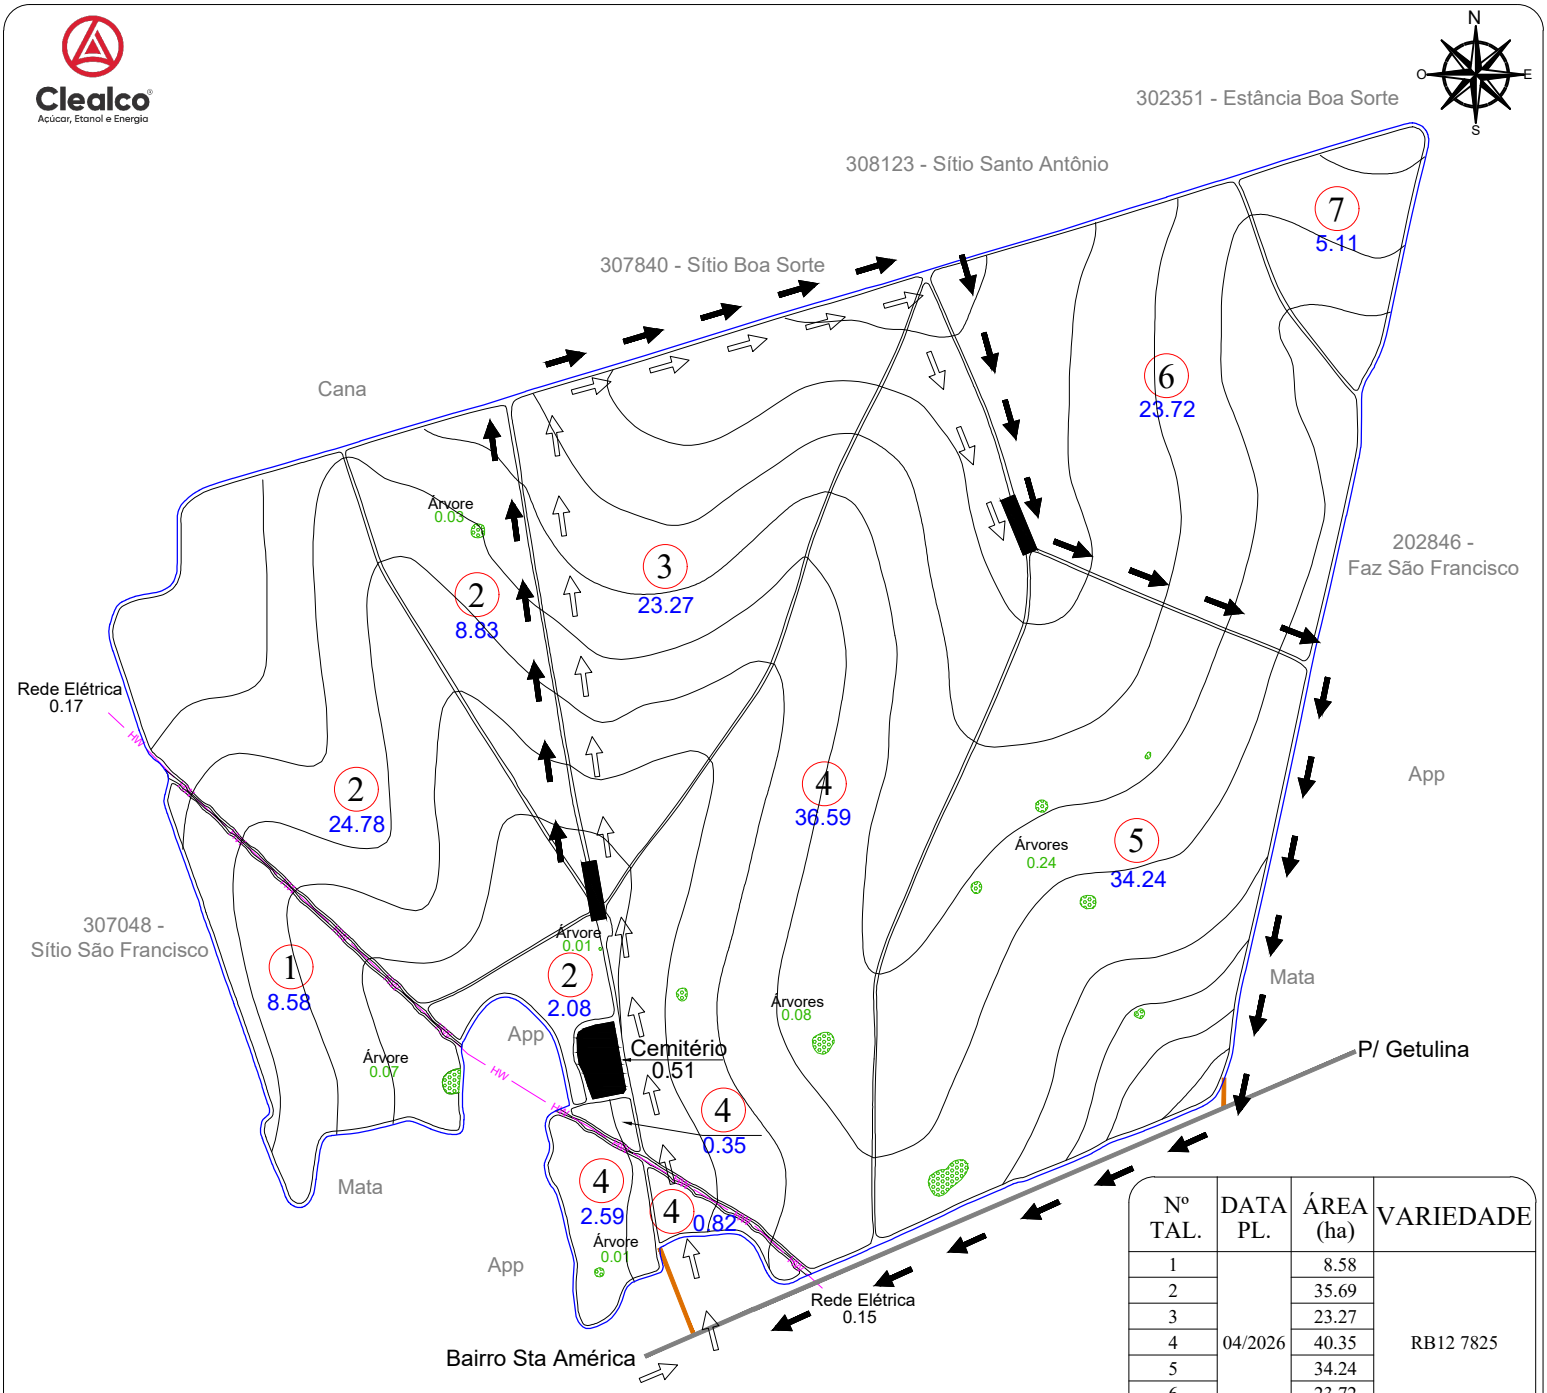

Nº TAL.	DATA PL.	ÁREA (ha)	VARIEDADE
1	04/2026	8.58	RB12 7825
2		35.69	
3		23.27	
4		40.35	
5		34.24	
6		23.72	
7		5.11	
TOTAL PLANTIO		170.96	--------

ÁREAS	(ha)	(%)
PLANTIO	170.96	95.79
CARREADORES	6.25	3.50
OUTROS	0.00	0.00
SUB TOTAL AGRICULTÁVEL	177.21	99.29
AP.P.	0.00	0.00
ÁRVORES	0.44	0.25
OUTROS	0.83	0.47
SUB TOTAL NÃO AGRICULT.	1.27	0.71
ÁREA TOTAL	178.48	100.00

LEGENDA


- FAZENDA
- TALHÃO
- REDE ELÉTRICA
- VAZIO
- TERRAÇO BASE LARGA
- TERRAÇO EMBUTIDO
- (P.O.A) PATIO DE OPERAÇÃO
- CARREGADO

ESPAÇAMENTO: 1.50 x 1.50
TIRO MÉDIO ESTIMADO: 306.34 m
D.V: 4.20 %

C. NÍVEL: 18389.07 m/l 4.23 ha 2.37 %

ESCALA: 1: 10.500

CROQUI DE ACESSO

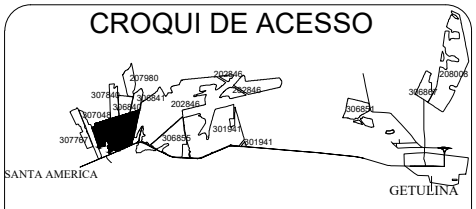

SÍTIO METODIO III

PROPRIETÁRIO: ALVARO METODIO
COMPRADOR: CLEALCO
MUNICÍPIO: GETULINA - SP

DISTÂNCIAS (km):
UNID. I - Asfalto: 82.70 Terra.: 1.10
UNID.I I - Asfalto: 29.20 Terra.: 1.10

COORDENADAS: E(X): 597962.60 N(Y): 7590336.28
LAT: -21°47'16.8384" LONG: -50°3'8.5506"

CLEALCO - AÇÚCAR E ALCOOL S/A - DEPARTAMENTO DE GEOTECNOLOGIA

LEVANTAMENTO VIA:
- SATÉLITE
- GPS / VANT
- GOOGLE

UNIDADE: II
PARTE: A/A
FUNDO AGRÍCOLA: 308239

M:\01-Mapa de safra\Mapas Atualizados\Terceiro\308239 - Sitio Metódio III (Luiz Francisco De Castro Ventura)\308239 - Sitio Metódio III (Luiz Francisco De Castro Ventura).dwg

Bruno Gamboa 27/08/26