
Clealco
Açúcar, Etanol e Energia

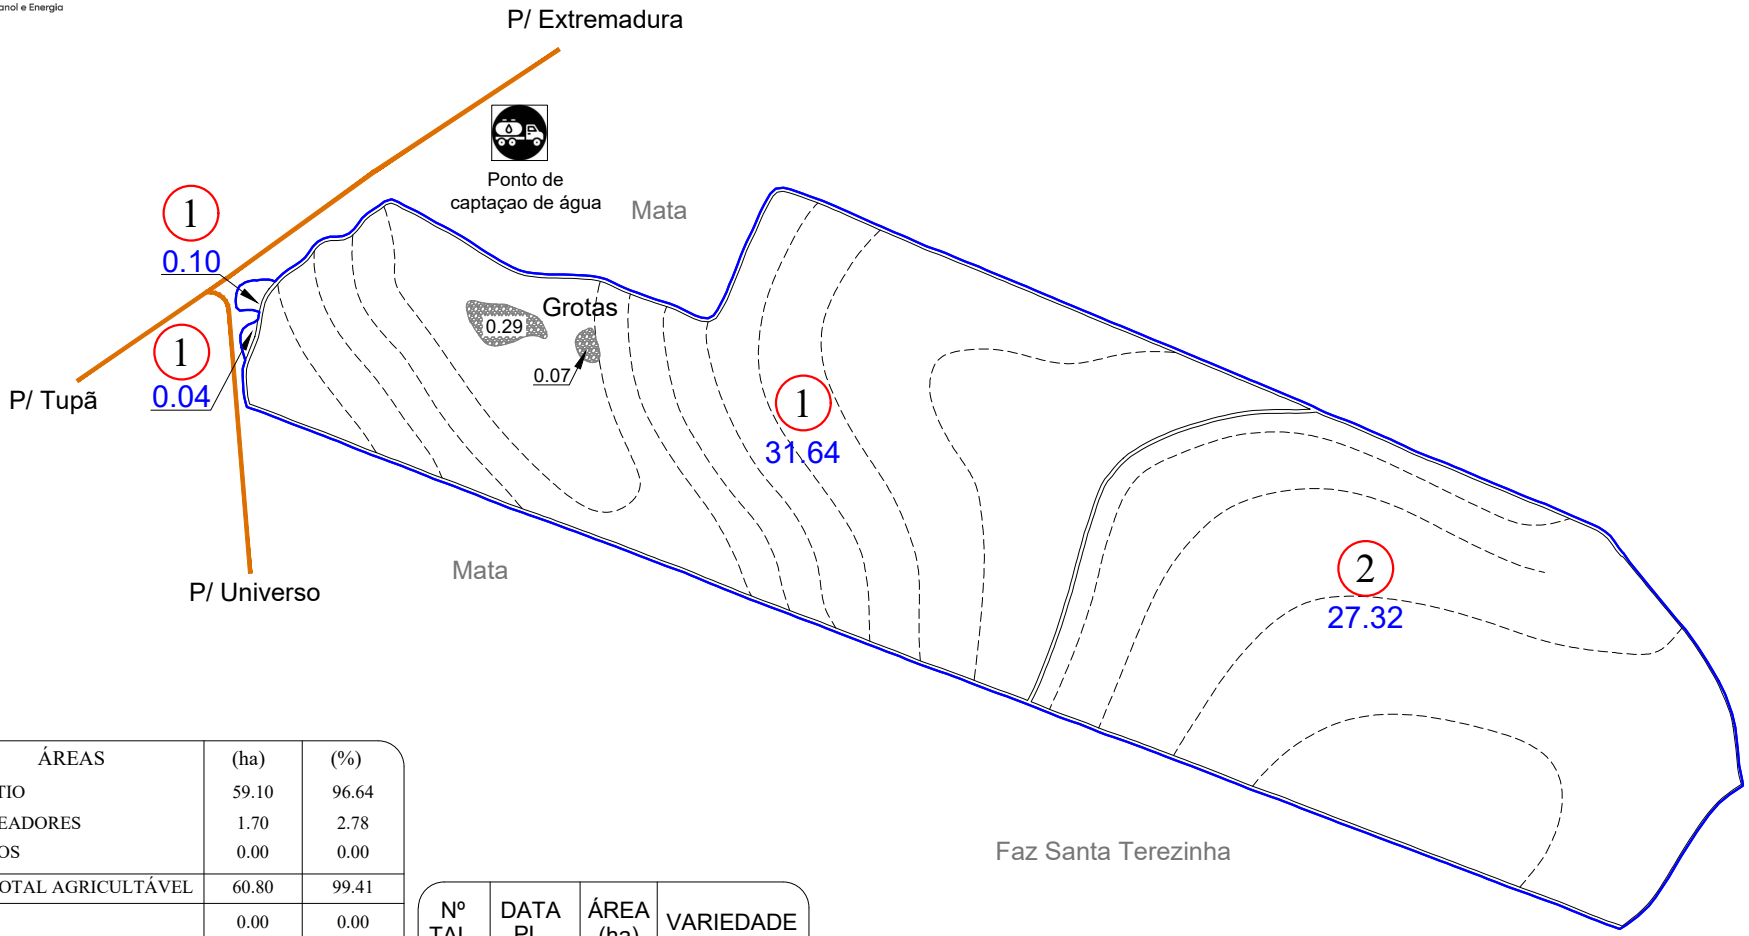

ÁREAS	(ha)	(%)
PLANTIO	59.10	96.64
CARREADORES	1.70	2.78
OUTROS	0.00	0.00
SUB TOTAL AGRICULTÁVEL	60.80	99.41
AP.P.	0.00	0.00
ÁRVORES	0.00	0.00
OUTROS	0.36	0.59
SUB TOTAL NÃO AGRICULT.	0.36	0.59
ÁREA TOTAL	61.16	100.00


Nº TAL.	DATA PL.	ÁREA (ha)	VARIEDADE
1	07/2021	31.78	RB86 7515
2		27.32	
TOTAL PLANTIO		59.10	

ESCALA: 1: 8.500

LEGENDA
- FAZENDA
- TALHÃO
- REDE ELÉTRICA
- TERRAÇO BASE LARGA
- TERRAÇO EMBUTIDO
- VAZIO
- CARREGADO

ESPAÇAMENTO: 1.50 x 1.50
TIRO MÉDIO ESTIMADO: - m
D.V: 3.74 %

CROQUI DE ACESSO

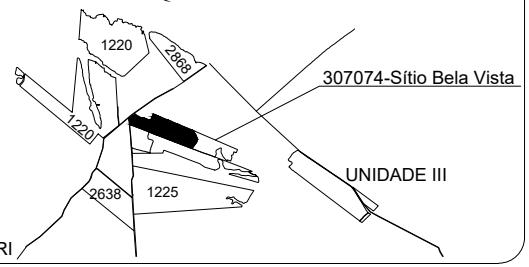

SÍTIO BELA VISTA

PROPRIETÁRIO: MOACIR STEFANELI
COMPRADOR: CLEALCO
MUNICÍPIO: IACRI - SP

DISTÂNCIAS (km):
UNID. I - Asfalto: 37.50 Terra.: 6.50
UNID.I I - Asfalto: 71.00 Terra.: 6.50

COORDENADAS: E(X): 541055.23 N(Y): 7585599.87
LAT: -21°49'58.9500" LONG: -50°36'9.8064"
CLEALCO - AÇÚCAR E ALCOOL S/A - DEPARTAMENTO DE GEOTECNOLOGIA

LEVANTAMENTO VIA:
- SATÉLITE
- GPS / VANT
- GOOGLE

UNIDADE: I
PARTE: A/A
FUNDO AGRÍCOLA: 308257

M:\01-Mapa de safra\Mapas Atualizados\Terceiro\308257 - Sítio Bela Vista (Moacir Stefaneli)\308257 - Sítio Bela Vista (Moacir Stefaneli).dwg

Peterson Santos 30/04/26