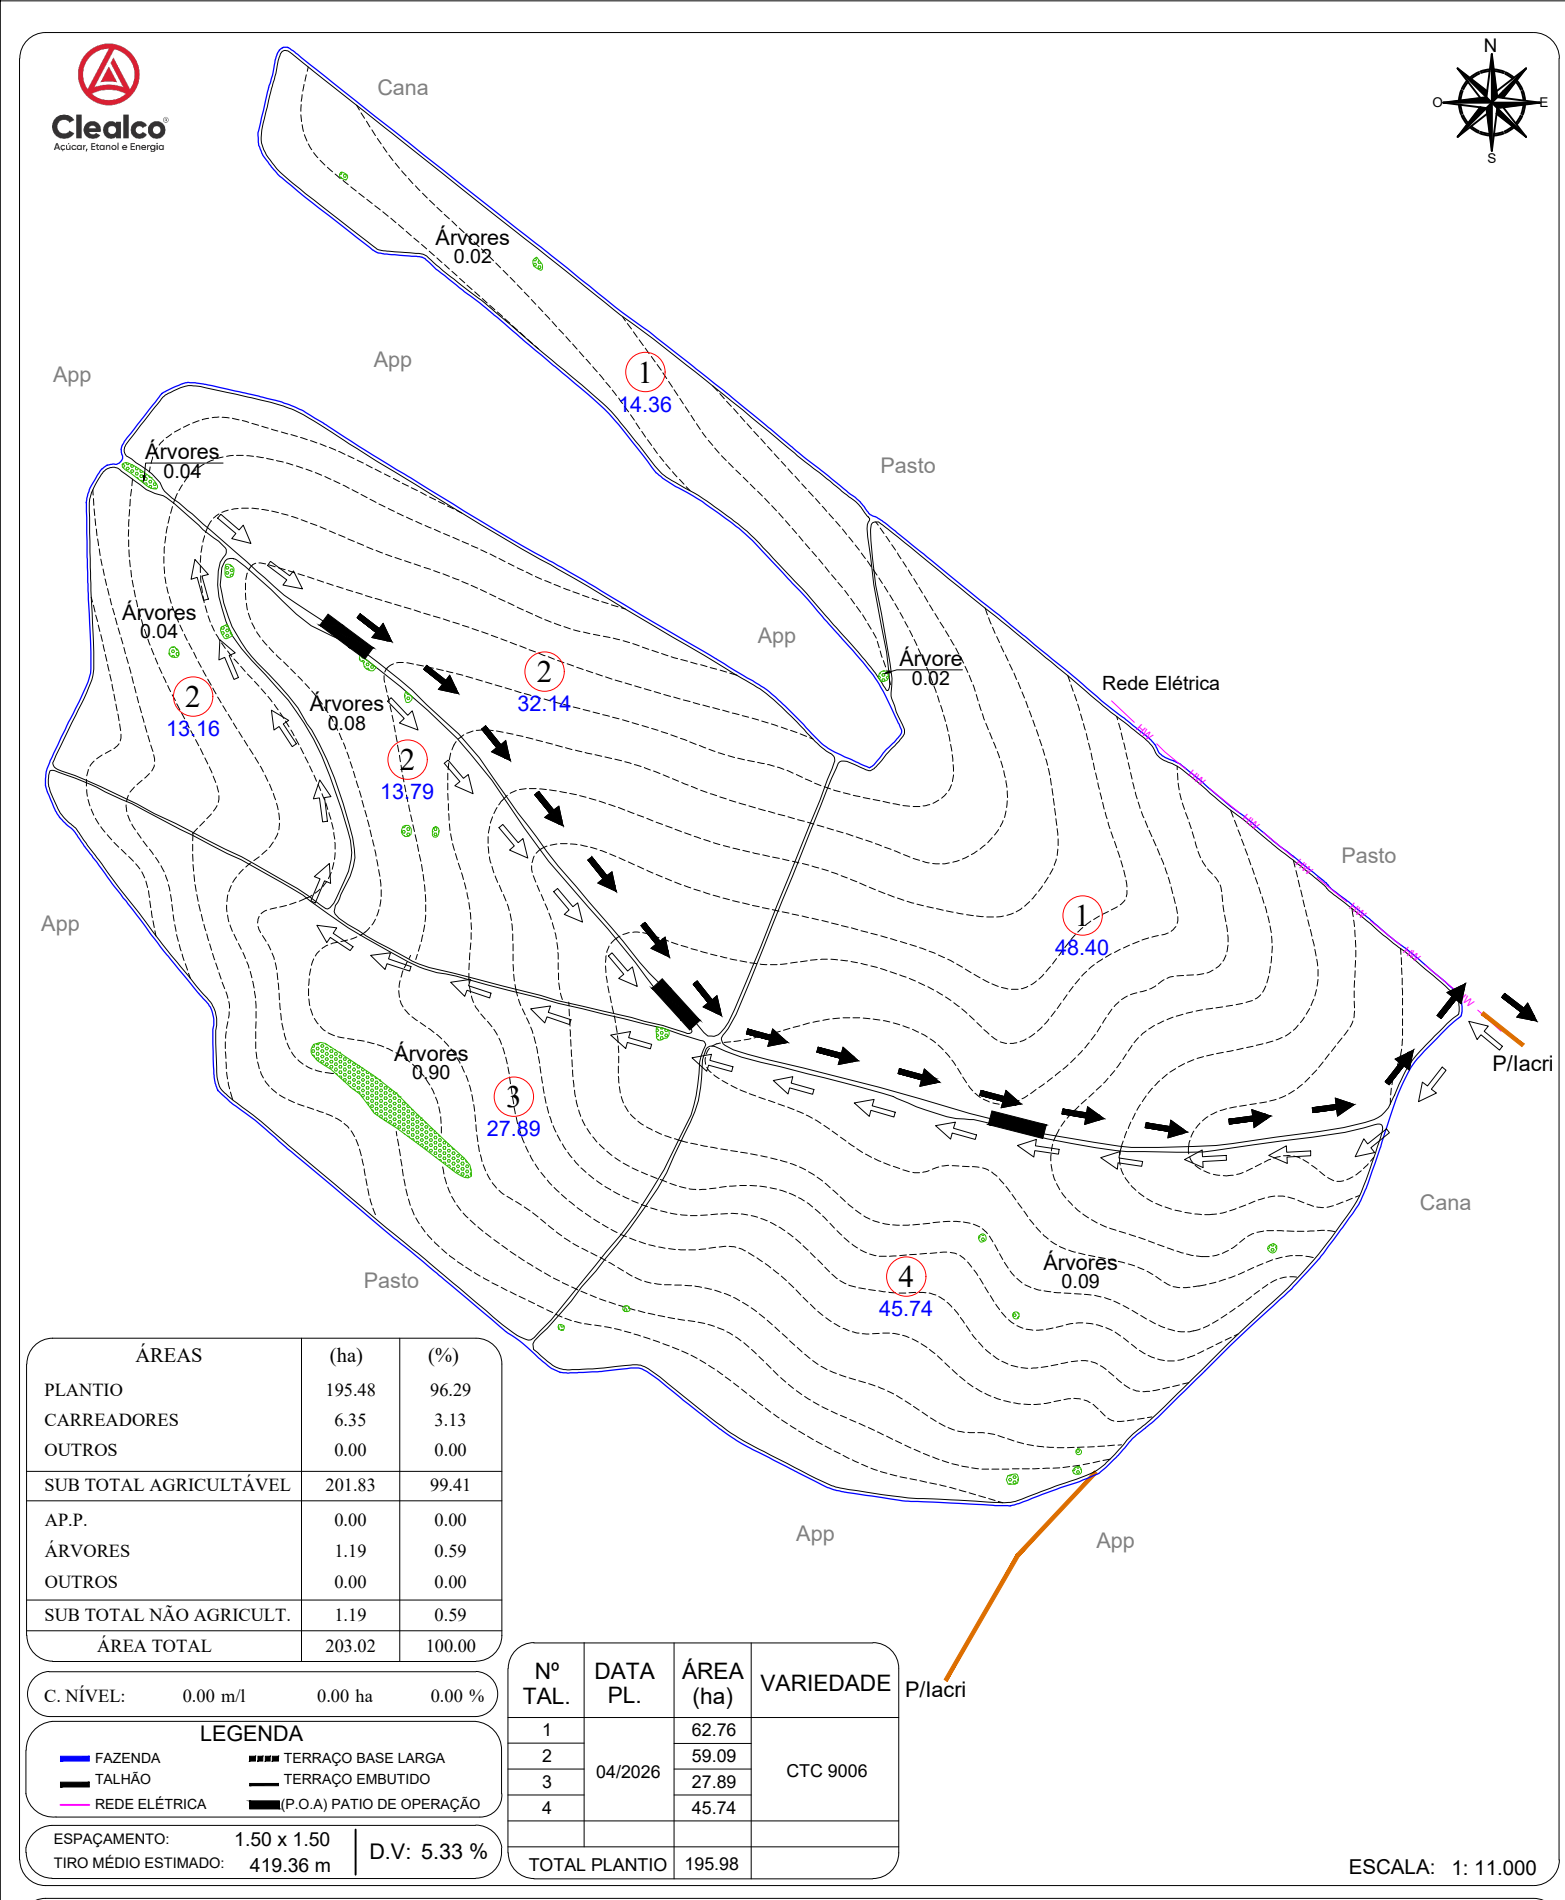


ÁREAS	(ha)	(%)
PLANTIO	195.48	96.29
CARREADORES	6.35	3.13
OUTROS	0.00	0.00
SUB TOTAL AGRICULTÁVEL	201.83	99.41
AP.P.	0.00	0.00
ÁRVORES	1.19	0.59
OUTROS	0.00	0.00
SUB TOTAL NÃO AGRICULT.	1.19	0.59
ÁREA TOTAL	203.02	100.00

C. NÍVEL: 0.00 m/l 0.00 ha 0.00 %

LEGENDA


- FAZENDA
- TALHÃO
- REDE ELÉTRICA
- TERRAÇO BASE LARGA
- TERRAÇO EMBUTIDO
- (P.O.A) PATIO DE OPERAÇÃO

ESPAÇAMENTO: 1.50 x 1.50
TIRO MÉDIO ESTIMADO: 419.36 m
D.V: 5.33 %

Nº TAL.	DATA PL.	ÁREA (ha)	VARIEDADE
1	04/2026	62.76	CTC 9006
2		59.09	
3		27.89	
4		45.74	
TOTAL PLANTIO		195.98	

ESCALA: 1: 11.000

CROQUI DE ACESSO

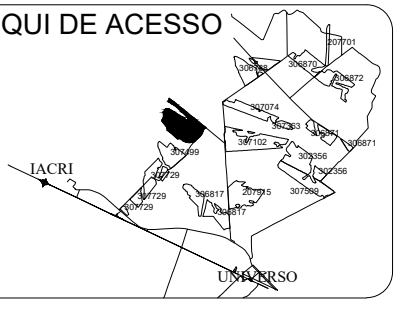

FAZENDA UEYAMA III

PROPRIETÁRIO: CLAUDEMIR STEFANELI
COMPRADOR: CLEALCO
MUNICÍPIO: IACRI - SP

DISTÂNCIAS (km):
UNID. I - Asfalto: 36.50 Terra.: 9.00
UNID.I I - Asfalto: 71.00 Terra.: 9.00

COORDENADAS: E(X): 537817.90 N(Y): 7585035.34
LAT: -21°50'17.5717" LONG: -50°38'2.5331"

CLEALCO - AÇÚCAR E ALCOOL S/A - DEPARTAMENTO DE GEOTECNOLOGIA

LEVANTAMENTO VIA:
- SATÉLITE
- GPS / VANT
- GOOGLE

UNIDADE: I
PARTE: A/A
FUNDO AGRÍCOLA: 308273

M:\01-Mapa de safra\Mapas Atualizados\Terceiro\308273 - Fazenda Ueyama III (Claudemir Stefanelli)\308273 - Fazenda Ueyama III (Claudemir Stefanelli).dwg

Peterson Santos 14/10/2026