
Clealco
Açúcar, Etanol e Energia

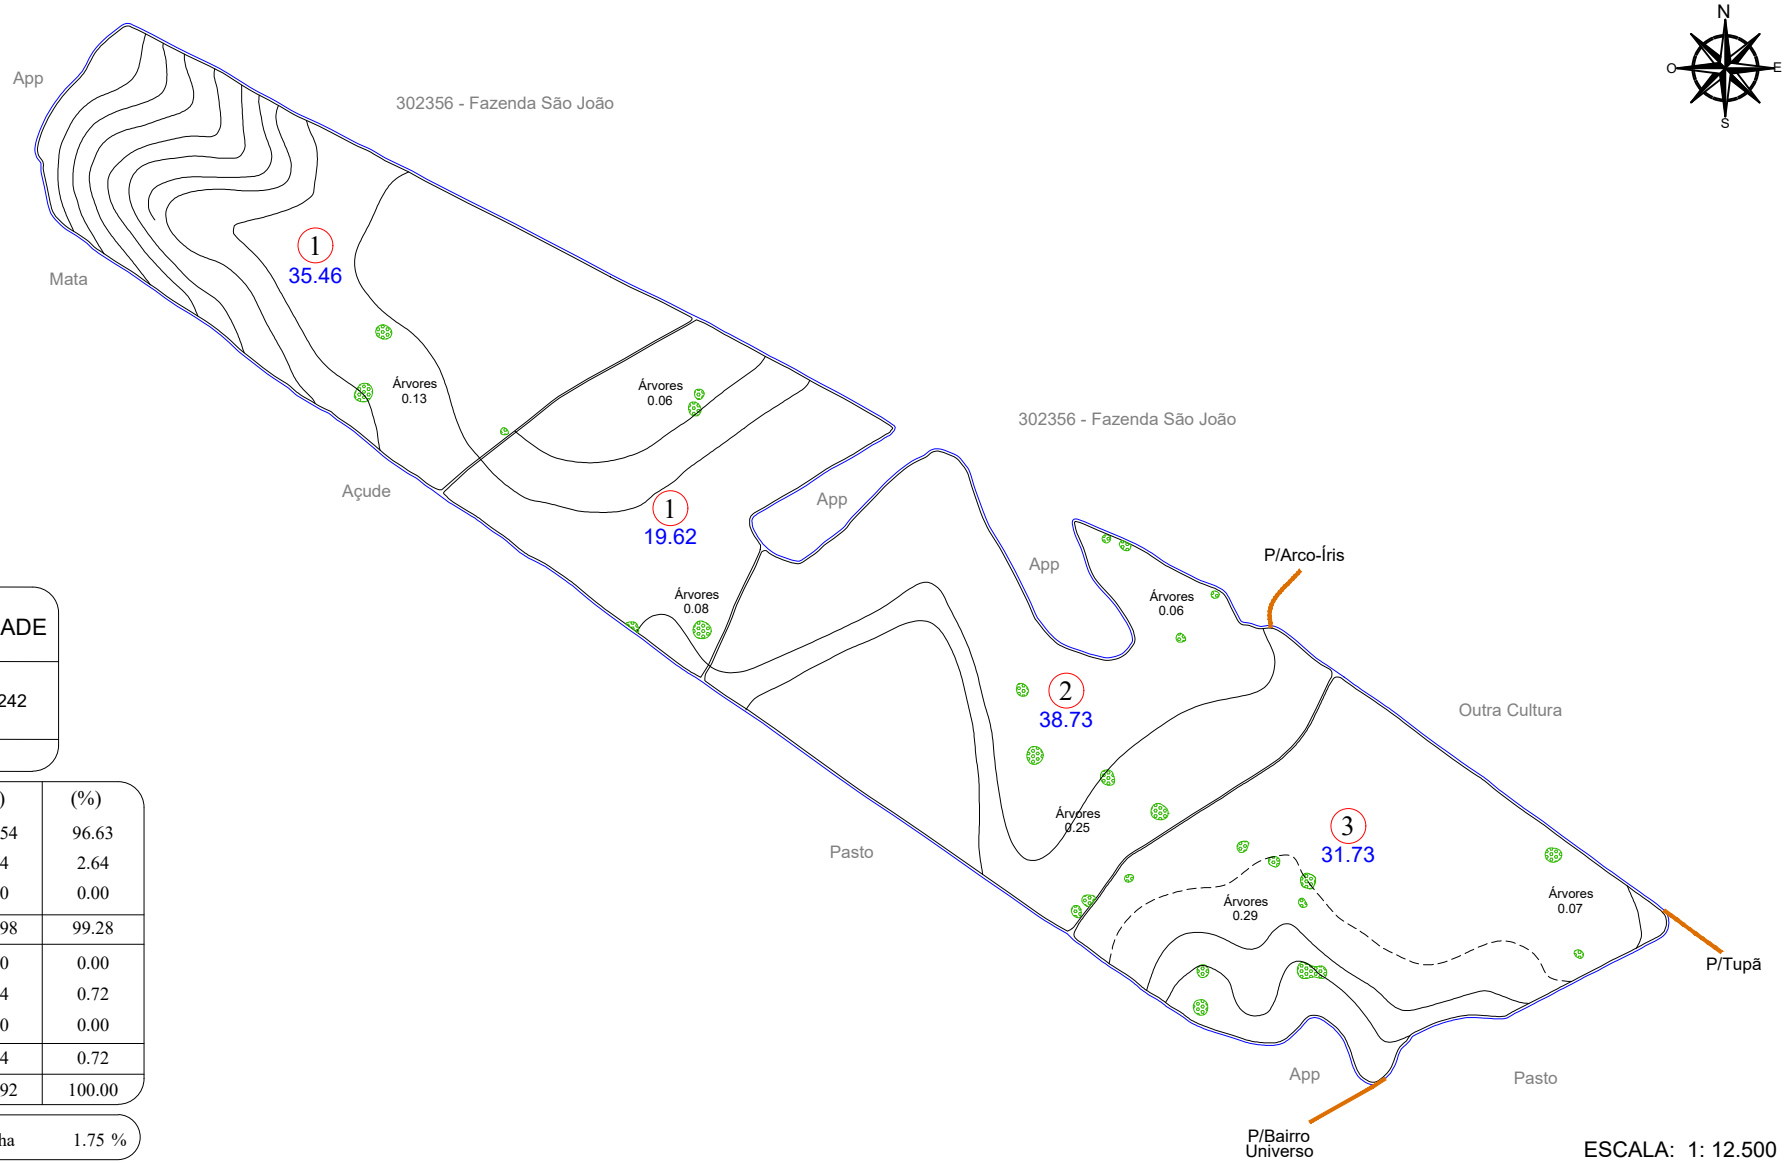

Nº TAL.	DATA PL.	ÁREA (ha)	VARIEDADE
1	05/2023	55.08	RB97 5242
2		38.73	
3		31.73	
TOTAL PLANTIO		125.54	

ÁREAS	(ha)	(%)
PLANTIO	125.54	96.63
CARREADORES	3.44	2.64
OUTROS	0.00	0.00
SUB TOTAL AGRICULTÁVEL	128.98	99.28
AP.P.	0.00	0.00
ÁRVORES	0.94	0.72
OUTROS	0.00	0.00
SUB TOTAL NÃO AGRICULT.	0.94	0.72
ÁREA TOTAL	129.92	100.00

C. NÍVEL: 9906.24 m/l 2.28 ha 1.75 %


ESCALA: 1: 12.500

LEGENDA

- FAZENDA
- TALHÃO
- REDE ELÉTRICA
- TERRAÇO BASE LARGA
- TERRAÇO EMBUTIDO
- VAZIO
- CARREGADO

ESPAÇAMENTO: 1.50 x 1.50
TIRO MÉDIO ESTIMADO: 000.00 m
D.V: 5.11 %

CROQUI DE ACESSO

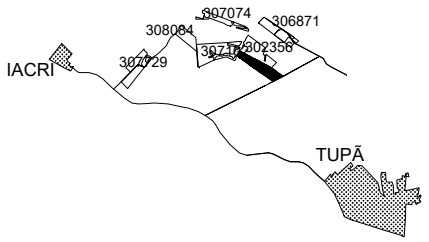

FAZENDA PRIMAVERA

PROPRIETÁRIO: CLAUDEMIR STEFANELLI
COMPRADOR: CLEALCO
MUNICÍPIO: IACRI - SP

DISTÂNCIAS (km):
UNID. I - Asfalto: 36.10 Terra.: 11.30
UNID.I I - Asfalto: 29.00 Terra.: 25.40

COORDENADAS: E(X): 543608.19 N(Y): 7582301.61
LAT: -21°51'46.0023" LONG: -50°34'40.5588"
CLEALCO - AÇÚCAR E ALCOOL S/A - DEPARTAMENTO DE GEOTECNOLOGIA

LEVANTAMENTO VIA:
SATÉLITE
GPS / VANT
GOOGLE

UNIDADE: II
PARTE: A/A
FUNDO AGRÍCOLA: 308275

M:\01-Mapa de safra\Mapas Atualizados\Terceiro\308275 - Fazenda Primavera (Claudemir Stefanelli)\308275 - Fazenda Primavera (Claudemir Stefanelli).dwg

Peterson Santos 15/10/26