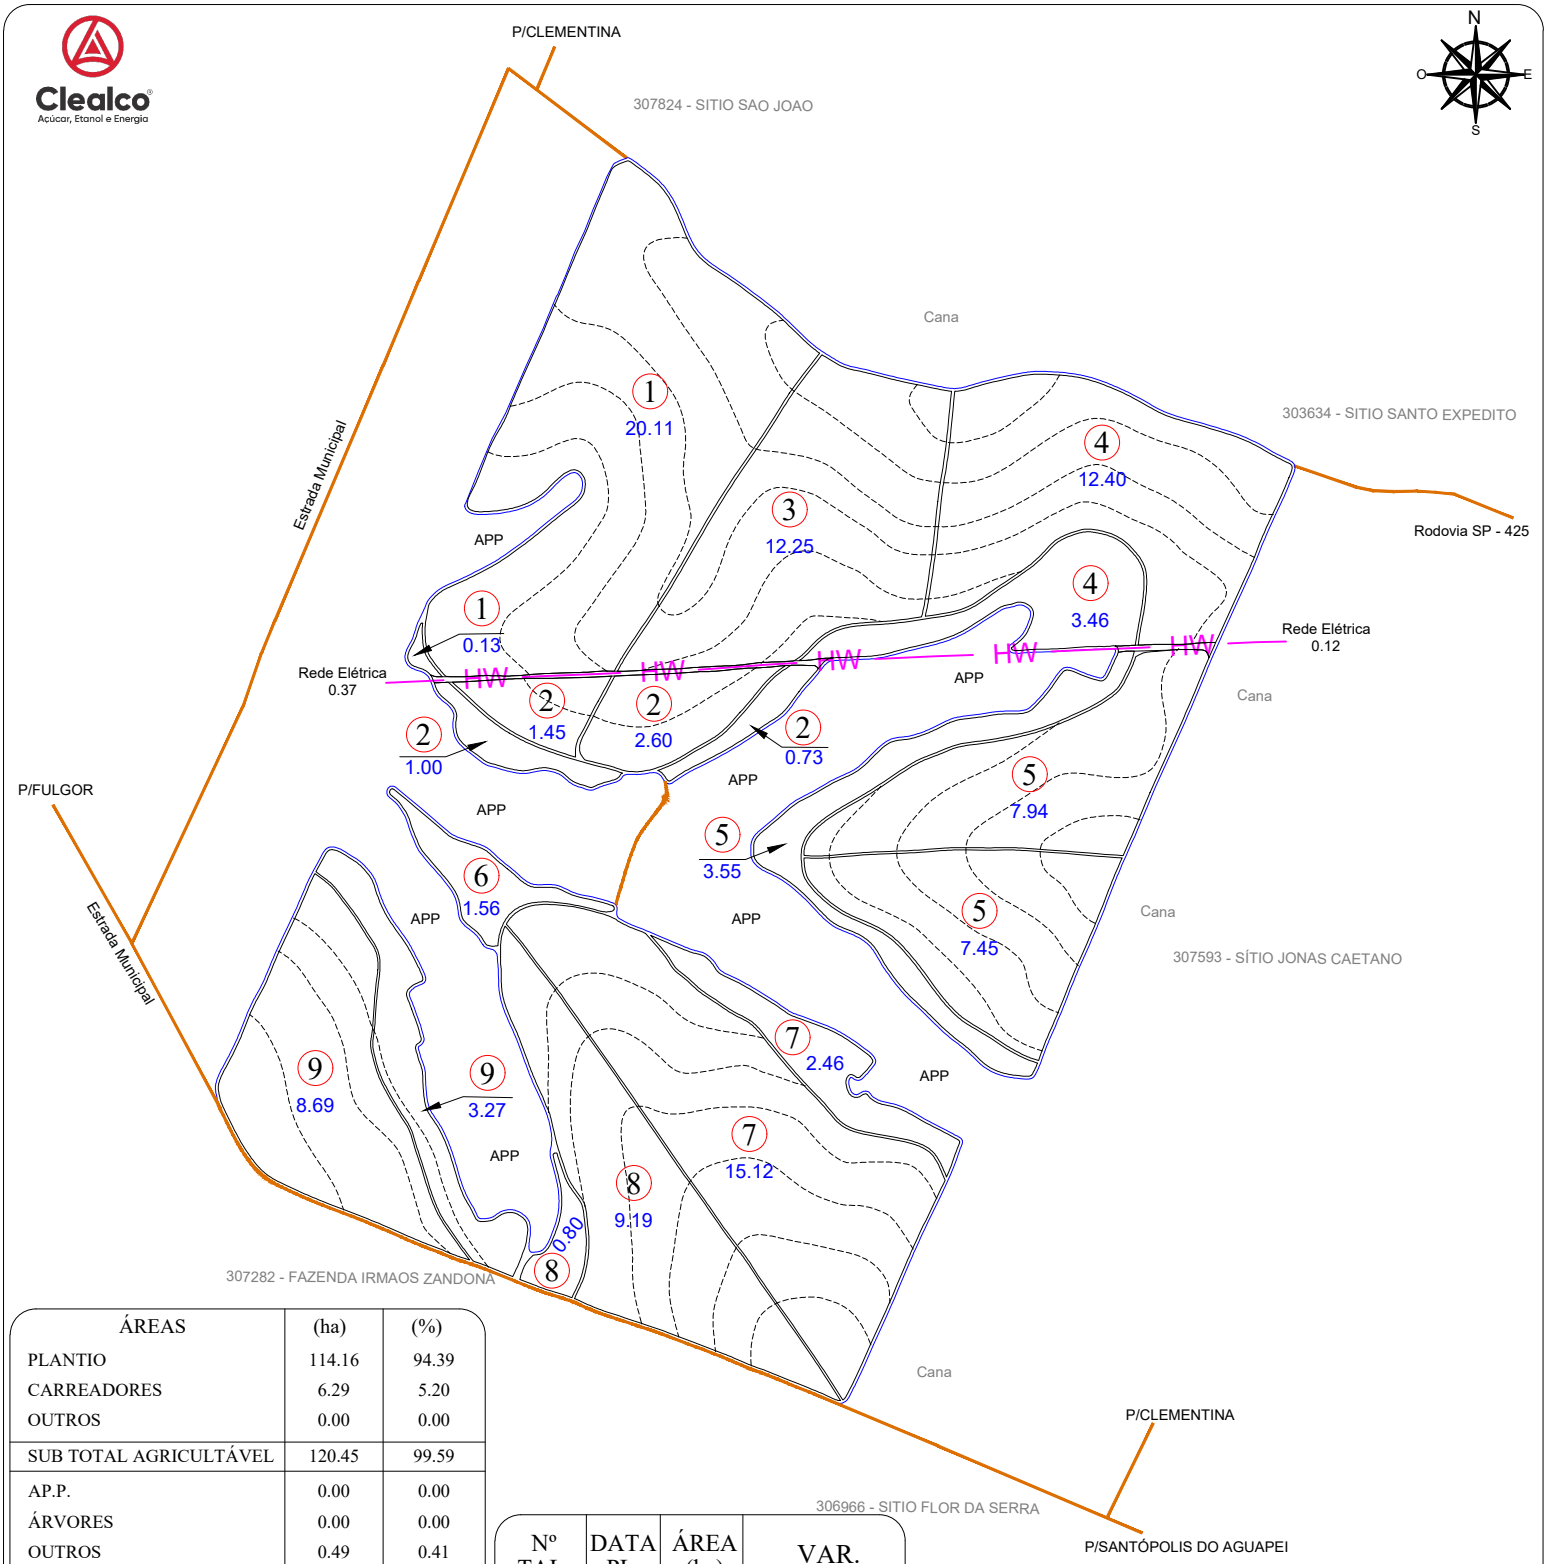


ÁREAS	(ha)	(%)
PLANTIO	114.16	94.39
CARREADORES	6.29	5.20
OUTROS	0.00	0.00
SUB TOTAL AGRICULTÁVEL	120.45	99.59
AP.P.	0.00	0.00
ÁRVORES	0.00	0.00
OUTROS	0.49	0.41
SUB TOTAL NÃO AGRICULT.	0.49	0.41
ÁREA TOTAL	120.94	100.00

C. NÍVEL: 13250.89 m/l 3.05 ha 2.52 %

LEGENDA


- FAZENDA
- TALHÃO
- REDE ELÉTRICA
- TERRAÇO BASE LARGA
- TERRAÇO EMBUTIDO
- (P.O.A) PATIO DE OPERAÇÃO

ESPAÇAMENTO: 1.50 x 1.50
TIRO MÉDIO ESTIMADO: 213.44m
D.V: 5.65 %

Nº TAL.	DATA PL.	ÁREA (ha)	VAR.
1	06/2023	20.24	RB975242
2		5.78	
3		12.25	
4		15.86	
5		18.94	
6		1.56	
7		17.58	
8		9.99	
9		11.96	
TOTAL PLANTIO		114.16	--------

ESCALA: 1: 11.000

CROQUI DE ACESSO

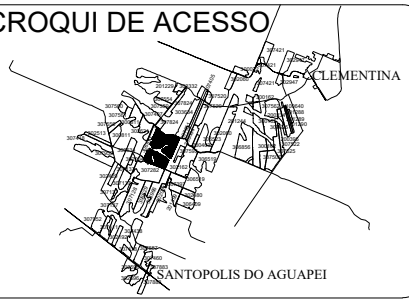

SÍTIO SÃO JUDAS TADEU

PROPRIETÁRIO: RENATO CESAR RAMIRO
COMPRADOR: CLEALCO
MUNICÍPIO: CLEMENTINA - SP

DISTÂNCIAS (km):
UNID. I - Asfalto: 6.50 Terra.: 5.50
UNID.I I - Asfalto: 54.00 Terra.: 5.50

COORDENADAS: E(X): 550354.89 N(Y): 7612676.09
LAT: -21°35'17.4435" LONG: -50°30'48.8154"

CLEALCO - AÇÚCAR E ALCOOL S/A - DEPARTAMENTO DE GEOTECNOLOGIA

LEVANTAMENTO VIA:
- SATÉLITE
- GPS / VANT
- GOOGLE

UNIDADE: I
PARTE: A/A
FUNDO AGRÍCOLA: 310454

M:\01-Mapa de safra\Mapas Atualizados\Terceiro\310454 - Sítio São Judas Tadeu (Renato Cesar Ramiro)\310454 - Sítio São Judas Tadeu (Renato Cesar Ramiro).dwg

Bruno Gamboa 00/08/25